



DRAWING

REV DESCRIPTION	DATE	REV NO
1.	12-11-2025	REV 00

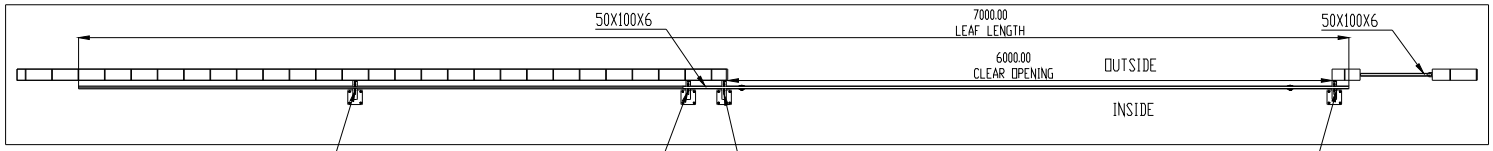


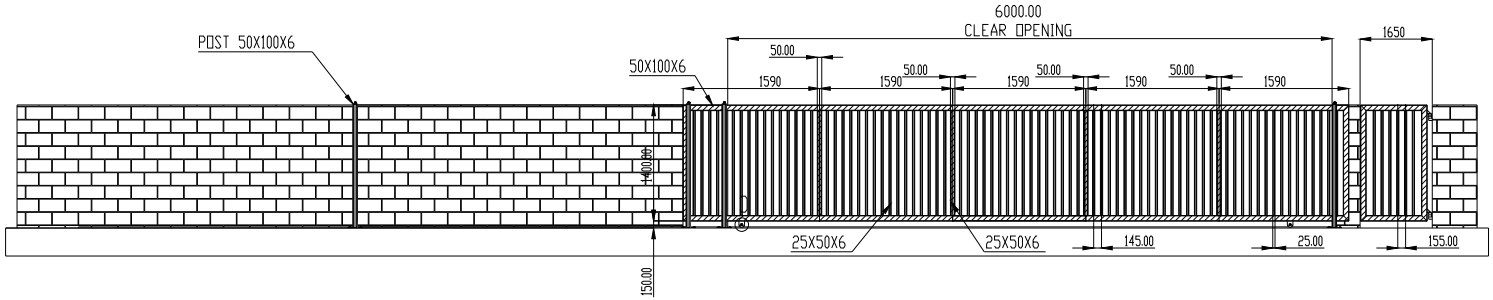

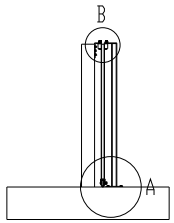


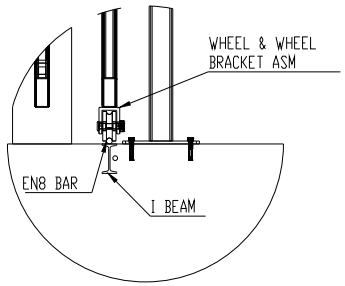

DETAIL A
SCALE 1 : 11

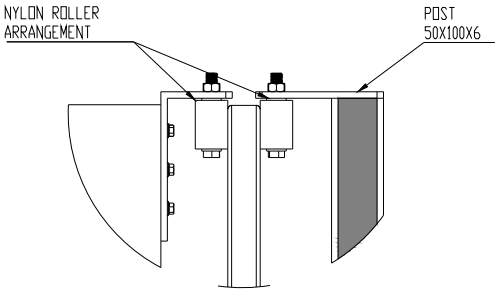

DETAIL B
SCALE 1 : 5

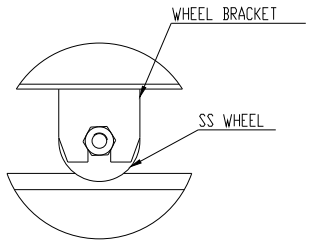

DETAIL C
SCALE 1 : 4

SS WHEEL ARRANGEMENT

NOTE :

SPECIAL INSTRUCTION'S :

TITLE - DOOR AUTOMATION			
DWG NO - NTPL-000-PM			
	NAME	SIGNATURE	DATE
DRAWN	V.W.		12-11-2025
CHK'D	B.S.		13-11-2025
APPV'D	V.T.		13-11-2025
If any queries contact - Design@nihva.com			
ALL DIMENSION ARE IN mm			A2

NIHVA
NIHVA Technologies Pvt. Ltd.

NIHVA TECHNOLOGIES
PVT.LTD.PUNE
Website - www.nihva.com

PRODUCT - SLINDING GATE	
PROJECT NO - NTPL-000-PM	REVISION - 00
SITE LOCATION -	WEIGHT -
MATRIAL -	QTY - 1
PROJECTION METHOD	SCALE :
	SHEET 1 OF 1