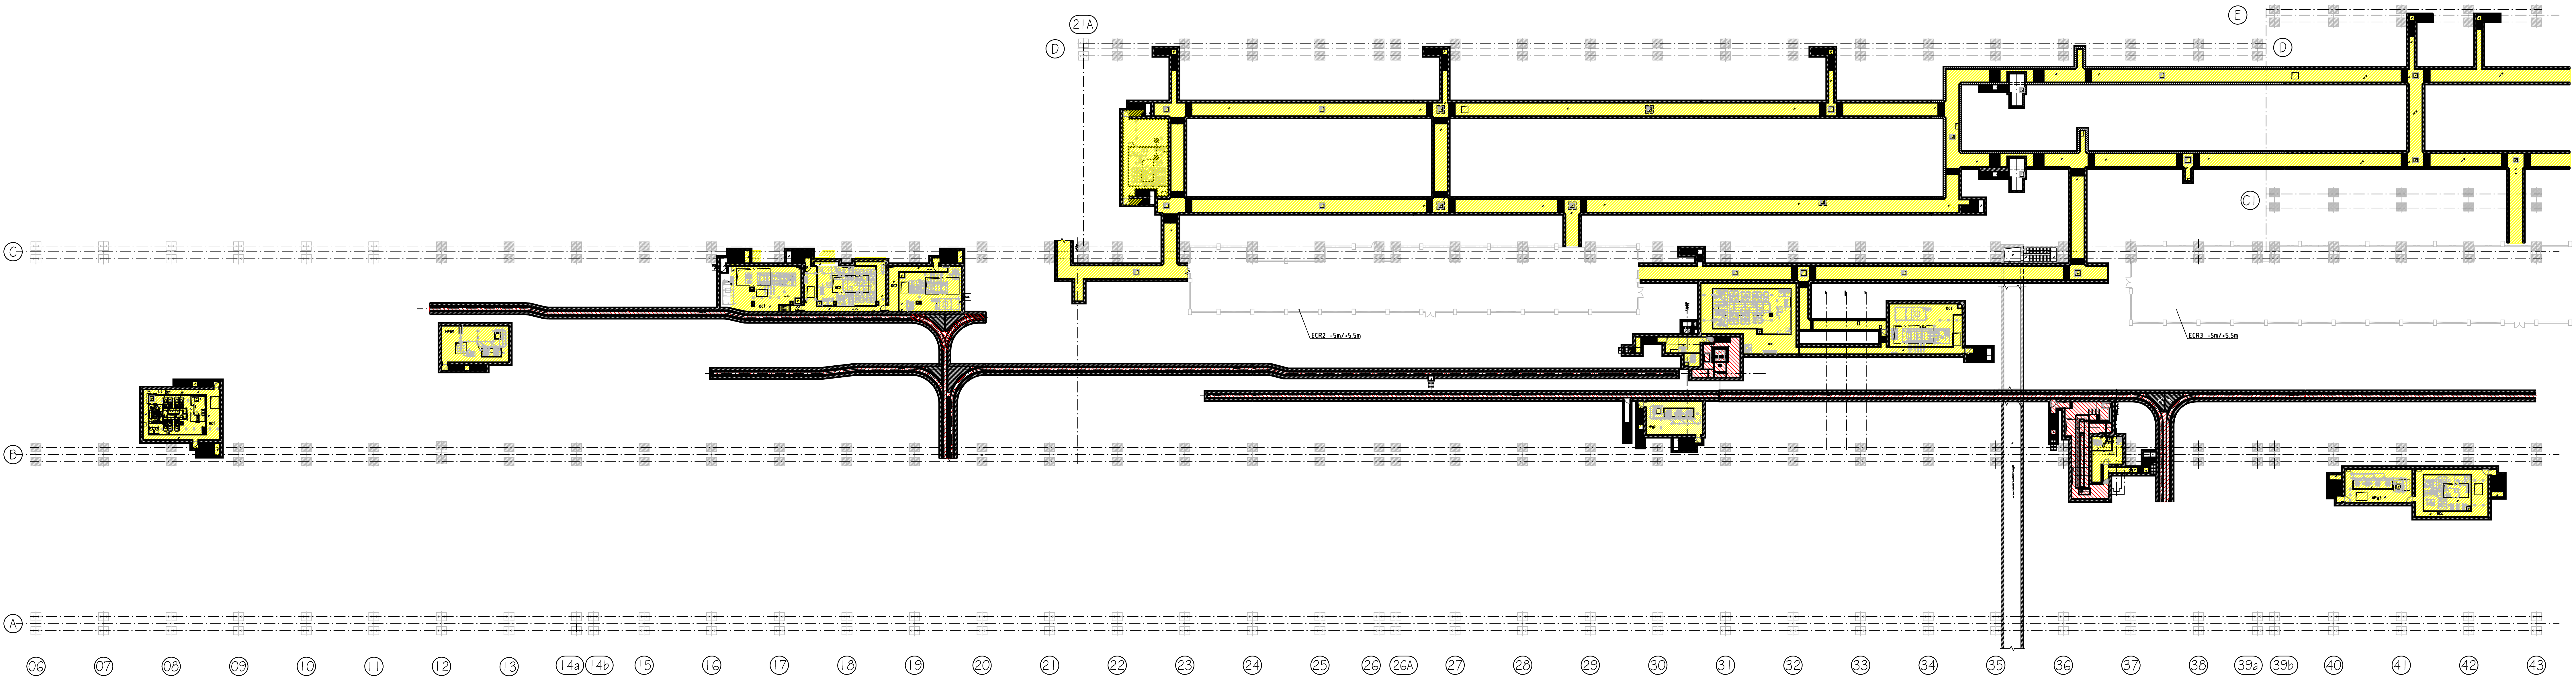

Working Areas

1	loading of beams and blanks	13	activities during straight.roll changing
2	change of spraying rings	14	inspection beams
3	Activities during mill stand changing	15	installation of comb
4	Inspection under load	16	preparation labeling
5	preparation works for mill stand changing	17	adjusting stopper
6	change of saw blade	18	change of coils (bundling area)
7	preparation saw blade	19	unloading of bundles
8	change of chip bucket	20	removal of short length
9	change of scrap bucket	21	repairing of beams
10	handling of sample	22	preparation of rolls, chocks and guides
11	testing of sample (laboratory)	23	operating and control
12	preparation straightening rolls		

GATE

GATE WITH MECH. LOCKING DEVICE

GATE WITH ELECT. LOCKING DEVICE

DOOR WITH MECH. LOCKING DEVICE

DOOR WITH ELECT. LOCKING DEVICE

DOOR

DOOR WITH MECH. LOCKING DEVICE

DOOR WITH ELECT. LOCKING DEVICE

▨ DANGER ZONE 1
No access while unit is in operation.

▨ DANGER ZONE 2
Access only to qualified and authorized persons possible
In defined operating states.
High Residual Risks
Note safety Instructions In operating and maintenance manual.

▨ DANGER ZONE 3
Access only to qualified and authorized persons possible
In defined operating states.
Low Residual Risks
Note safety instructions in operating and maintenance manual.

▨ DANGER ZONE 4
Permanente working place:
Unrestricted access possible while unit is in operation.
Note general safety instructions.

▨ WORKING PLACE
Part of no access zone, that can be entered by trained operators
under particular conditions only
Note safety Instructions In operating and maintenance manual.

REQUEST-/
ACKNOWLEDGEMENT BUTTON

EMERGENCY STOP

ACKNOWLEDGEMENT BUTTON

→ ESCAPE ROUTES

RAILING

REMOVABLE RAILING

FENCE

REMOVABLE FENCE

REMOVABLE CHAIN

LIGHT CURTAIN

Positions of crossovers must be in correspondence
with the General Routing Plan (by Customer)

This safety layout must be considered in coherence
with safety Instructions in Operation and Maintenance Manual.
(Especially Chapter A2)

9463 0000 / RAILBHIL

CATEGORY OF DRWG. APPROVAL INFORMATION REFERENCE RECORD CONSTRUCTION

SAIL

BHILAI STEEL PLANT, BHILAI, CHATTISGARH
7.0 MTPA EXPANSION

मेकॉन लिमिटेड
MECON LIMITED

VENSDOR'S NAME: SMS Meer/SMS Meer India/ABB
PACKAGE DESCRIPTION: UNIVERSAL RAIL MILL (Pkg No-047)
TITLE OF DRAWING. SAFETY LAYOUT, -5000
SCALE-
VENDOR'S DRG NO.-
PROJECT DRG. NO. BSP-SMS Meer-08-047-21-120-50-BE-06603

Fertigungsvorschriften
Manufacturing Instructions
SN 200

Ursprung / Origin
Fertiggewicht
Finished weight
kg
Modell-Nr.
Pattern-No.
Werkstoff / Material
Projektionsmethode 1
First angle projection method
ISO 128

	Datum Date	Name
Bearb. Drawn	30.03.12	Fryen
Geprüft Checked	30.03.12	Prätzel
Norm Stand		

Aus-gabe
Issue | Änderung
Revision | Datum
Date | Name

Typ
Type SAFETY LAYOUT
Benennung
Sicherheitslayout -5000
Title
SAFETY LAYOUT -5000
Maßstab
Scale
1:200

SMS
MEER
SMS group

Sach-Nr. Drawing-No.
0100133-00.603
Blatt
Sheet 3
4 Blätter
Sheets

Ersatz für:/Supersedes:
Ersetzt durch:/Superseded by:

A0

Diese Zeichnung und alle darauf enthaltenen Informationen sind vertraulich. This drawing and all information on it is confidential.

The reproduction, distribution and utilization of this document as well as the disclosure of its content to others without prior explicit written consent of SMS Meer GmbH is prohibited. Holder has to protect this document against unauthorized withdrawal of third parties. Offenders will be held liable for the payment of damages. All rights reserved in case of patent/utility model/trademark protection.