


Weitergabe sowie Vervielfältigung dieses Dokuments, Verwertung und Mitteilung seines Inhalts sind nur nach vorheriger ausdrücklicher schriftlicher Zustimmung von SMS Meer GmbH gestattet. Das Dokument ist vor unberechtigtem Zugriff Dritter zu schützen. Zuwiderhandlungen verpflichten zu Schadensersatz. Alle Rechte aus Patent-/Gebrauchsmuster-/Markenschutz vorbehalten.

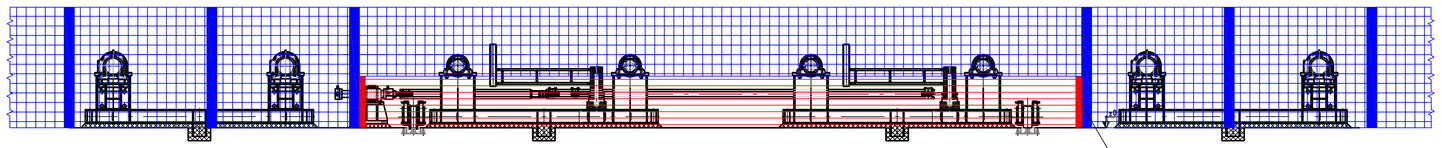

Light Barrier
LB-L01-11

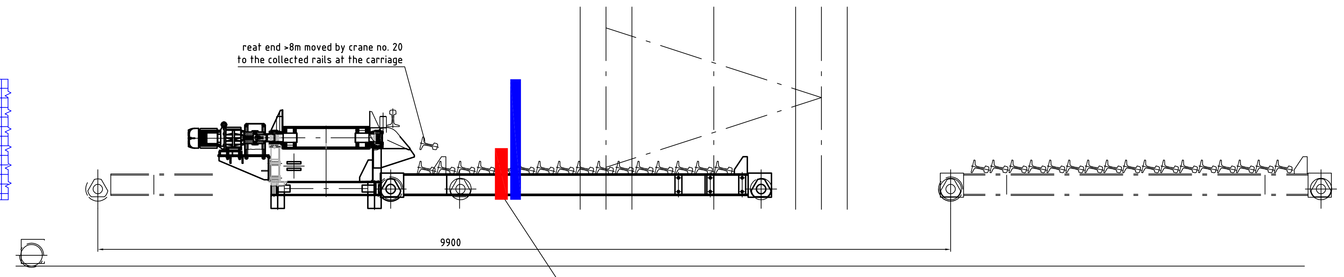

Light Barrier
LB-L01-11

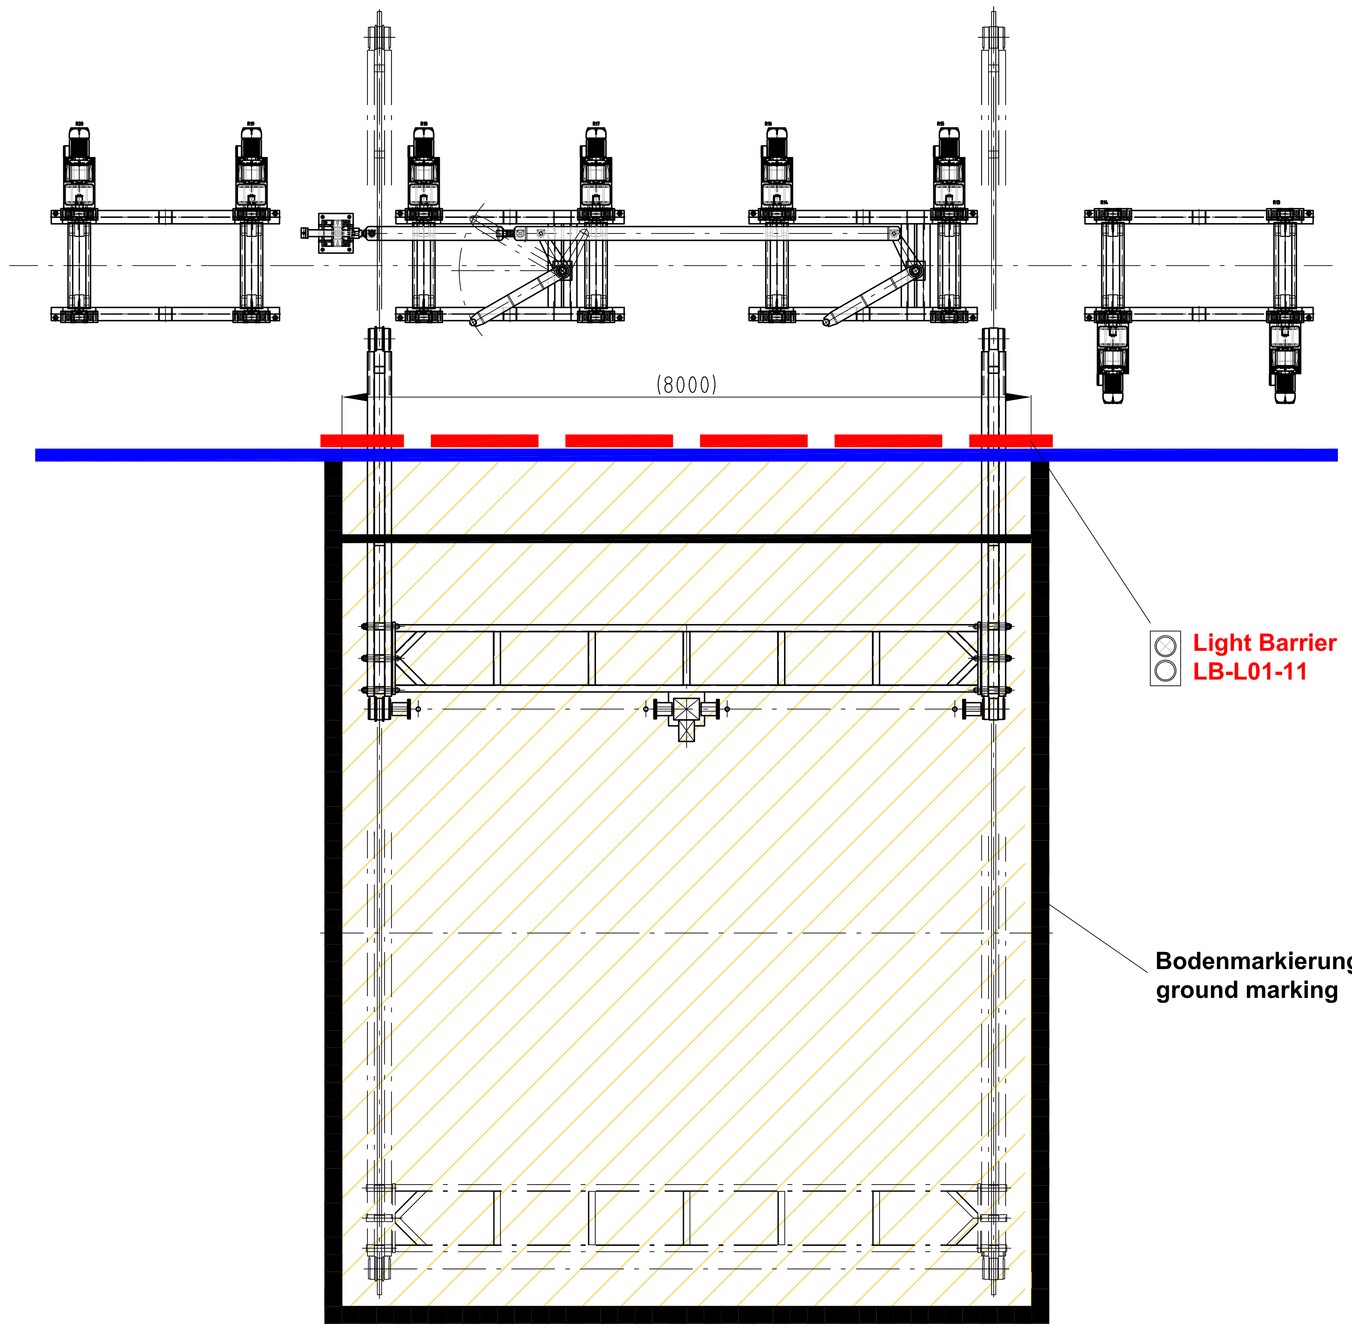

Light Barrier
LB-L01-11

Bodenmarkierung
ground marking

9463 0000 / RAILBHIL

CATEGORY OF DRWG.	APPROVAL	INFORMATION	REFERENCE	RECORD	CONSTRUCTION

BHILAI STEEL PLANT, BHILAI, CHATTISGARH
7,0 MTPA EXPANSION

मेकॉन लिमिटेड
MECON LIMITED

VENSDOR'S NAME: SMS Meer/SMS Meer India/ABB

PACKAGE DESCRIPTION: UNIVERSAL RAIL MILL (Pkg No-047)

TITLE OF DRAWING. PARTITION 7,8 SAFETY LAYOUT

SCALE-

VENDOR'S DRG NO.-

PROJECT DRG. NO. BSP-SMS Meer-08-047-21-130-35-BE-06655 REV. -

Fertigungsvorschriften / Manufacturing Instructions: SN 200

Ursprung / Origin

Fertiggewicht / Finished weight: kg

Modell-Nr. / Pattern-No.

Werkstoff / Material

Projektionsmethode 1 / First angle projection method — ISO 128

	Datum / Date	Name
Bearb. / Drawn	19.09.11	Prätzel
Geprüft / Checked	19.09.11	Prätzel
Norm. Stand		

Typ / Type

Benennung: TEILBEREICH, 7,8

Title: PARTITION 7,8

Maßstab / Scale: 1:50

Sach-Nr.: Drawing-No.: 0100133-00.655

Blatt / Sheet 03 — 03 Blätter / Sheets

Ersatz für / Supersedes:

Ersetzt durch / Superseded by:

Ausgabe / Issue	Änderung / Revision	Datum / Date	Name

SMS MEER — SMS group

The reproduction, distribution and utilization of this document as well as the disclosure of its content to others without prior explicit written consent of SMS Meer GmbH is prohibited. Holder has to protect this document against unauthorized withdrawal of third parties. Offenders will be held liable for the payment of damages. All rights reserved in case of patent/utility model/trademark protection.

Weitergabe sowie Vervielfältigung dieses Dokuments, Verwertung und Mitteilung seines Inhalts sind nur nach vorheriger ausdrücklicher schriftlicher Zustimmung von SMS Meer GmbH gestattet. Das Dokument ist vor unberechtigtem Zugriff Dritter zu schützen. Zuwiderhandlungen verpflichten zu Schadensersatz. Alle Rechte aus Patent-/Gebrauchsmuster-/Markenschutz vorbehalten.

Diese Zeichnung und alle darauf enthaltenen Informationen sind vertraulich. This drawing and all information on it is confidential.

A1