
DETAILS AT A

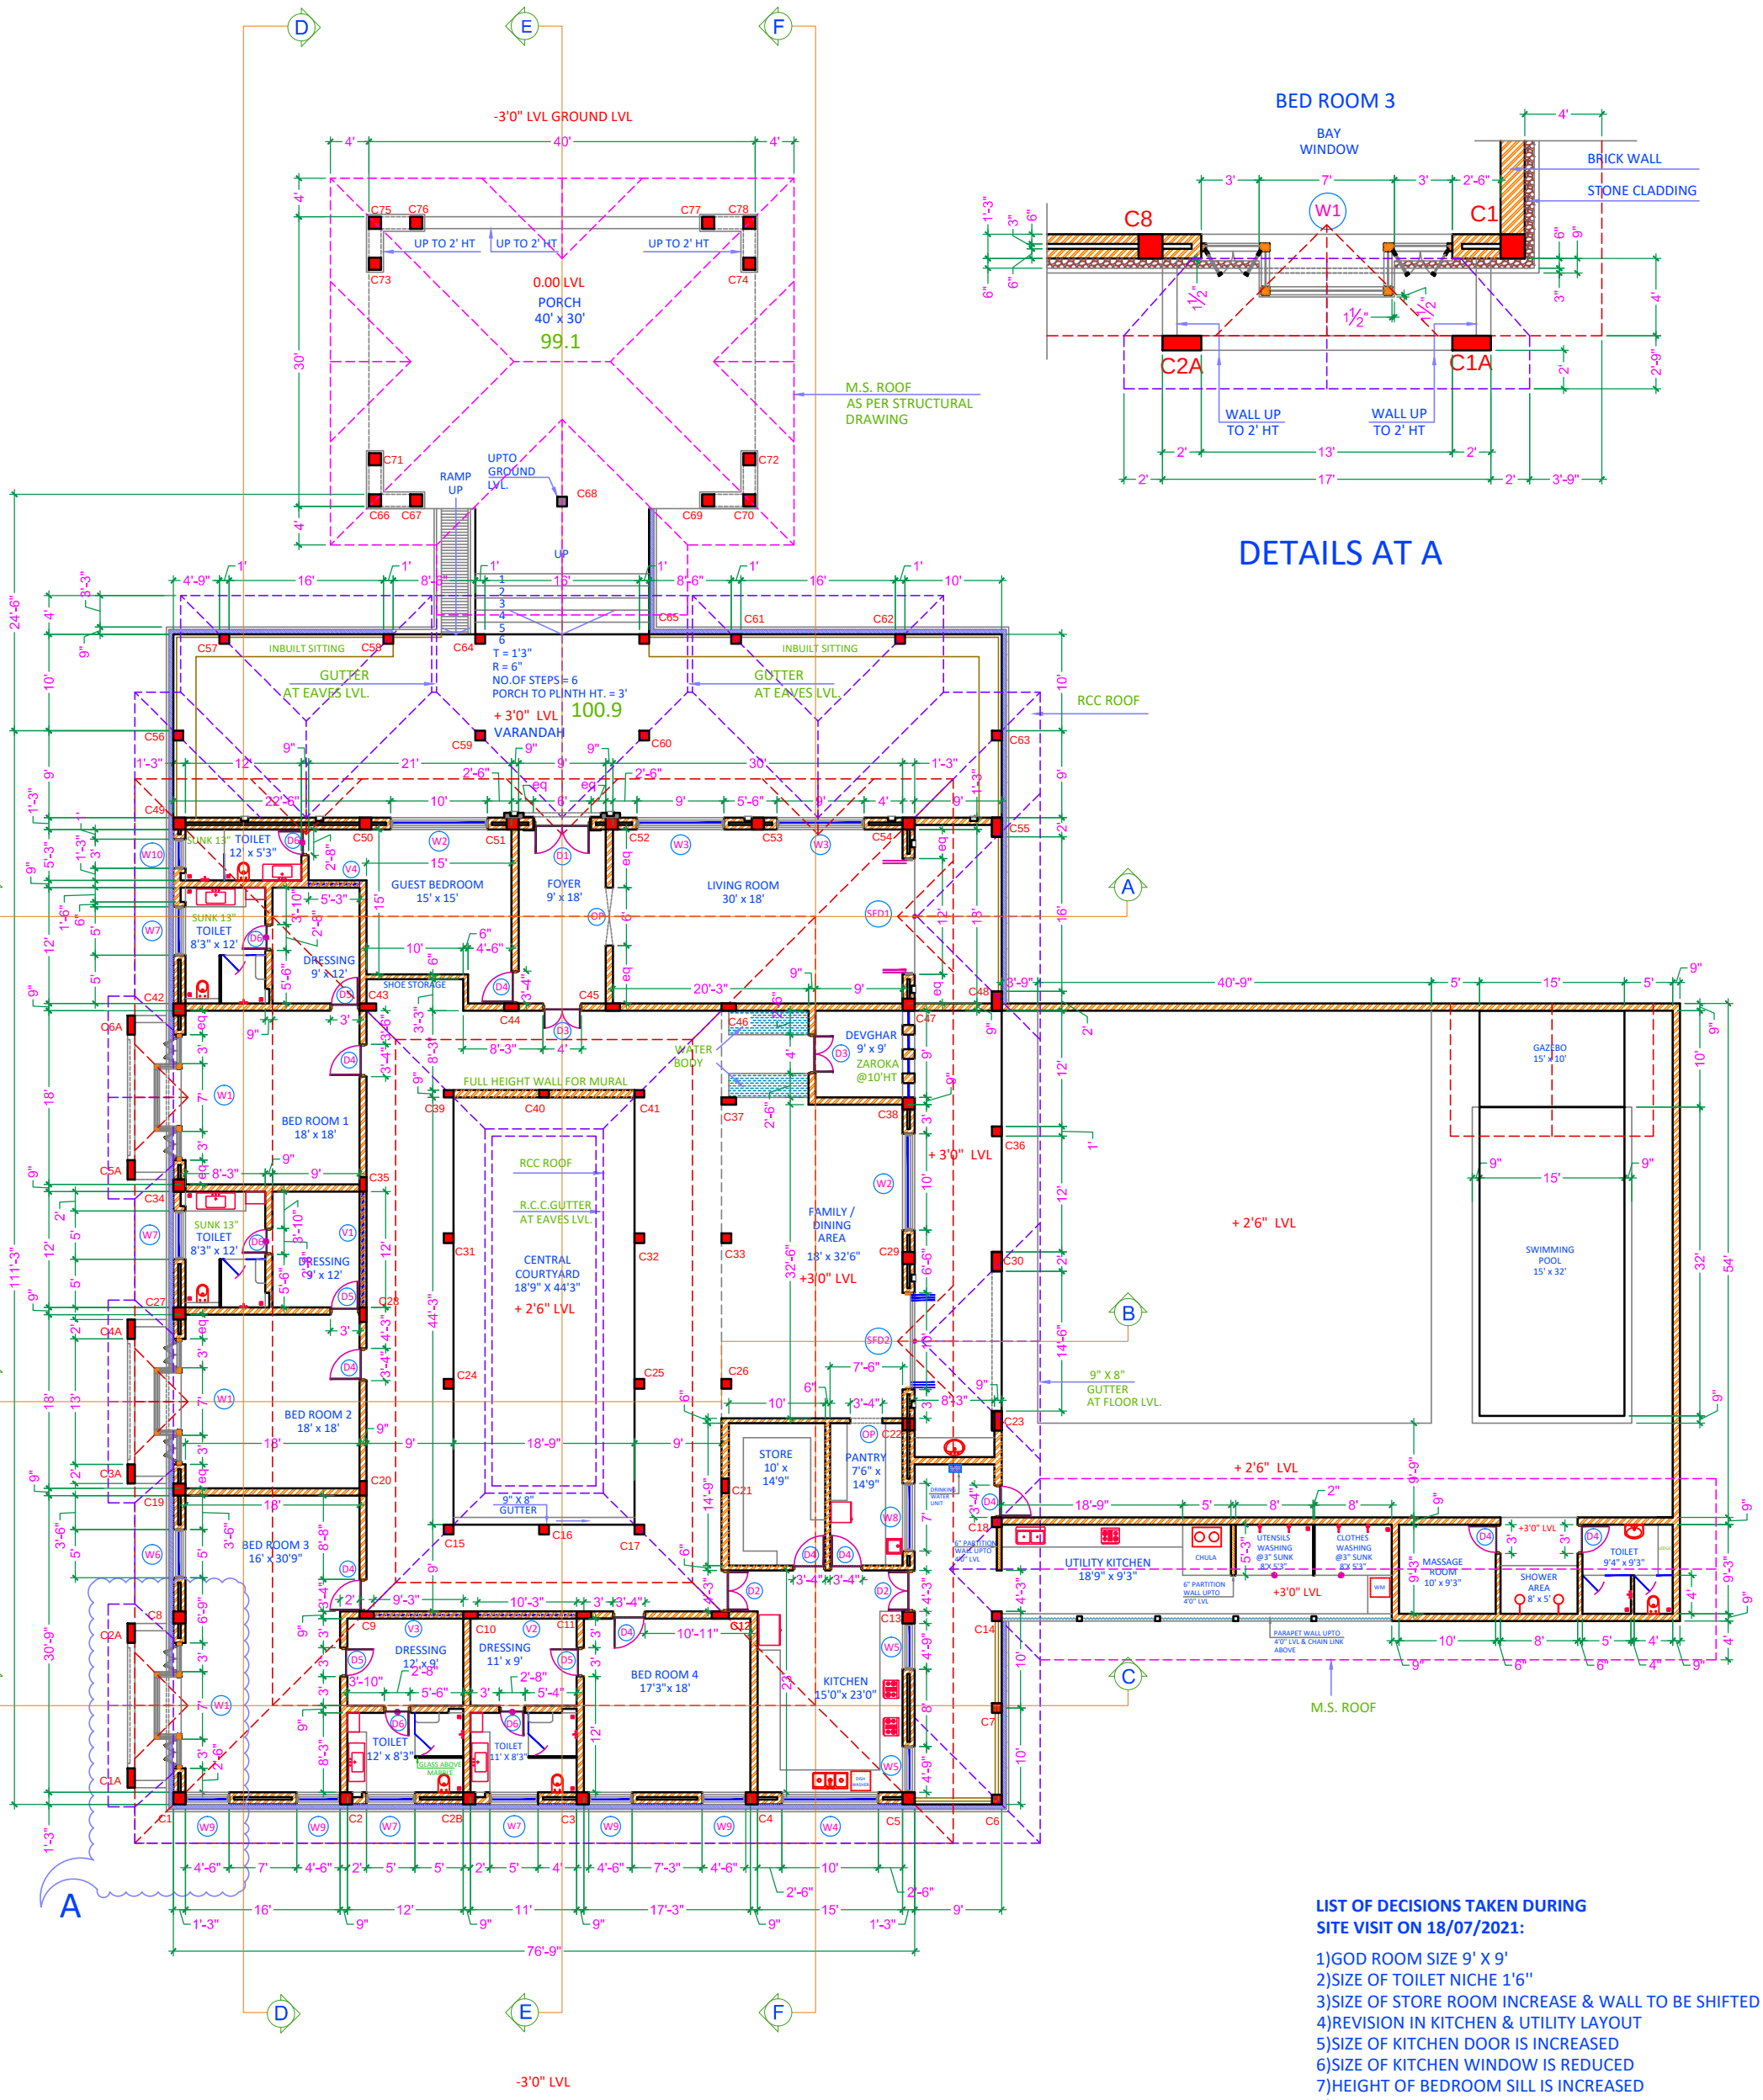

GROUND FLOOR PLAN

LIST OF DECISIONS TAKEN DURING SITE VISIT ON 18/07/2021:

1)GOD ROOM SIZE 9' X 9'
2)SIZE OF TOILET NICHE 1'6''
3)SIZE OF STORE ROOM INCREASE & WALL TO BE SHIFTED
4)REVISION IN KITCHEN & UTILITY LAYOUT
5)SIZE OF KITCHEN DOOR IS INCREASED
6)SIZE OF KITCHEN WINDOW IS REDUCED
7)HEIGHT OF BEDROOM SILL IS INCREASED
8)GUEST ROOM DOOR IS SHIFTED
9)TOILET SLAB CANCELED
10)PLUMBING LINE & OUTLET IN GOD ROOM
11)TOILET WINDOW SILL HEIGHT IS 2'0''
12)CHANGES IN GUEST ROOM TOILET LAYOUT

REV.12 ISSUED TO CLIENT = 2021-07-21
REV.11 ISSUED TO CLIENT = 2021-07-17
REV.10 ISSUED TO CLIENT = 2021-06-24
REV.9 ISSUED TO CLIENT = 2021-05-25
REV.8 ISSUED TO CLIENT = 2021-05-17
REV.7 ISSUED TO CLIENT = 2021-05-14
REV.6 ISSUED TO CLIENT = 2021-05-03
REV.5 ISSUED TO CLIENT = 2021-04-29
REV.5 ISSUED TO CLIENT = 2021-04-27
REV.5 ISSUED TO CLIENT = 2021-03-03
REV.4 ISSUED TO CLIENT = 2020-11-18
REV.3 ISSUED TO CLIENT = 2020-11-06
REV.2 ISSUED TO CLIENT = 2020-11-05
REV.1 ISSUED TO CONT. = 2020-10-30

M/s. Indrajit and Rupa Nageshkar
Architects, Engineers and Urban Designers

RUDRANEIL
R.S. No. 380/E, Rajaram Rifles colony,
Rajarampuri 13th Lane (East),
Kolhapur - 416008. Maharashtra, India.
Tel: +91 231 2520567 Fax: +91 231 2525114
admin@nageshkararchitects.com
www.nageshkararchitects.com

PROPOSED BUNGALOW FOR MR. RAHUL KUL AT RAHU

JOB NO.	REV.12 DATE	DRG. NO.	DRWN BY	CHKD BY
-	2021-07-21	W2	KETAKI	INDRAJIT