
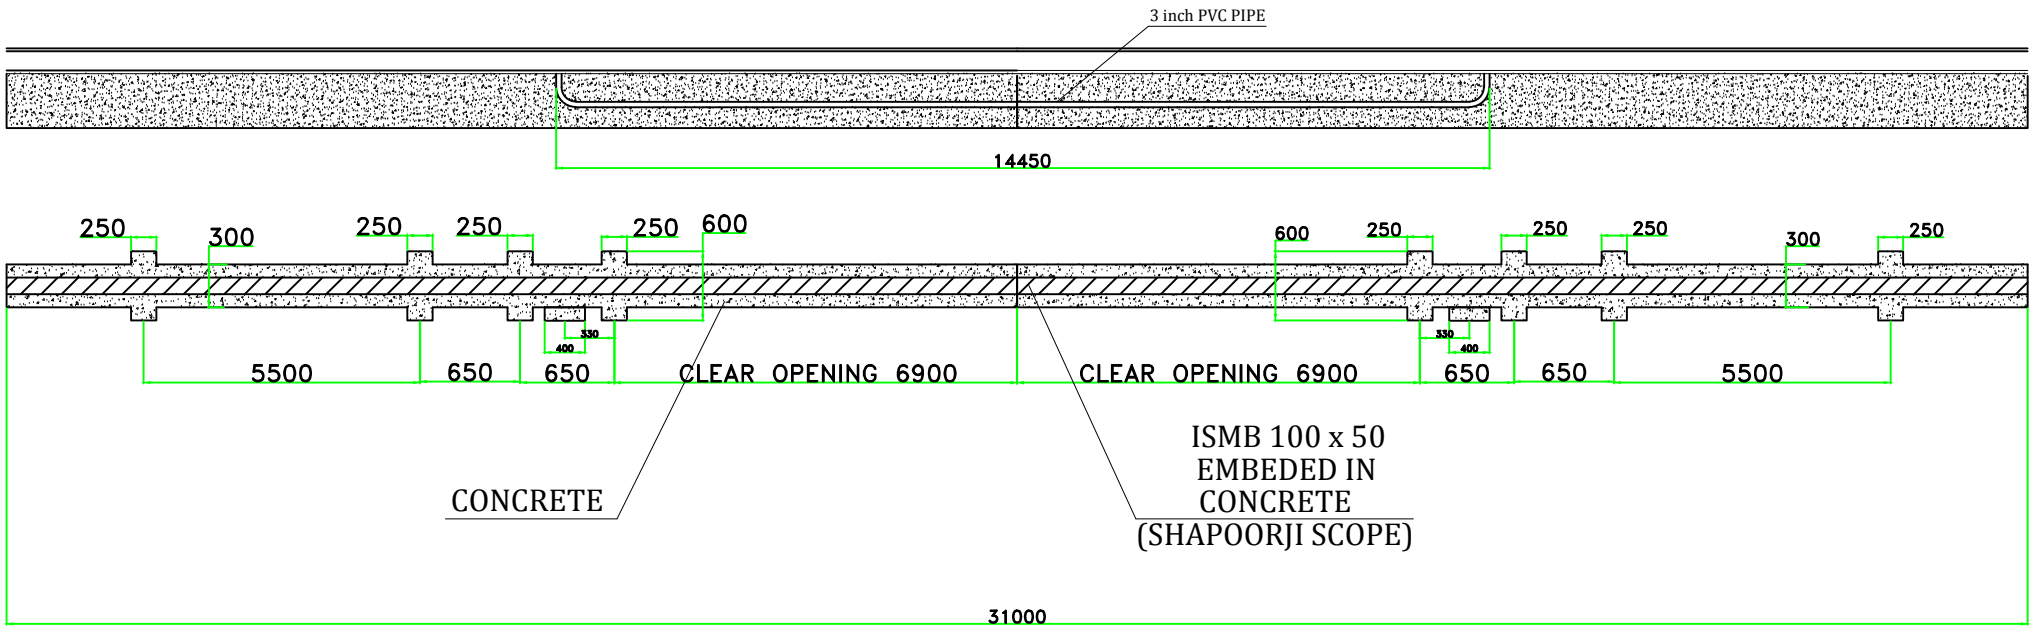


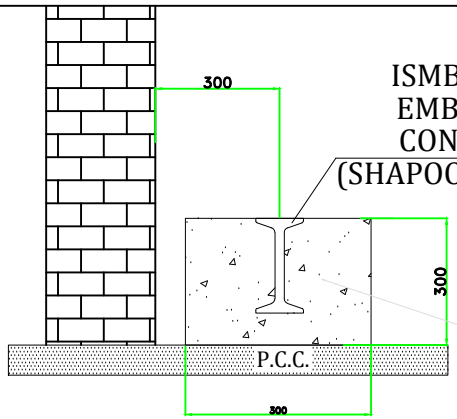

ISMB 100 x 50
EMBEDED IN
CONCRETE
(SHAPOORJI SCOPE)

RCC BEAM
300X300
(SHAPOORJI
SCOPE)

14METER SLIDING GATE FOUNDATION

This drawing & designing is the property of NIHVA TECHNOLOGIES. Not be sold or copy to any other concern.

TITLE

SLIDING GATE
FOUNDATION

CLIENT APPROVAL

ALL DIMENSION ARE IN mm

	SIGN	DATE
DRAWN	ABHIJIT	05/06/15
CHECK	ANIL	05/06/15
REV.	01	
APPRD.		
MFG		
Ref. No.		

NIHVA
NIHVA TECHNOLOGIES PVT. LTD.

NIHVA TECHNOLOGY
PVT. LTD. PUNE
Tel : 020 66304033
Email:- info@nihva.com
Website:- www.nihva.com

CLIENT - SHAPOORJI

PROJECT -ALSTOM

SITE -SANAND, GUJRAT

DWG. NO. - NIHVA/15-16/031

SCALE: 01 | WT: | SHEET: 01 OF 01

If any queries contact : projects@nihva.com