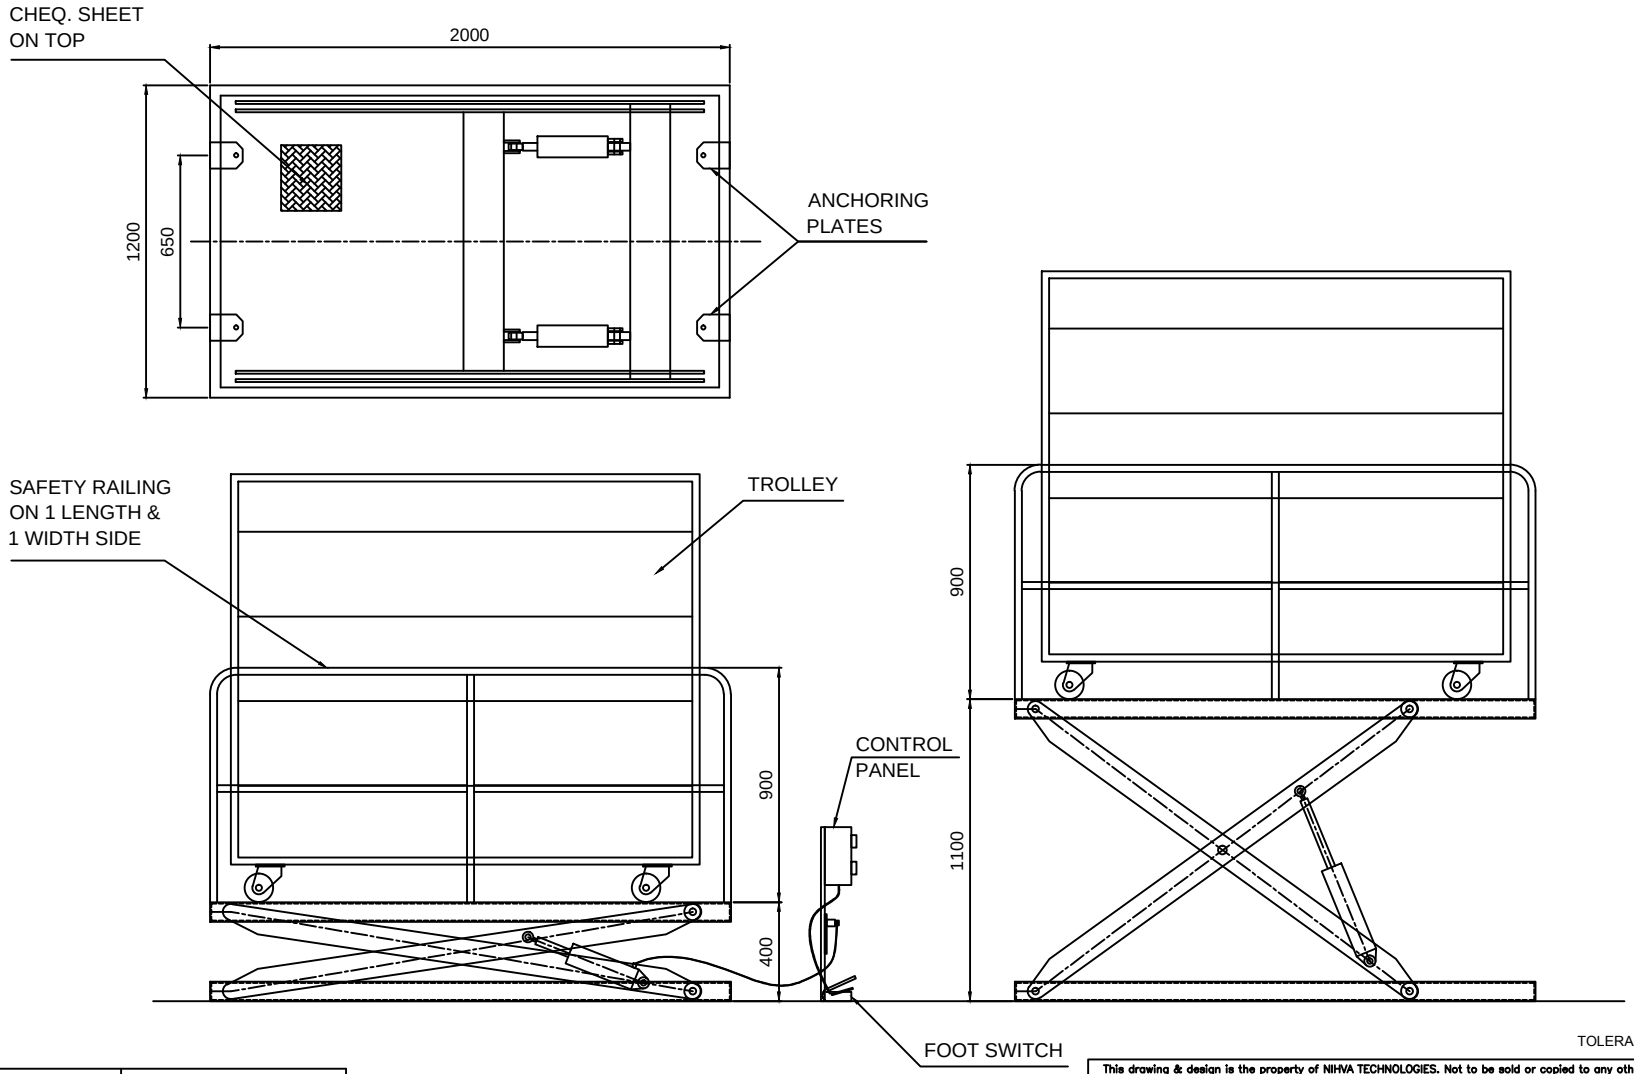


TOLERANCE - ±10mm

SAFETY RAILING	900 MM HEIGHT
LIFT HT	700 MM
MAX HT	1100 MM
SHUT HT	400 MM
PLATFORM SIZE	2000L X 1200W
CAPACITY	250 KGS

NOTE :
1. INPUT SUPPLY VOLTAGE & PNEUMATIC CONNECTION TO SOLENOID MANIFOLD WILL BE IN CLIENT SCOPE.
2. IF REQ. CIVIL WORK WILL BE IN CLIENT SCOPE.

This drawing & design is the property of NIHVA TECHNOLOGIES. Not to be sold or copied to any other concern.

TITLE
FLOOR MOUNTED PNEUMATIC SCISSOR LIFT

	NAME	SIGN	DATE
DRAWN	P.V.A		01.10.2019
CHECK	G.J		01.10.2019
APPRD.			

NIHVA TECHNOLOGIES PVT. LTD.
NIHVA TECHNOLOGIES PVT. LTD. PUNE
Tel : 020 66304033
Email:- info@nihva.com
Website:- www.nihva.com

CLIENT - L.G
PROJECT -
SITE LOCATION - RANJANGAON
If any queries contact : design@nihva.com
DWG. NO. : NIHVA/19-20/0110
REV- 0
ALL DIMENSION ARE IN mm
SCALE: NTS
WT:
SHEET: 01 OF 01