

SCISSOR LIFT SIZE	WIDTH (W)	LENGTH (L)	HEIGHT (H)	LIP (C) LENGTH
	2000	2000	800	300


PIT DIMENSION	WIDTH (W 1)	LENGTH (L 1)	DEPTH (D)	ALL DIMENSIONS ARE IN mm
	2150	2150	805	

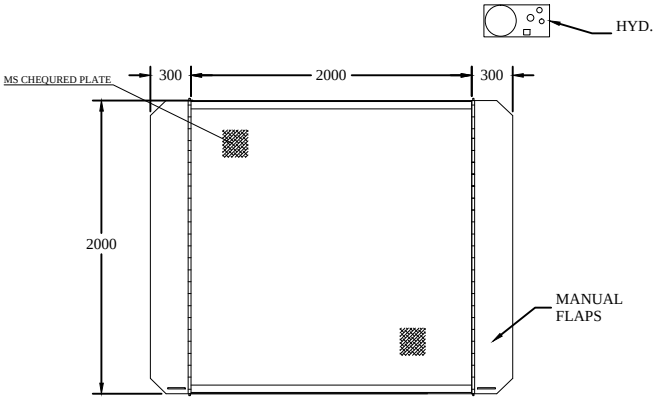

PLAN

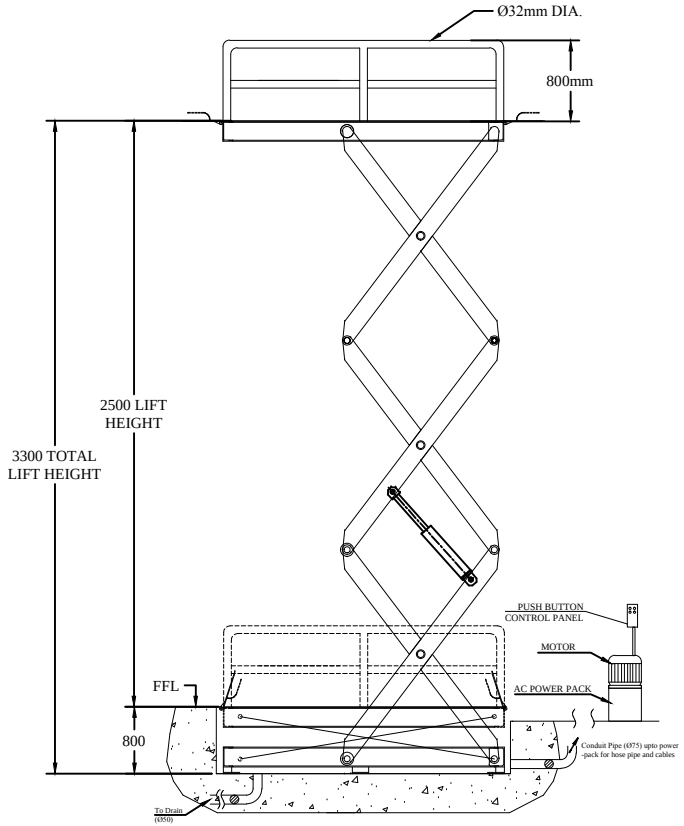

ELEVATION

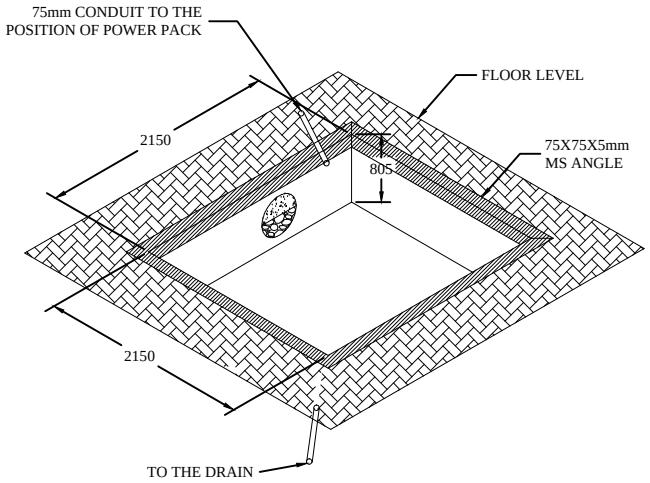

PIT DRAWING

REVISION 1- LIFT HEIGHT REVISED FROM 1800 TO 2500mm.
REVISION 2- PLATFORM SIZE REVISED FROM 2X3m TO 2X2m.

This drawing & designing is the property of NIHVA TECHNOLOGIES. Not be sold or copy to any other concern.

TITLE: SCISSOR LIFT

NIHVA TECHNOLOGIES PVT. LTD.
NIHVA TECHNOLOGY PVT. LTD. PUNE
Tel : 020 66304033
Email:- info@nihva.com
Website:- www.nihva.com

	SIGN	DATE
DRAWN	OMKAR	04/10/17
CHECK	SHEKHAR	04/10/17
REV.	0	
APPROVAL	SHEKHAR	04/10/17

CLIENT - SHILCHER TECHNOLOGIES LTD.
PROJECT -
SITE - VADODARA, GUJRAT
DWG. NO. : NIHVA/17-18/0198/R02
If any queries contact : projects@nihva.com
SCALE: NTS | WT: | SHEET: 01 OF 01
ALL DIMENSION ARE IN mm

SCISSOR LIFT- 5000 KG CAPACITY