

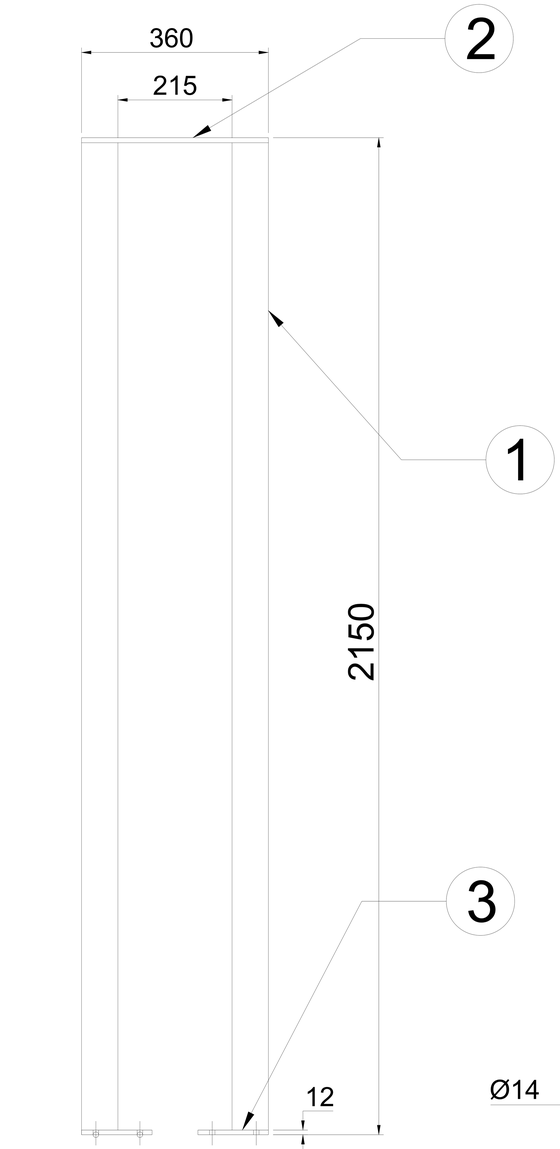


POST

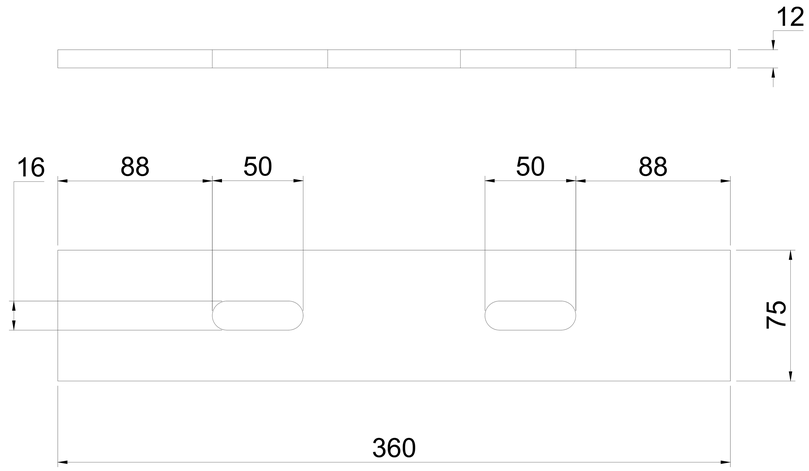

2 TOP PLATE

SR.NO	DESCRIPTION	SPECIFICATION	QTY	WEIGHT
5	NYLON WHEEL	Ø50 X 75L WITH M14 STUD	8 NOS	
4	ANCHOR BOLT	M12 X 150L	32 NOS	
3	PROFILE	140 X 12 X 200L	8 NOS	
2	PROFILE	75 X 12 X 360L	4 NOS	
1	SQ. TUBE	72 X 72 X 3.2 THK X 2125L	8 NOS	

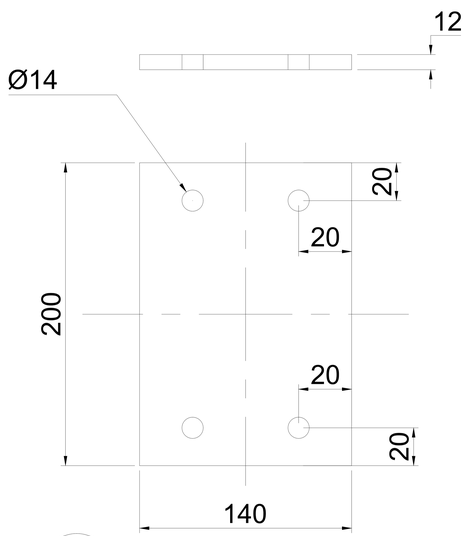

3 BASE PLATE

This drawing & designing is the property of NIHVA TECHNOLOGIES. Not to be sold or copied to any other concern.

TITLE	SLIDING GATE POST DRAWING			NIHVA TECHNOLOGIES PVT. LTD.	NIHVA TECHNOLOGIES PVT. LTD. PUNE
	NAME	SIGN	DATE	Website:- www.nihva.com	Tel : 020 66304033
DRAWN	P.V.A		26.07.19	CLIENT -	Email:- info@nihva.com
CHECK	V.M.T		26.07.19	PROJECT -	
APPROVAL				SITE LOCATION -	
If any queries contact : design@nihva.com				DWG. NO. : NIHVA/19-20/VDR/116	REV.:- 0
ALL DIMENSION ARE IN mm				SCALE: NTS	WT: SHEET: 01 OF 01