

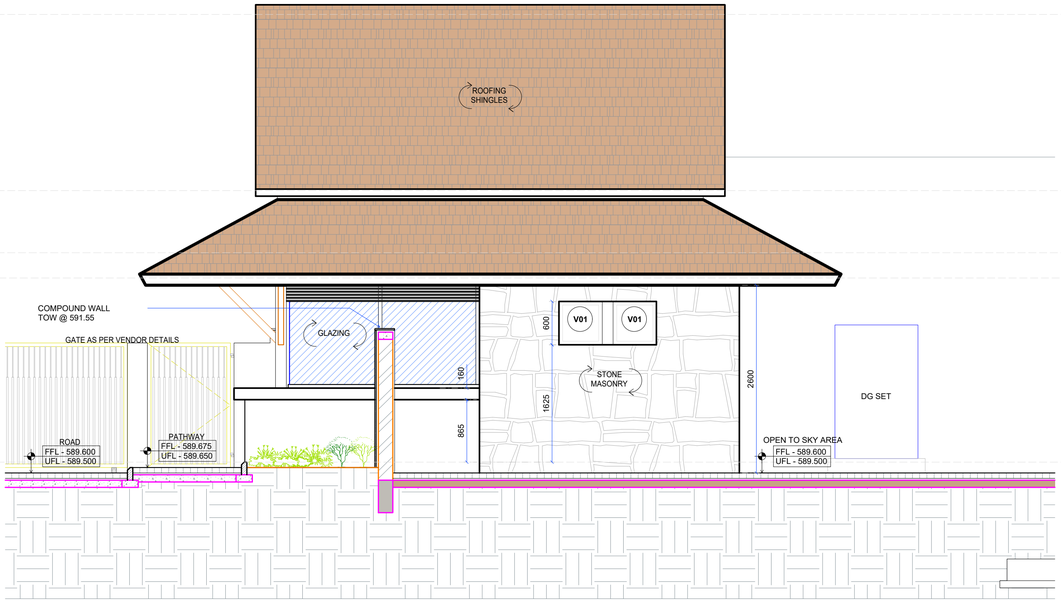



ELEVATION A
(SCALE - 1:40)

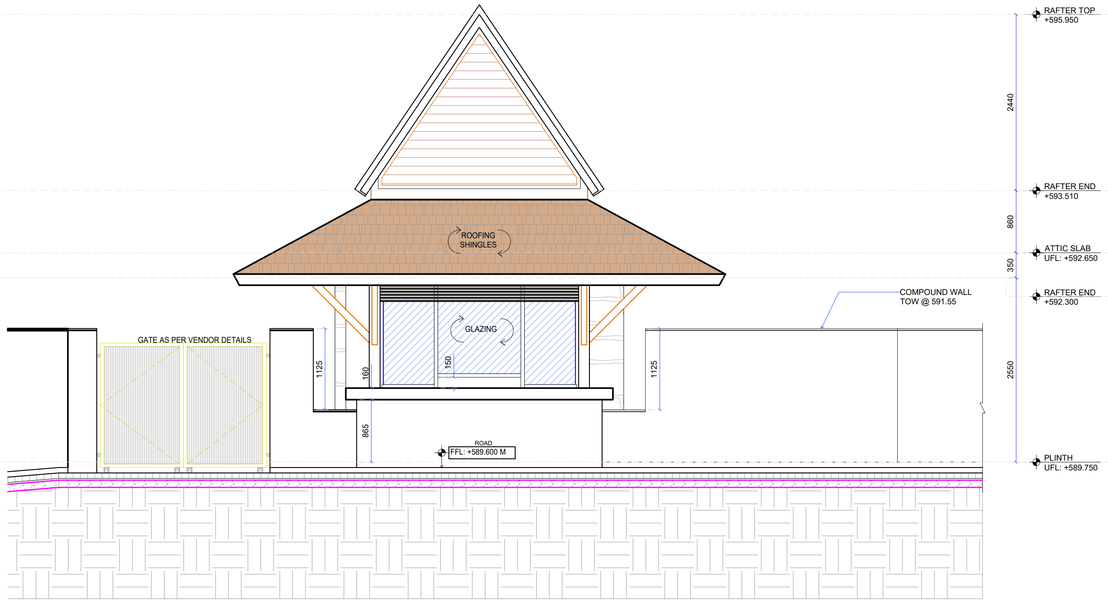

ELEVATION B
(SCALE - 1:40)

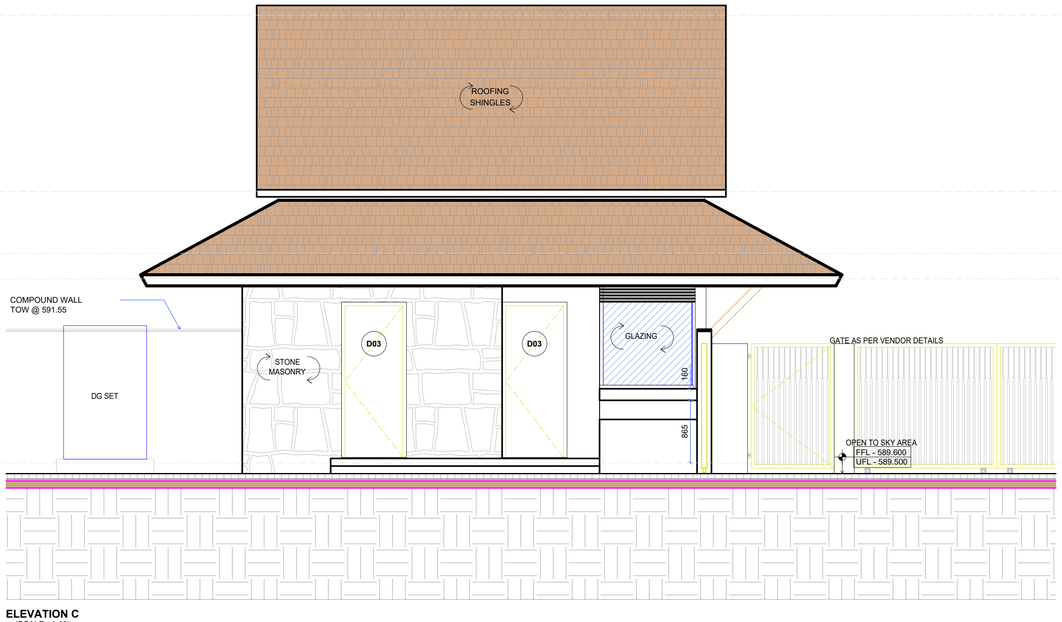

ELEVATION C
(SCALE - 1:40)

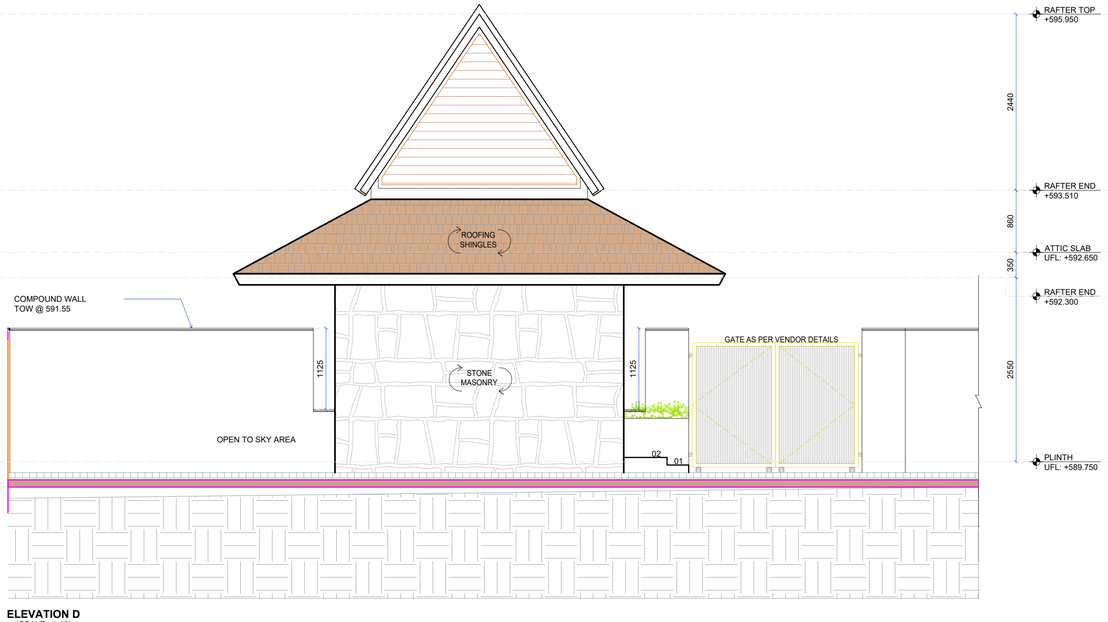

ELEVATION D
(SCALE - 1:40)

Panchshil
PANCHSHIL REALTY
Pune: Tech Park One, Tower "E", 191 Yerwada, Pune 411 006

ISSUES

SITE	RCC	LANDSCAPE	INTERIOR	SERVICES	

REVISIONS

REV. NO.	DATE	DESCRIPTION	DRN BY	CHKD BY
R0	23/05/25	ISSUED FOR CONSTRUCTION	SV	PD

DRAWING NOTES

1. REFER SHOP DRAWINGS FOR ALL ROOFING DETAILS
2. REFER SHOP DRAWINGS FOR ALL GLAZING DETAILS
3. REFER MEP DRAWINGS FOR ALL SERVICES

GOOD FOR CONSTRUCTION

NOTES

1. ONLY WRITTEN DIMENSIONS TO BE FOLLOWED.
2. ALL DIMENSIONS ARE IN MILLIMETERS AND LEVELS IN METERS UNLESS OTHERWISE SPECIFIED.
3. ALL LEVELS/ DIMENSIONS ARE FROM UNFINISHED ARCHITECTURAL SURFACES.
4. FOR STRUCTURAL, SERVICES, LANDSCAPE & INTERIOR DETAILS REFER RELEVANT CONSULTANTS DRAWINGS.
5. DISCREPANCIES IF ANY TO BE BROUGHT TO THE NOTICE OF THE ARCHITECTS BEFORE EXECUTION.

DATE : 23-05-25
DEALT : PD
DRAWN BY : SV
SCALE : 1 : 40

PROJECT :
BOUGAIN VILLA, LOHEGAON, PUNE

DRAWING TITLE :
UTILITY SPACE 01 - SECURITY CABIN 1 ELEVATIONS

JOB NO. PAN - 2332
DRAWING NO. 2332_B-2.3
REVISION NO. R0