
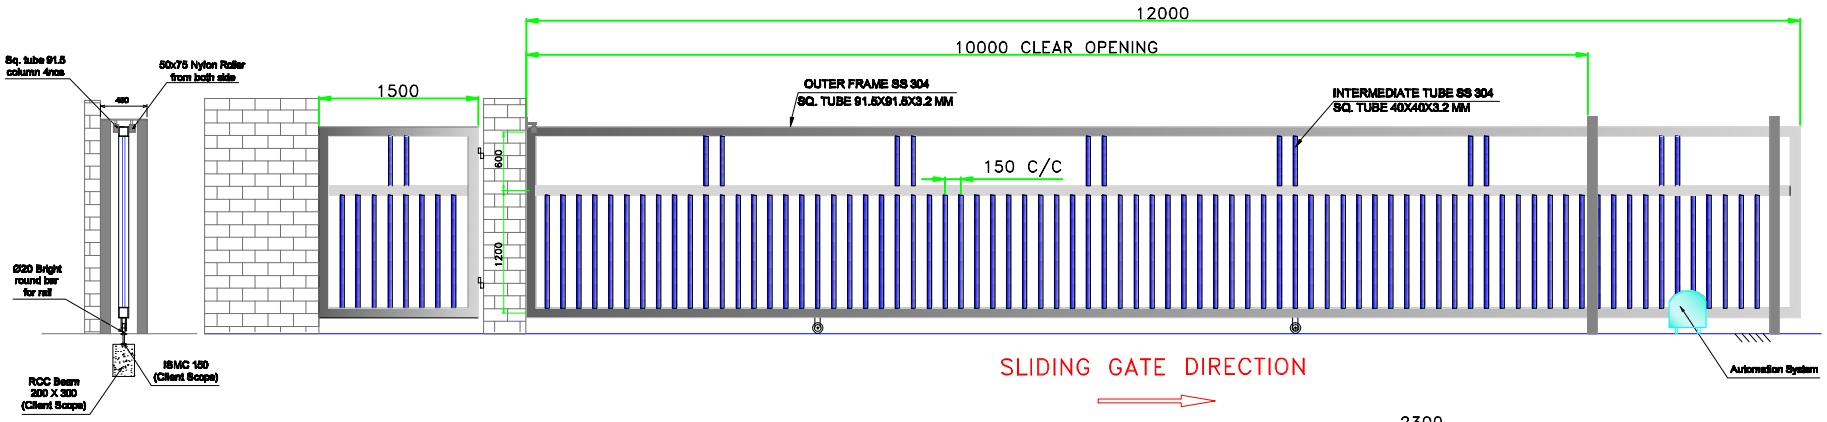


SLIDING GATE DIRECTION

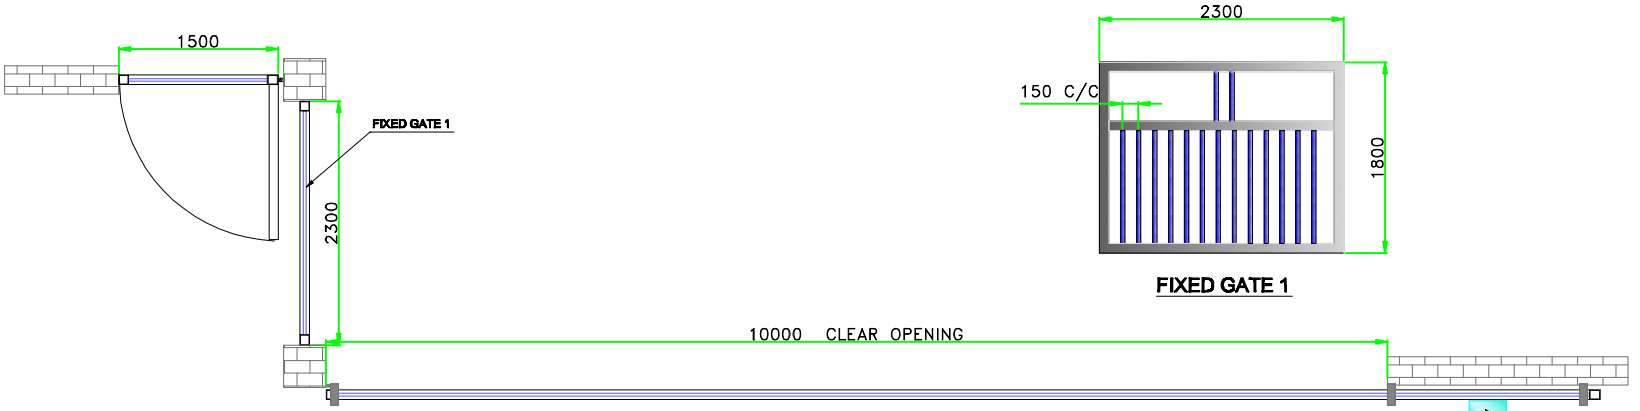

TOP VIEW

FIXED GATE 1

SLIDING GATE SIZE = 12000 (W) X 1800 (H), QTY = 1NOS..
CLEAR OPENING = 10,000 (W) X 1800 (H)
WICKET GATE SIZE = 1500(W) X 1800 (H), QTY = 1NOS.
FIXED GATE SIZE = 2300(W) X 1800(H), QTY = 1NOS.
OUTER FRAME = 91.5 X 91.5 X 3.2 mm
INNER FRAME = 40 X 40 X 2 mm
GAP B/W FRAME = 150 c/c
MATERIAL = SS 304
C' COLUMN VERTICAL SUPPORT = 4 NOS.

This drawing & designing is the property of NIHVA TECHNOLOGIES. Not be sold or copy to any other concern.

TITLE: SLIDING GATE	ALL DIMENSION ARE IN mm			NIHVA TECHNOLOGIES PVT. LTD.
		SIGN	DATE	
	DRAWN	ABHIJIT	05/11/14	CLIENT - JSW
CLIENT APPROVAL	CHECK	ANIL	05/11/14	PROJECT -
	REV.	02		SITE - KHED
	APPRD.			DWG. NO. - NVA/JSW/D1/1 of 3
	MFG			SCALE: 01 / WT: / SHEET: 0101
	Ref. No.			If any queries contact : projects@nihva.com

NIHVA TECHNOLOGY PVT. LTD. PUNE
Tel : 020 66304033
Email:- info@nihva.com
Website:- www.nihva.com