
LEGEND - GRADE : 310 N /MM2

NOTE - MAXIMUM WELD SIZE AS PER TABLE GIVEN BELOW


SYMBOL	LEGEND	WEIGHT	MAX. WELD SIZE
Ⓐ	R.H.S.122x61x4.5 mm thk	11.88	5
Ⓑ	R.H.S.122x61x4.5 mm thk	11.88	5
Ⓒ	S.H.S. 40x40x4mm thk	4.20	4
PURLIN	R.H.S. 145 x82x3.2 mm thk	17.74	5
TIE RUNNER	R.H.S.122x61x4.5 mm thk	11.88	5
TYP BRACING	2 ⊣ 65X65X6		6

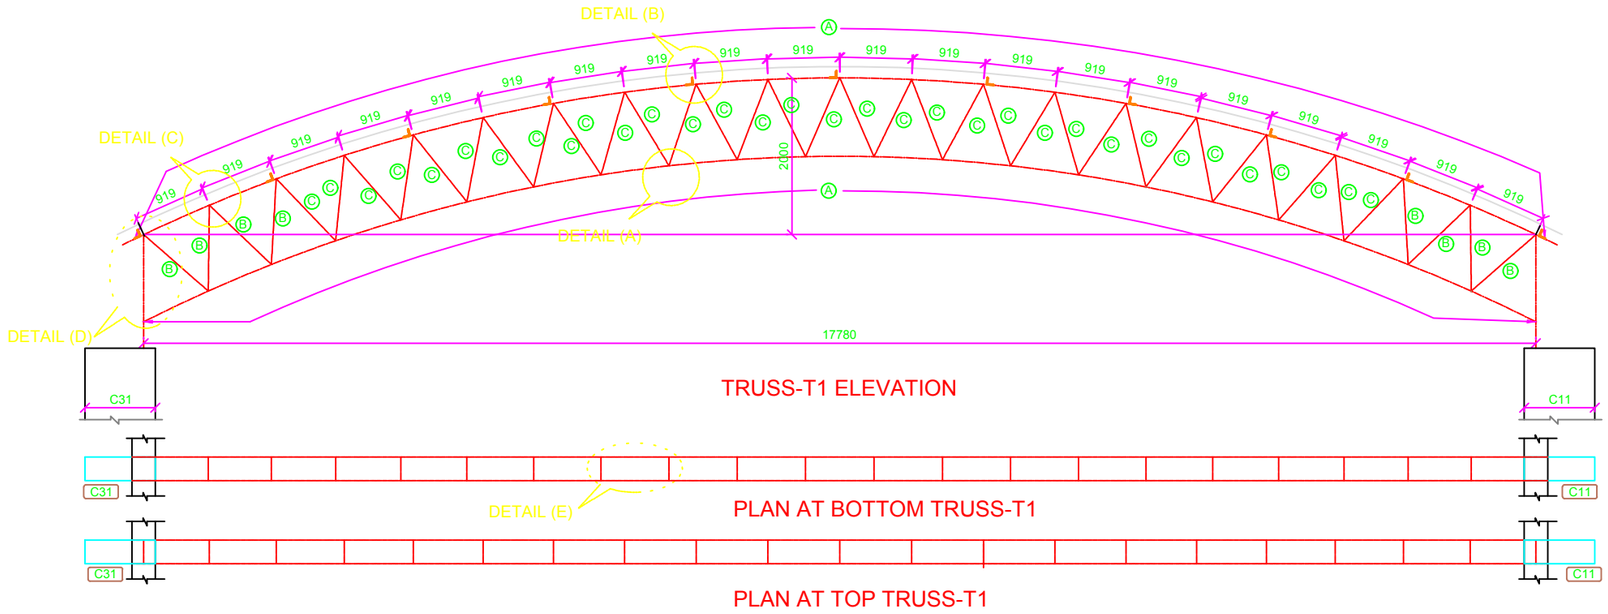


TRUSS-T1 ELEVATION

PLAN AT BOTTOM TRUSS-T1


PLAN AT TOP TRUSS-T1

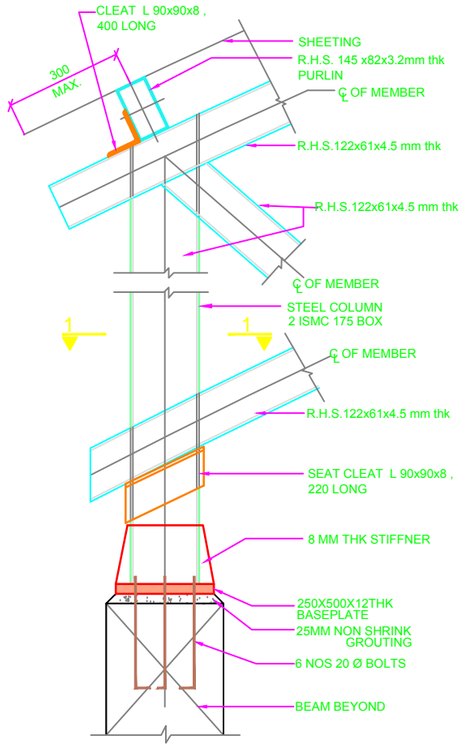


DETAILS AT D

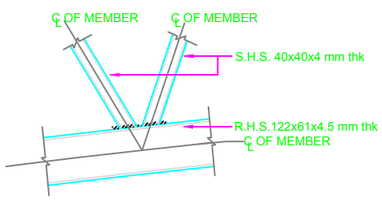

DETAILS AT A

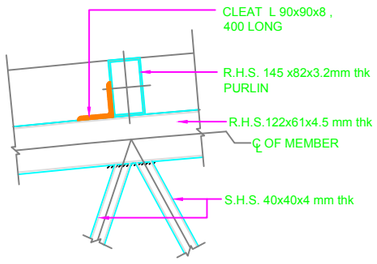


DETAILS AT B

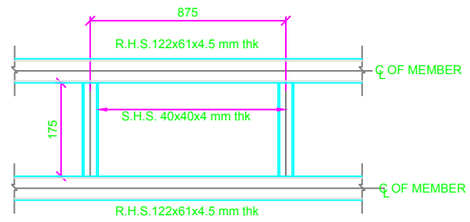


DETAILS AT 'E'

SECTION 1..1

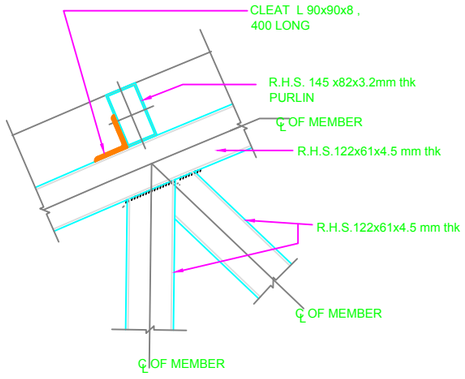

DETAILS AT C

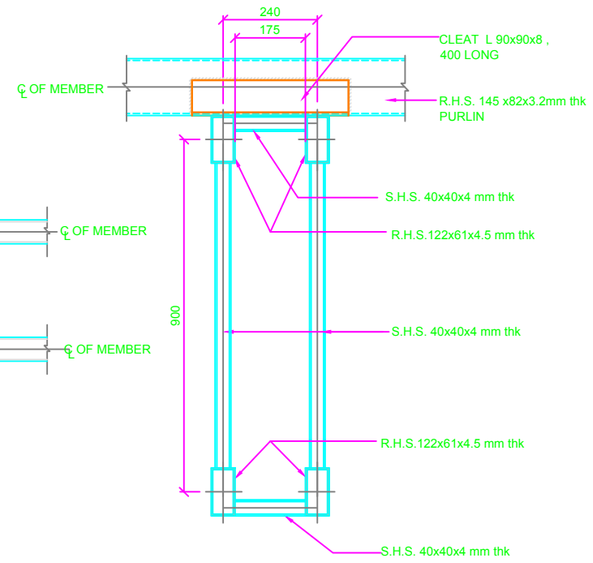

SECTION OF TRUSS-T1

R5	DESIGN		DATE		
R4	DESIGN		DATE		
R3	DESIGN		DATE		
R2	DESIGN		DATE		
R1	DESIGN		DATE		
R0	DESIGN	ORIGINAL ISSUE	DATE	00/00/2023	
			DRAWN BY		
REV NO		REVISION DETAILS			

DRAWING	TRUSS ELEVATION
PROJECT	PROP. CONSTRUCTION OF SCHOOL BLDG AT VIMANNAGAR PUNE FOR SYMBIOSIS.
ARCHITECT	PANASE ASSOCIATE
CLIENT	SYMBIOSIS.

SATISH MARATHE
CONSULTING ENGINEERS
GHAGARE RESIDENCY, 105A/30, INCOME TAX LANE, PUNE - 411 004.
WEB: satishmarathe.com EMAIL : smce.civil@gmail.com
Ph. (020) - 25441396, 25445477, 29910754.

DESIGNED BY	ANGADI	DATE	AUG-2023
DRAWN BY	SAWANT	SHEET NO	S1-A
CHECKED BY	___	JOB NO	4573
SCALE	NTS		

NOT FOR CONSTRUCTION