
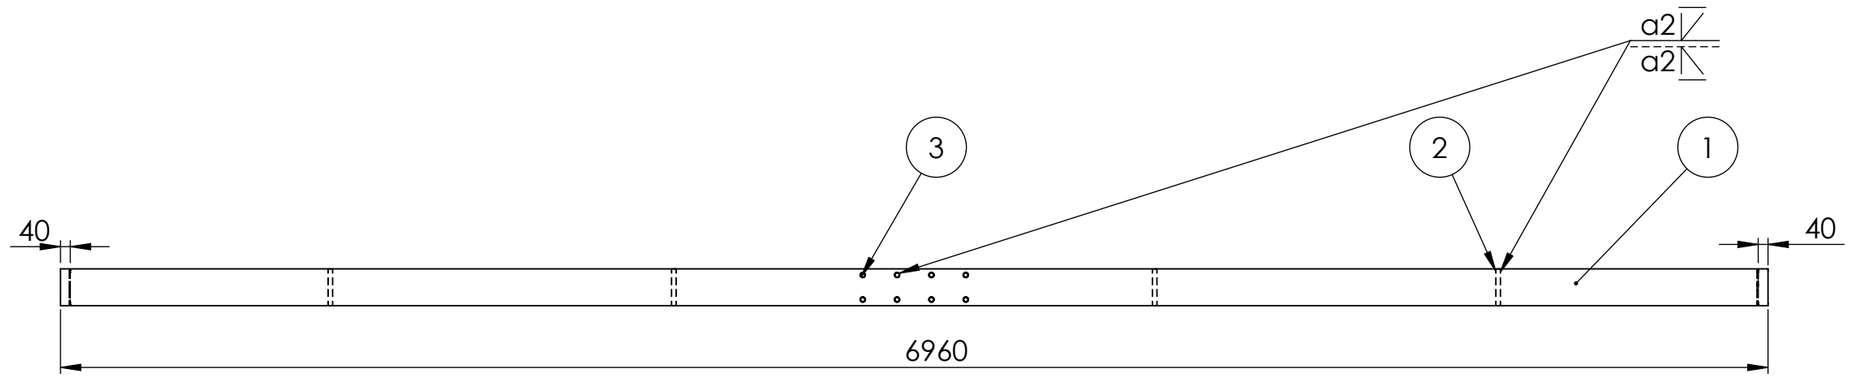


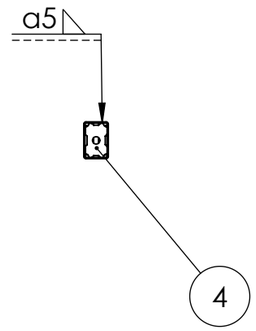

NR	NAZWA	NR RYSUNKU	MATERIAL	NR KATALOGOWY	ILOSC
4	przeslo - plyta A	P.1.2	1.0045 (S355JR)		2
3	przeslo - tuleja A	P.1.3	1.0045 (S355JR)		8
2	przeslo - tuleja B	P.1.4	1.0045 (S355JR)		4
1	przeslo - profil A	P.1.1	1.0045 (S355JR)		1

PROJEKT:

NAZWA ELEMENTU: przeslo - spawane

NR KATALOGOWY:

KATEGORIA: przeslo

TYP ELEMENTU: zlozenie

ETAP PRODUKCJI: spawanie

NORMA:

MATERIAL:

MASA: 124.80 kg

ROZMIAR ARKUSZA: A3

PODZIALKA: 1:25

NUMER RYSUNKU: P.1

DATA/WERSJA: 24.04.2025

© 2018-2025 Copyright
JP NOVATION Sp. z o.o.
All rights reserved.

Wymiary nietolerowane wykonac w klasie dokladnosci
"m" wg. normy ISO 2768-1