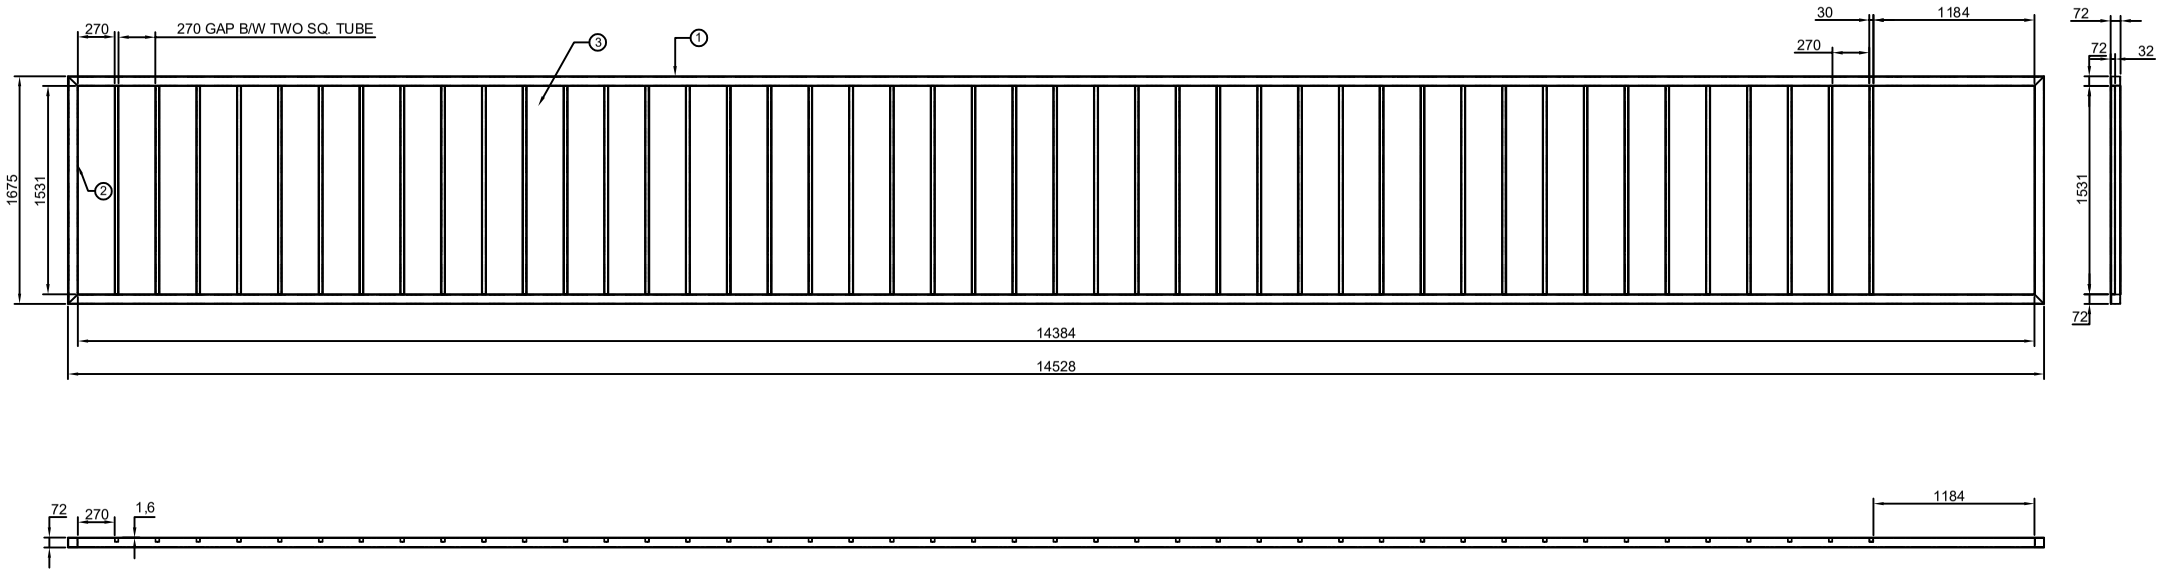


Note:-

1.All Dimension are in MM

2.Kindly Mentain the given Dimensions

BOM				
SL NO.	DESCRIPTION	SPECIFICATION	QTY	WEIGHT
1	MS SQ. TUBE	72X72X3.2X14528L	2NOS	203.39
2	MS SQ. TUBE	72X72X3.2X1675L	2NOS	23.45
3	MS SQ. TUBE	30X30X2.6X1531L	44NOS	151.42

This drawing & design is the property of NIHVA TECHNOLOGIES. Not to be sold or copied to any other concern.

TITLE:- Sliding Leaf

NIHVA TECHNOLOGIES PVT. LTD.
NIHVA TECHNOLOGIES PVT. LTD. PUNE
Tel : 020 66304033
Email:- info@nihva.com
Website:- www.nihva.com

	NAME	DATE	SIGN
DRAWN	NIRMALA K	24/01/2023	
CHECK			
APPRD.	AMIT.K	24/01/2023	

If any queries contact : design1@nihva.com

ALL DIMENSION ARE IN mm

CLIENT - POONAM ROLLER FLOUR MILL PVT LTD

LOCATION -

PRODUCT - SLIDING GATE | QTY- 1

DWG NO:- NIHVA/22-23/MFG /0105 | REV-00

SCALE: NTS | SCALE:-- 1:1 | SHEET: 01 OF 01

Rev No.	Revision	Date	Revised By
1	GAP B/W TWO TUBES CHANGED FOR TRAY MTG	01.02.2023	NIRMALA K