

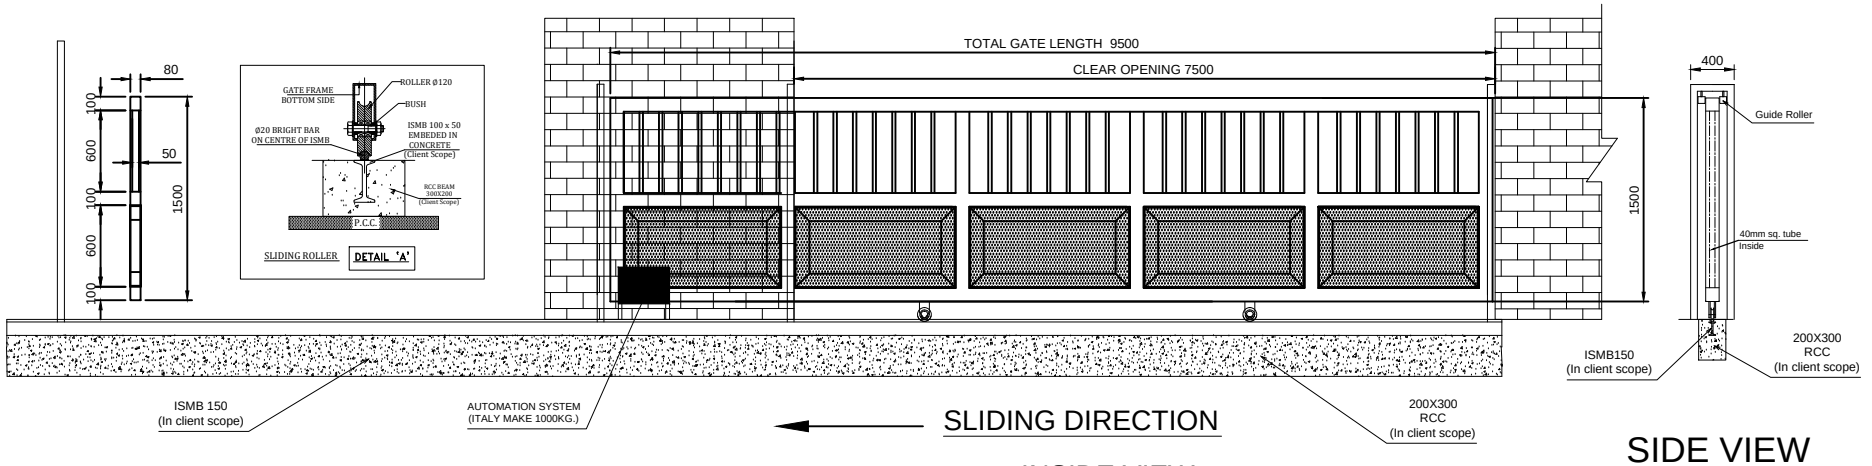


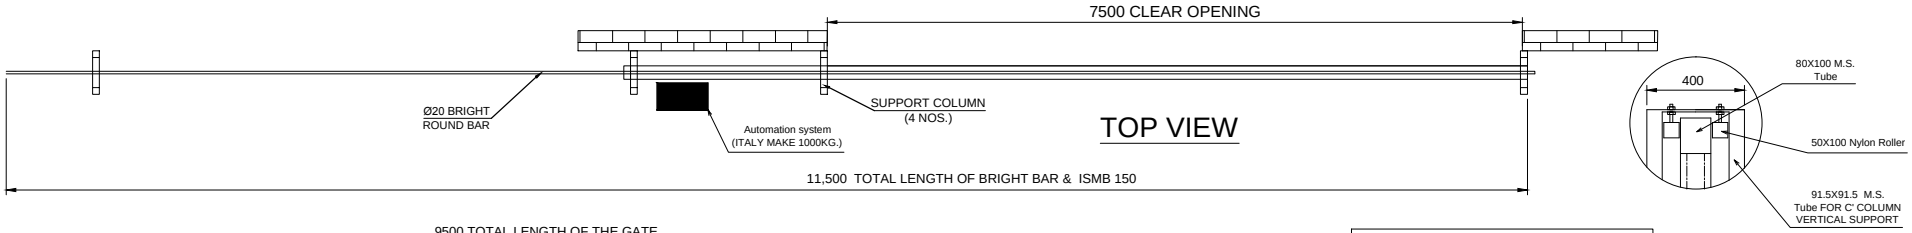

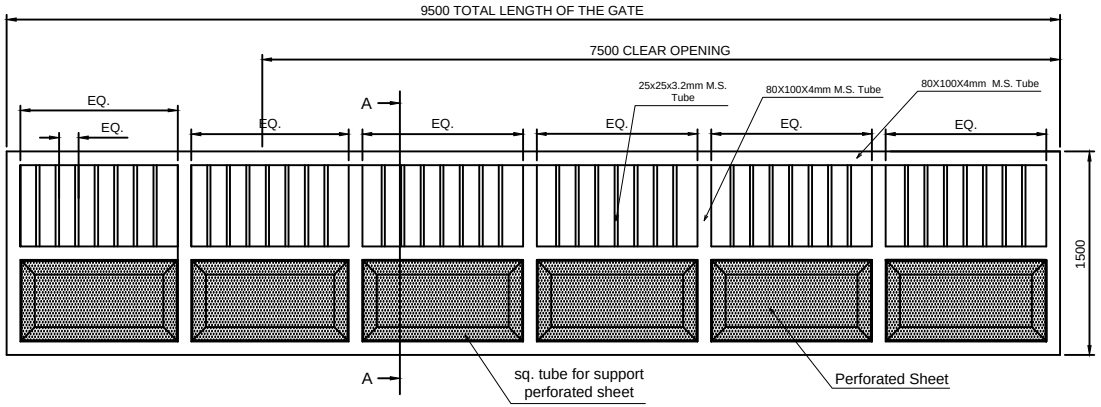

Clear Opening size - 7500X1500mm
Total length of gate - 9500X1500mm
No. Of Column - 4 nos.
Factory paint finish - Red oxide primer coat
NOTE :- *ALL REQ. CIVIL WORK WILL BE IN CLIENT SCOPE.

This drawing & designing is the property of NIHVA TECHNOLOGIES. Not be sold or copy to any other concern.

TITLE	MOTORIZED SLIDING GATE		NIHVA TECHNOLOGIES PVT. LTD.
	SIGN	DATE	
DRAWN	ABHIJIT	16/10/15	CLIENT - REWARD CONSTRUCTION
CHECK	ANIL	16/10/15	PROJECT - GIVAUDAN
REV.	02		SITE - RANJANGAON MIDC
APPROVAL			DWG. NO. : NIHVA/15-16/106
If any queries contact : projects@nihva.com			SCALE: 01 / WT: / SHEET: 01 OF 01
ALL DIMENSION ARE IN mm			

NIHVA TECHNOLOGY PVT. LTD. PUNE
Tel : 020 66304033
Email:- info@nihva.com
Website:- www.nihva.com