
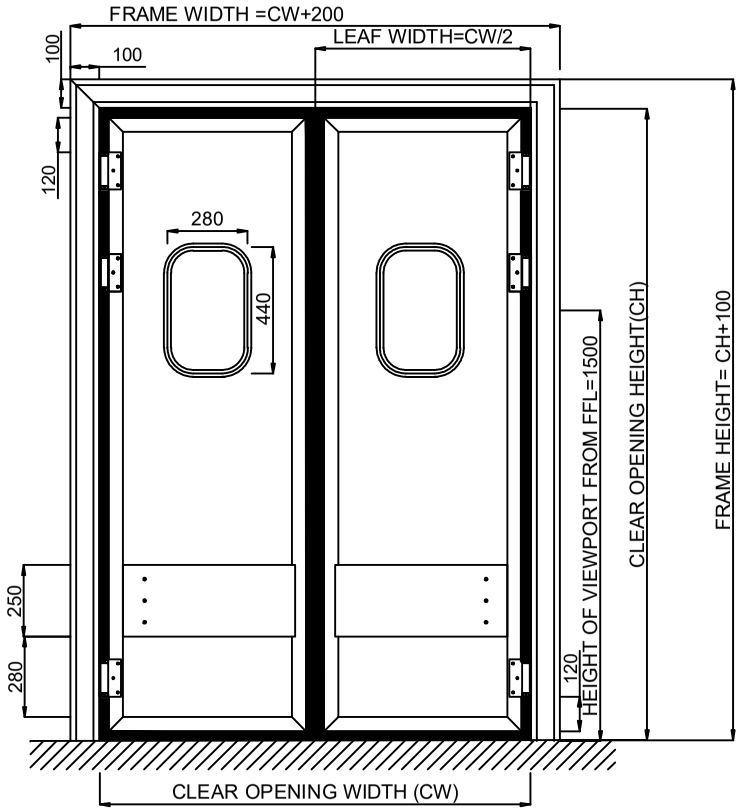


SL NO	CW	CH	QTY
1	1830	2390	2NOS
2	1837.5	2395	2NOS
3	1832.5	2380	2NOS

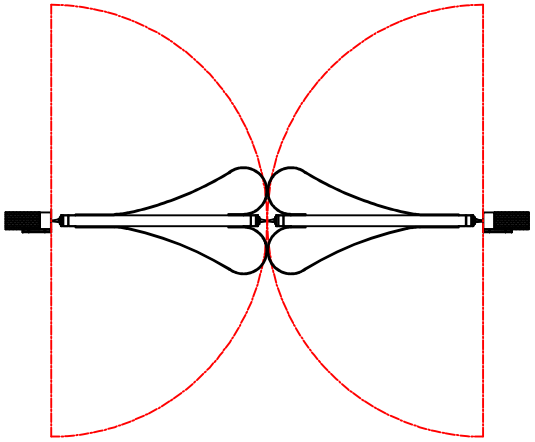

Note:
1.All dimension are in mm
2.All Civil work will be in client scope

LEAF FINISH : PE / PCGI
LEAF THICKNESS : 40 MM
HINGES MOC : DOUBLE ACTION STAINLESS STEEL
VIEW WINDOW : 1 UNIT ON EACH LEAF
VIEW WINDOW HEIGHT : 440 MM
VIEW WINDOW WIDTH : 280 MM
VIEW WINDOW POSITION FROM FFL : 1500 MM

This drawing & design is the property of NIHVA TECHNOLOGIES. Not to be sold or copied to any other concern.

TITLE:- NIHVA Make NFF3 Flip Flap Door

NIHVA TECHNOLOGIES PVT. LTD.
NIHVA TECHNOLOGIES PVT. PUNE
Tel : 020 66304033
Email:- info@nihva.com
Website:- www.nihva.com

	NAME	DATE	SIGN
DRAWN	SUJATA	22-03-2022	
CHECK	G.P	22-03-2022	
APPRD.	P.J	22-03-2022	

CLIENT - RBCC
LOCATION - PUNE
PRODUCT - FLIP FLAP DOOR
If any queries contact : design@nihva.com
DWG NO:-NIHVA/21-22/CLT/0372 REV- 01
ALL DIMENSION ARE IN mm
SCALE: NTS SCALE:-- 1:1 SHEET: 01 OF 01

Rev No.	Revision	Date	Revised By
1	Clear opening and clear height of the door has been changed	24/03/2022	Sujata