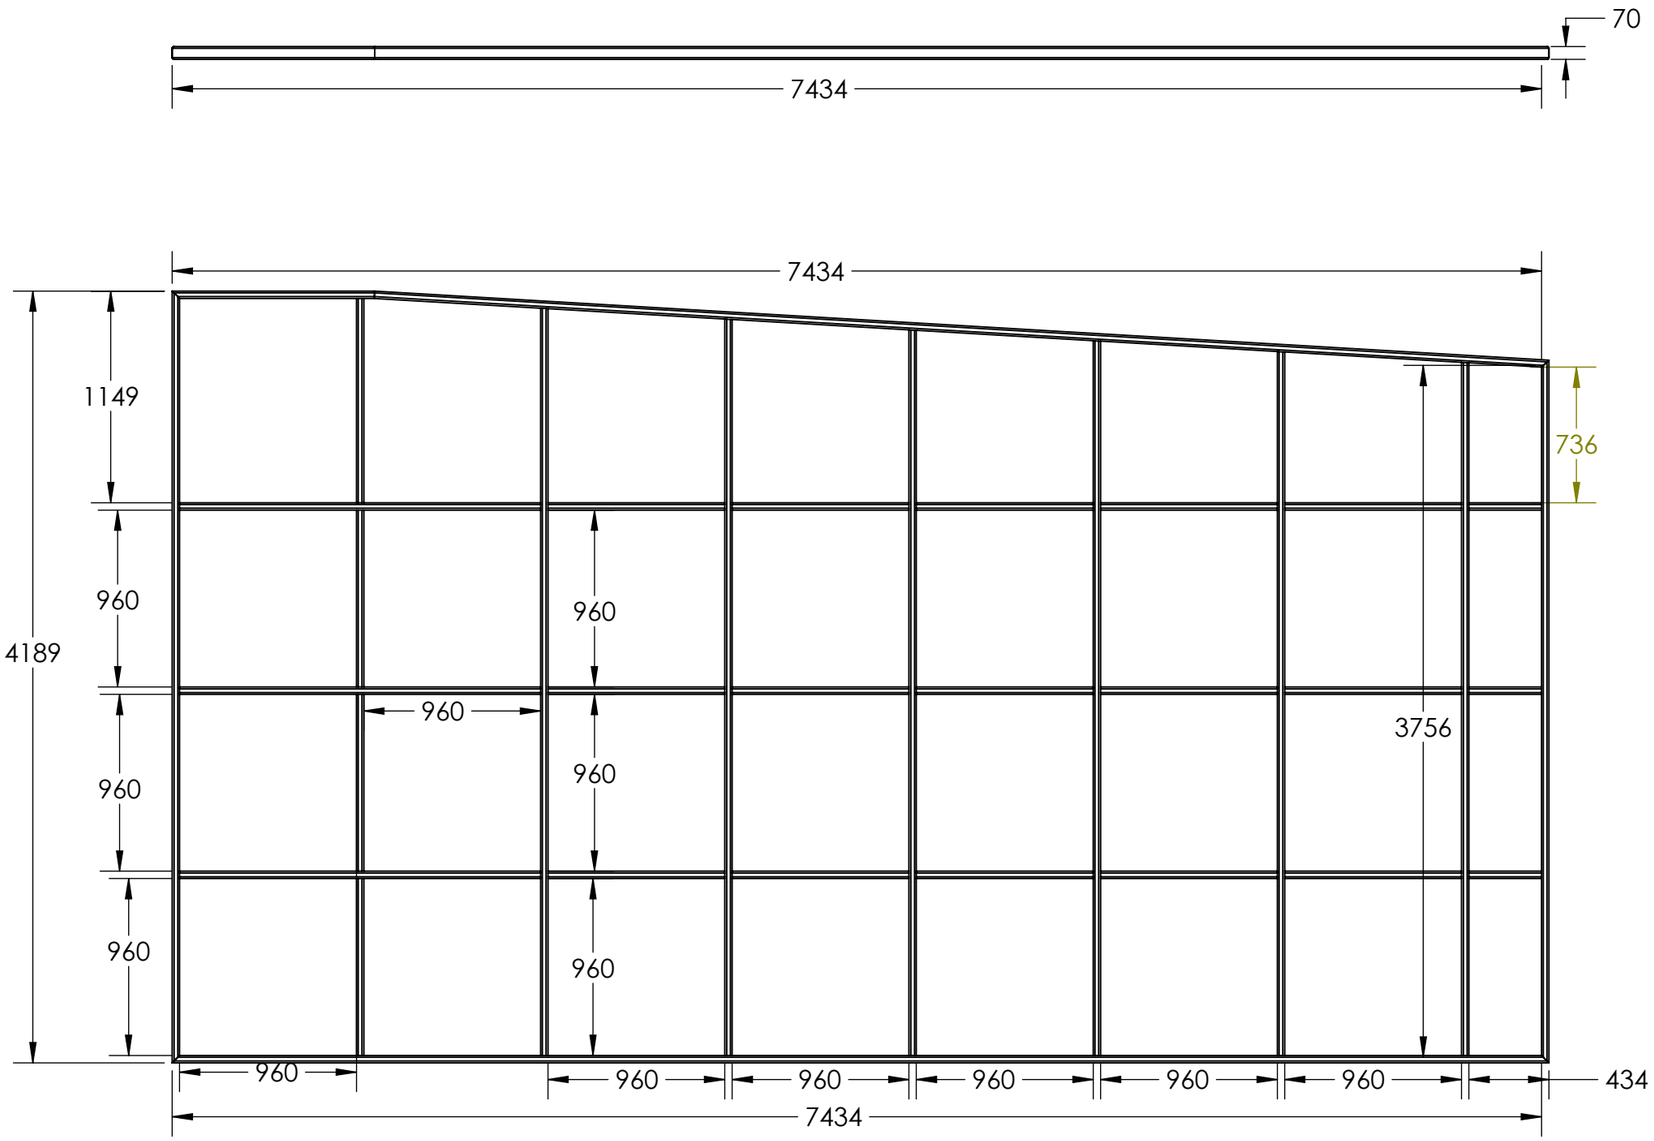

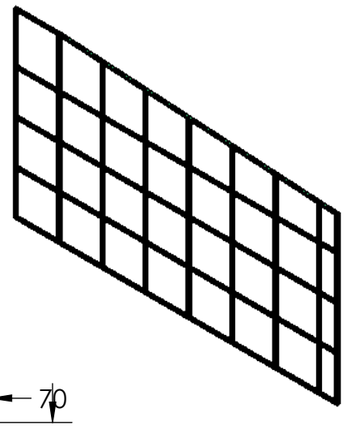

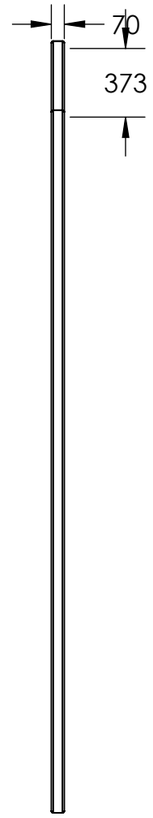

TITLE - PROFILE FOR PANEL NO-1				NIHVA TECHNOLOGIES PVT.LTD.PUNE
DWG NO - NTPL221-PROF01			QTY - 1	Website - www.nihva.com
	NAME	SIGNATURE	DATE	PROJECT NO - NTPL221
DRAWN	D.V.		20.03.2024	PRODUCT - BALCONY ENCLOSURE
CHK'D	P.M.		20.03.2024	SITE LOCATION -
APPV'D	V.T.		20.03.2024	
if any queries contact - supportautomation@nihva.com				REVISION -
ALL DIMENSION ARE IN mm			A3	SCALE - SHEET 32 OF 43