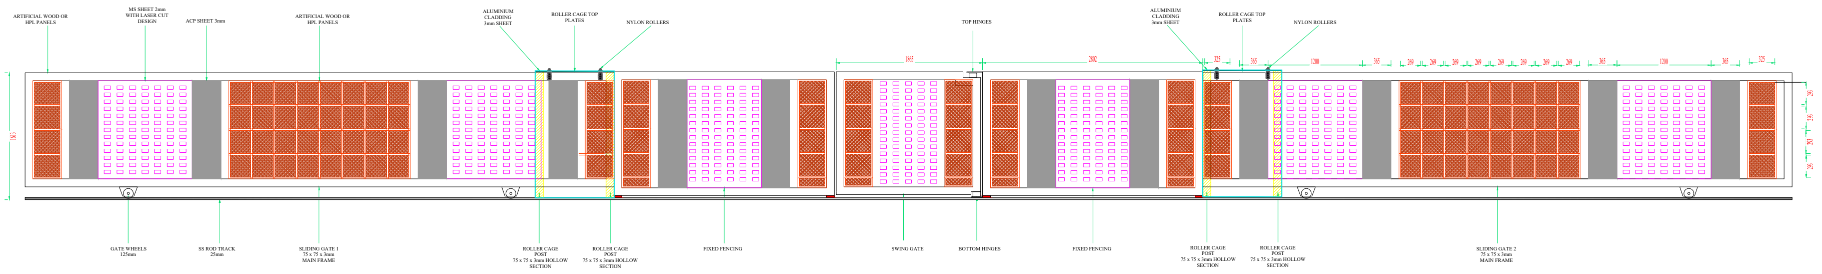
ARTIFICIAL WOOD OR HPL PANELS
MS SHEET 2mm WITH LASER CUT DESIGN
ACP SHEET 3mm
ARTIFICIAL WOOD OR HPL PANELS
ALUMINIUM CLADDING 3mm SHEET
ROLLER CAGE TOP PLATES
NYLON ROLLERS
TOP HINGES
ALUMINIUM CLADDING 3mm SHEET
ROLLER CAGE TOP PLATES
NYLON ROLLERS
1865
2802
325
365
1200
365
269
269
269
269
269
269
269
269
365
1200
365
325
1613
293
293
293
293
GATE WHEELS 125mm
SS ROD TRACK 25mm
SLIDING GATE 1 75 x 75 x 3mm MAIN FRAME
ROLLER CAGE POST 75 x 75 x 3mm HOLLOW SECTION
ROLLER CAGE POST 75 x 75 x 3mm HOLLOW SECTION
FIXED FENCING
SWING GATE
BOTTOM HINGES
FIXED FENCING
ROLLER CAGE POST 75 x 75 x 3mm HOLLOW SECTION
ROLLER CAGE POST 75 x 75 x 3mm HOLLOW SECTION
SLIDING GATE 2 75 x 75 x 3mm MAIN FRAME

VARSHA ENGINEERING FABROTICS LLP

www.varshaepl.com

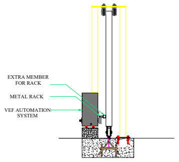

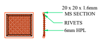

TITLE:- AUTOMATIC SLIDING GATES

CLIENT- SOBO ESTATE DEVELOPMENT PVT. LTD.

SITE :- JADE HOUSE, JUHU, MUMBAI.

DRG NO	SL-1 - FRONT VIEW
DRG VIEW	PLAN / ELEVTION
DRAWN BY	KAJAL PARMAR
CHECK BY	AJAY PARMAR
DATE	30-12-20
APPROVED DATE :-	31-12-20
APPROVED BY :-	AJAY PARMAR
REVISION	R1 on 4-4-21 | R2 on 6-6-21

www.varshaepl.com

IMPORTANT NOTES:

1.) DRAWING IS SUBJECT TO CHANGE.
2.) TOLERANCE SHALL BE AROUND 10 TO 15mm DEPENDING UPON CHANGES AND POSSIBILITIES.
3.)THIS IS THE IDEA PLAN FOR THE SAID PRODUCT.