

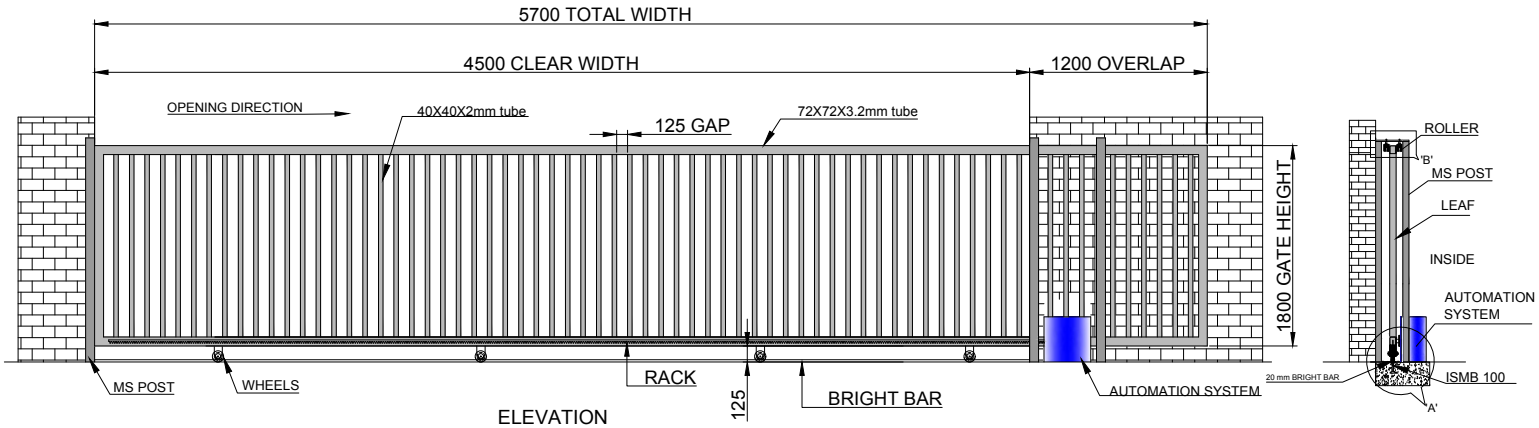


ELEVATION

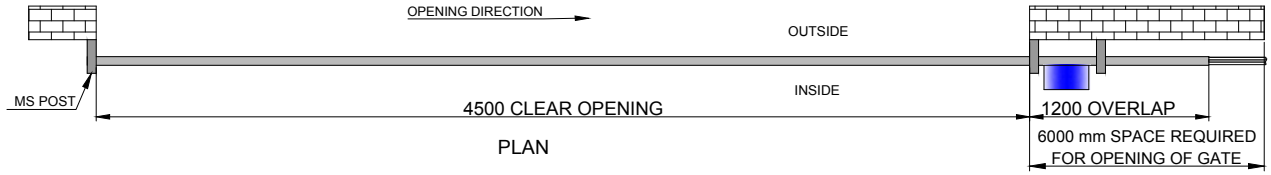

PLAN

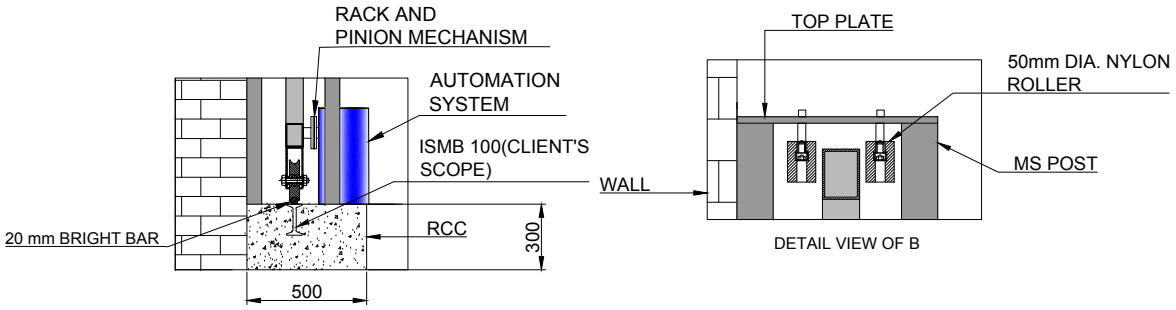

DETAIL VIEW OF A

DETAIL VIEW OF B

TOLERANCE- ±10mm

DIMENSION :

CLEAR WIDTH	CLEAR HEIGHT	QUANTITY
4500mm	1800mm	1 NO

MATERIAL:

THICKNESS :

NOTE-
1. ALL REQUIRED CIVIL WORK WILL BE IN CLIENTS SCOPE.
2. ONE COAT OF RED OXIDE & TWO COAT OF APPROVED RAL SHADE WILL BE GIVEN TO THE GATE.
3.GATE LEAF WILL BE IN TWO PARTS FOR TRANSPORTATION & WILL BE WELD TOGETHER ON SITE.

NIHVA TECHNOLOGIES PVT. LTD.
NIHVA TECHNOLOGIES PVT. LTD. PUNE
Email:- info@nihva.com
Website:- www.nihva.com

TITLE:

AUTOMATIC SINGLE LEAF SLIDING GATE

CLIENT'S APPROVAL :

CLIENT - GROUP SURYA

PROJECT - CUMMINS

SITE LOCATION -

DWG. NO. : NIHVA/19-20/0117

SCALE: NTS	WT:	SHEET:1 OF 1

DRAWN BY: P.V.A	DATE: 09.10.2019
CHECK BY :	DATE:
APPROVED BY :	DATE:

If any queries contact : design@nihva.com

NOTE: ALL DIMENSIONS ARE IN mm

THIS DRAWING & DESIGN IS THE PROPERTY OF NIHVA TECHNOLOGIES. NOT TO BE SOLD OR COPIED TO ANY OTHER CONCERN.