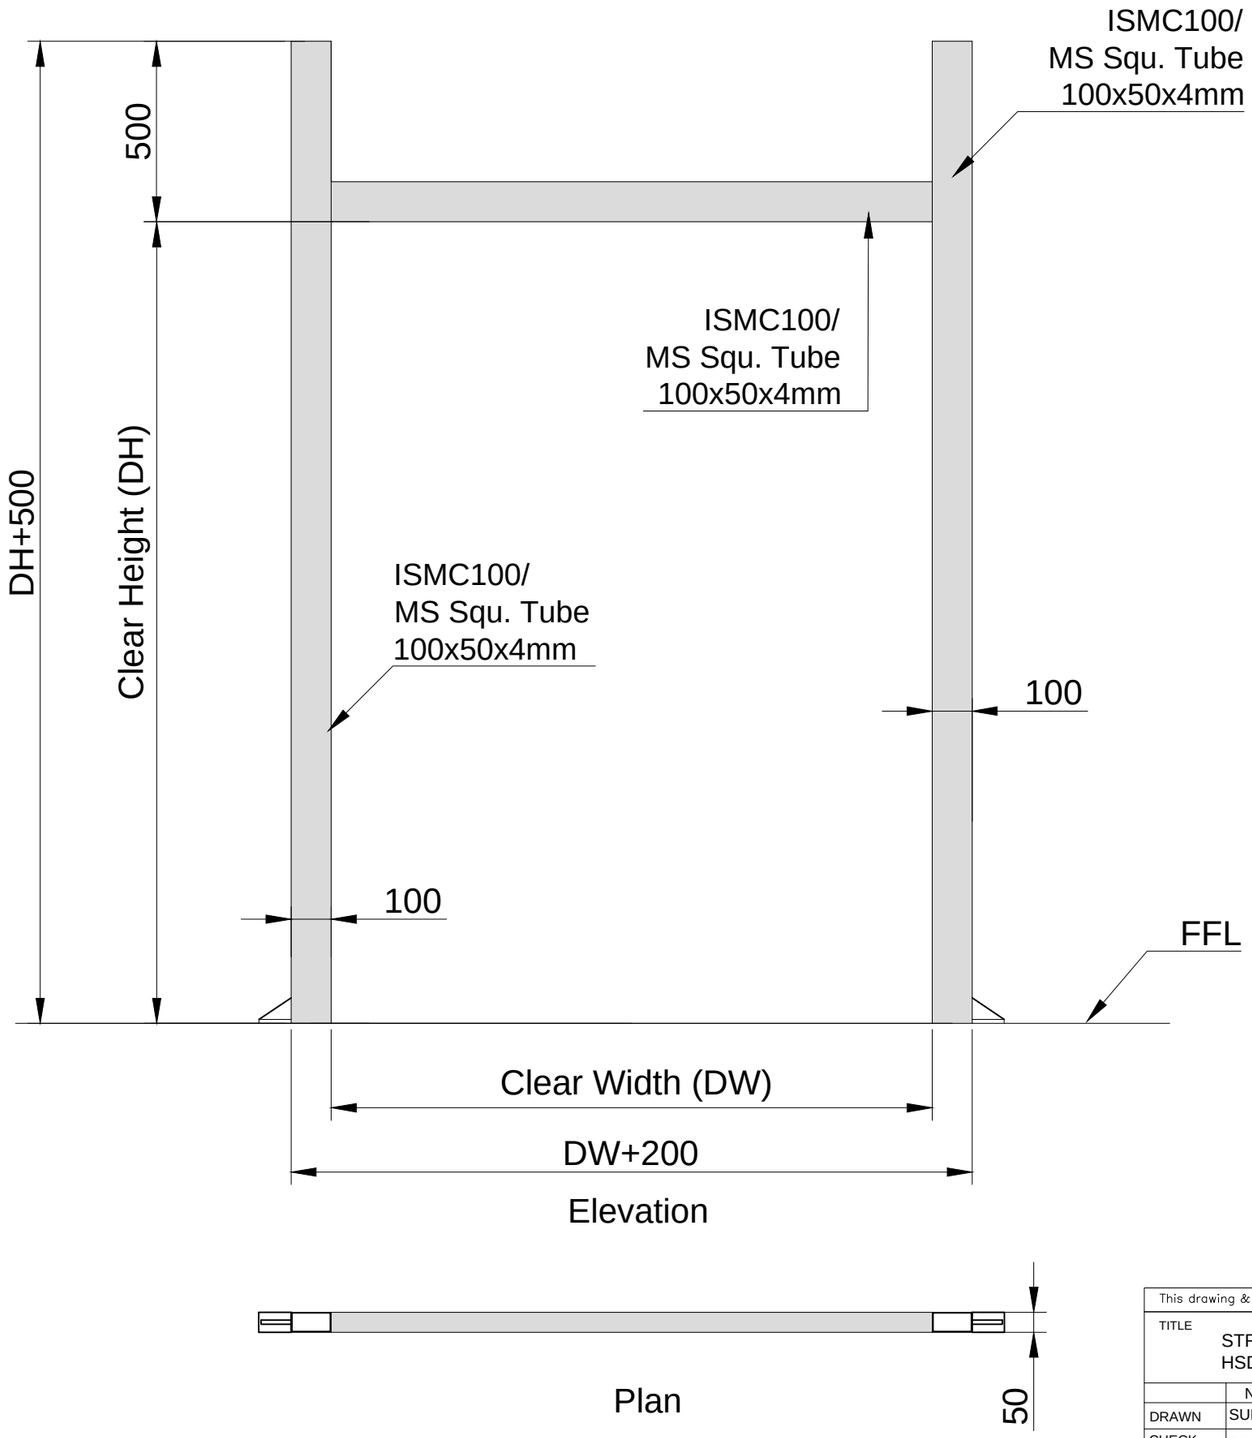


Note-
1. All Civil work will be in clients scope.

DOOR DIMENSION			
SR NO	DW	DH	QUANTITY
1	1900	2300	01

This drawing & designing is the property of NIHVA TECHNOLOGIES. Not to be sold or copied to any other concern.

TITLE
STRUCTURE FOR
HSD HS9020GHY

NIHVA TECHNOLOGIES PVT. LTD.
NIHVA TECHNOLOGIES
PVT. LTD. PUNE
Tel : 020 66304033
Email:- info@nihva.com
Website:- www.nihva.com

	NAME	SIGN	DATE
DRAWN	SURAJ		28/12/18
CHECK	PRADEEP		28/12/18
APPROVAL	R.D		28/12/18

If any queries contact : design@nihva.com

CLIENT -EMCURE PHARMACEUTICALS PVT. LTD .
PROJECT -EMCURE PHARMACEUTICALS PVT. LTD .
SITE - PUNE.
DWG. NO. : NIHVA/18-19/0221 | REV- 0
ALL DIMENSION ARE IN mm | SCALE: NTS | WT: | SHEET: 01 OF 01