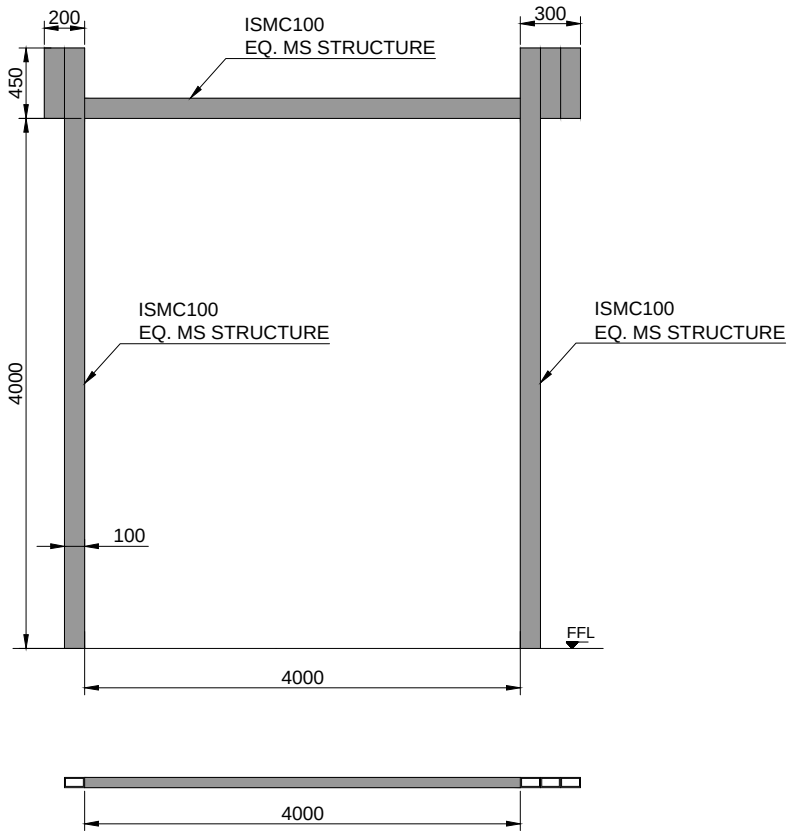


NOTE-
1. ALL CIVIL WORK WILL BE CLIENT'S SCOPE.
2.REQUIRED STRUCTURE FOR ROLLING SHUTTER SHALL BE IN CLIENT SCOPE.

This drawing & design is the property of NIHVA TECHNOLOGIES. Not to be sold or copied to any other concern.

S.N.	LOCATION	SIZE	QUANTITY
1	-	4000(W)X4000(H)	01 NOS

SR.NO.	PART DETAILS	DESCRIPTION	SIZE
01	ISMC	ISMC 100	14.250MTR

TOLERANCE - ±10mm

TITLE	ROLLING SHUTTER 4mX4m STRUCTURE			NIHVA TECHNOLOGIES PVT. LTD. PUNE
	NAME	SIGN	DATE	Tel : 020 66304033
DRAWN	SURAJ		06.12.2018	Email:- info@nihva.com
CHECK	PRADEEP		06.12.2018	Website:- www.nihva.com
APPRD.	R.D		06.12.2018	CLIENT -REWARD
If any queries contact : design@nihva.com				PROJECT -
ALL DIMENSION ARE IN mm				SITE LOCATION - RANJANGAON.
				DWG. NO. : NIHVA/18-19/0194 REV- 0
				SCALE: NTS WT: SHEET: 01 OF 01