


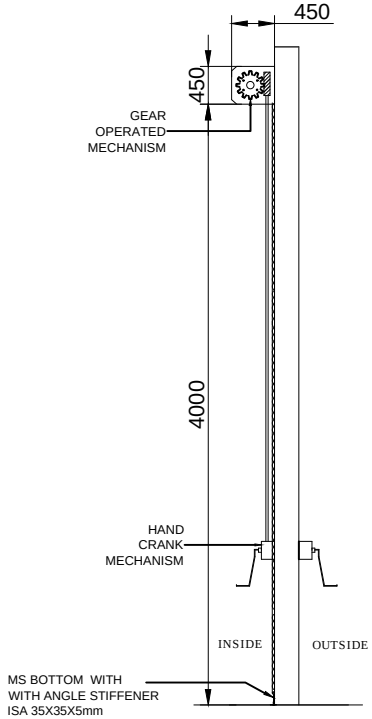


SIDE VIEW

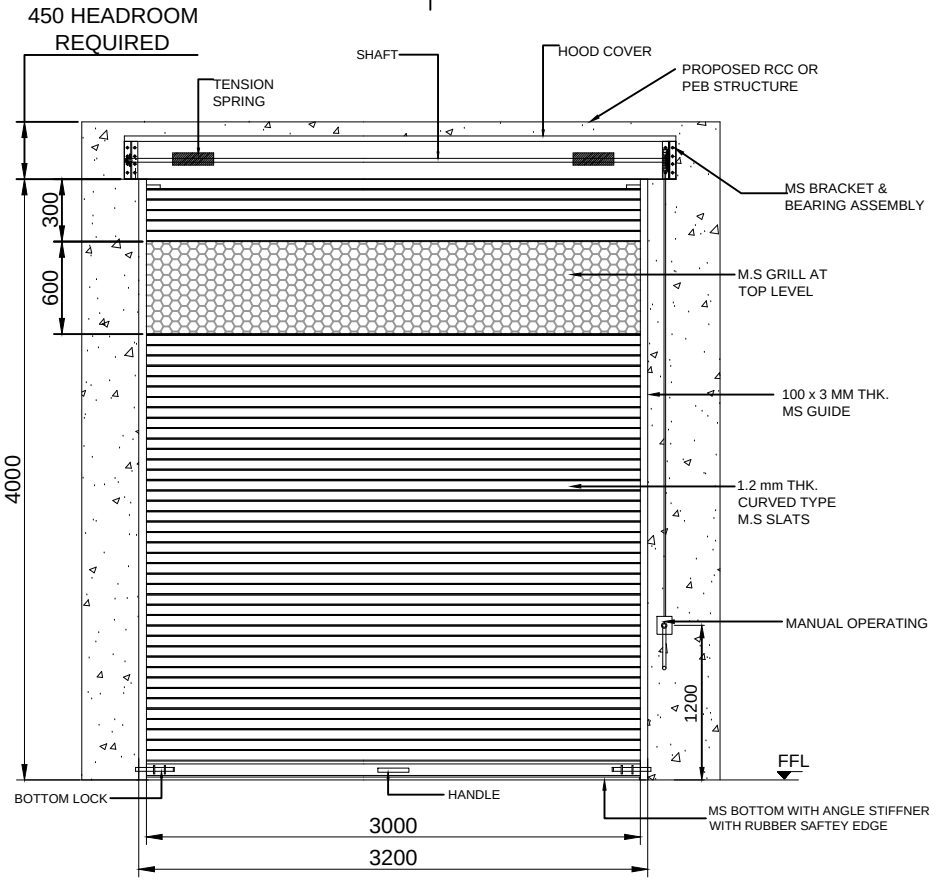


INSIDE ELEVATION

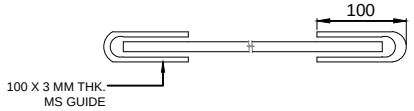


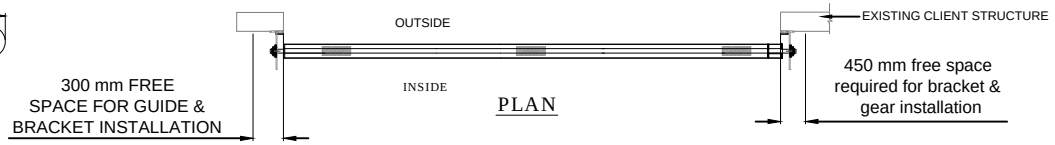


PLAN

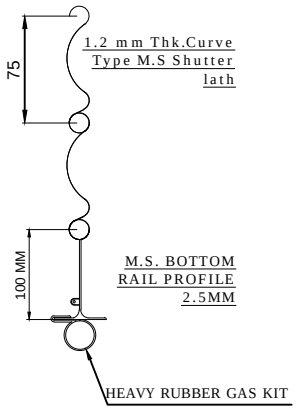

M.S. BOTTOM RAIL PROFILE 2.5MM

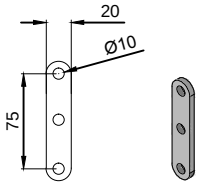

5 mm THK. LINK

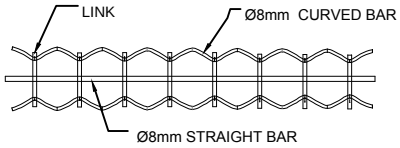

REV NO	REV DATE	DRAWN	REMARK
R03	06.11.2019	P.A	1. GRILL POSITION CHANGE 2. CLEAR HEIGHT CHANGE
R02	05.11.2019	P.A	1. GRILL POSITION CHANGE 2. SLAT THICKNESS CHANGE
R01	19.10.2019	P.A	1. GRILL ADDED

TOLERANCE - ±10mm

This drawing & design is the property of NIHVA TECHNOLOGIES. Not to be sold or copied to any other concern.

TITLE	GEAR OPERATED ROLLING SHUTTER 3m X 4 m Right side gear box.		
	NAME	SIGN	DATE
DRAWN	P.A		16.10.2019
CHECK	G.J		16.10.2019
APPRD.			

NIHVA TECHNOLOGIES PVT. LTD.
NIHVA TECHNOLOGIES PVT. LTD. PUNE
Tel : 020 66304033
Email:- info@nihva.com
Website:- www.nihva.com

CLIENT - PROGRESSIVE INFRA PROJECT PVT. LTD.

PROJECT -

SITE LOCATION - PUNE

If any queries contact : design@nihva.com

DWG. NO. : NIHVA/19-20/0136/R03 REV- R03

ALL DIMENSION ARE IN mm

SCALE: NTS WT: SHEET: 01 OF 01

NOTE-
1. ALL CIVIL WORK WILL BE CLIENT'S SCOPE.
2.STRUCTURE REQUIRED FOR SHUTTER IS IN CLIENT'S SCOPE.
3.FINAL FINISH OF SHUTTER WILL BE IN POWDER COATING OF APPROVED COLOR .