

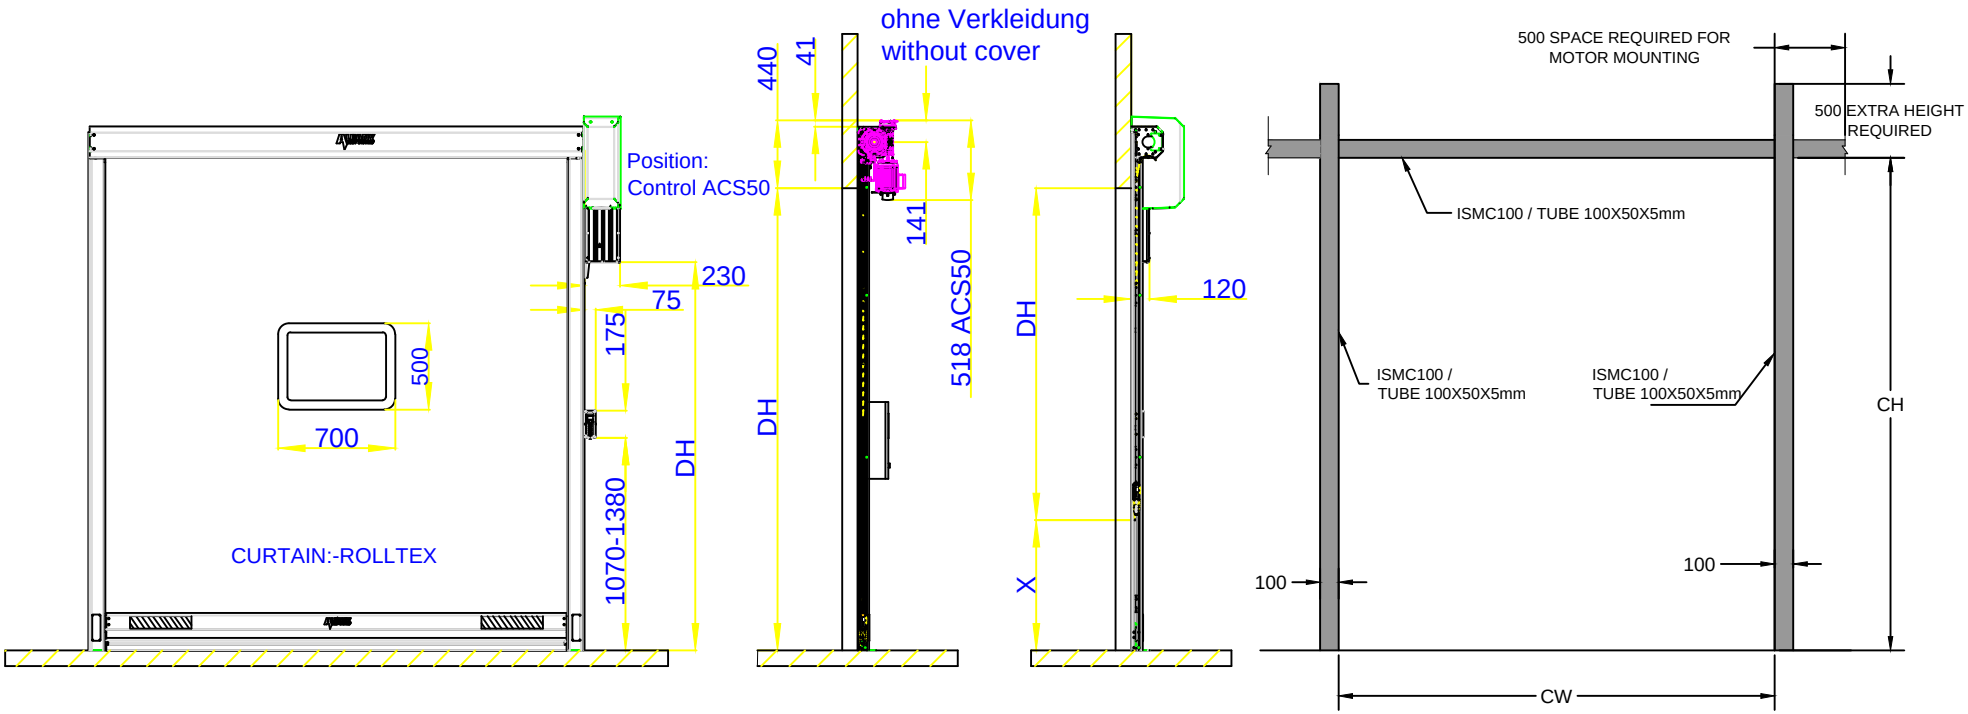


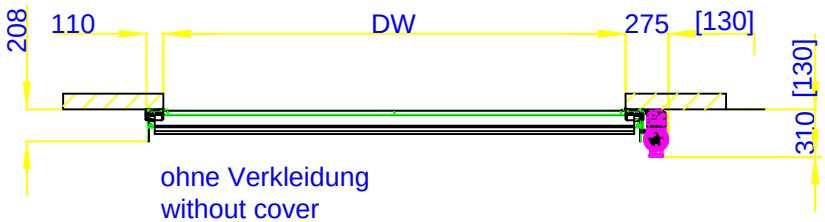

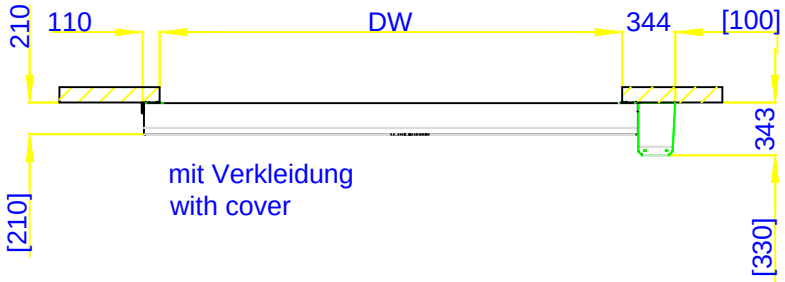

Tolerance ±3 mm (for all dimensions)

Dimensions in [ ] ==> clearance for installation

RAL : 5010 BLUE
CURTAIN:-ROLLTEX

CLEAR WIDTH	CLEAR HEIGHT	QTY
1500	900	1 NOS

This drawing & design is the property of NIHVA TECHNOLOGIES. Not to be sold or copied to any other concern.

TITLE
HIGH SPEED DOOR
RP300 & STRUCTURE

	SIGN	DATE
DRAWN	SURAJ	18/08/17
CHECK	SAGAR P.	18/08/17
REV.		
APPROVAL	SHEKHAR	18/08/17

If any queries contact : projects@nihva.com

ALL DIMENSION ARE IN mm

NIHVA
NIHVA TECHNOLOGIES PVT. LTD.
NIHVA TECHNOLOGIES
PVT. LTD. PUNE
Tel : 020 66304033
Email:- info@nihva.com
Website:- www.nihva.com

CLIENT - PENGUIN

PROJECT -

SITE LOCATION- COIMBATORE

DWG. NO. : NIHVA/17-18/0155

SCALE: NTS | WT: | SHEET: 01 OF 01