


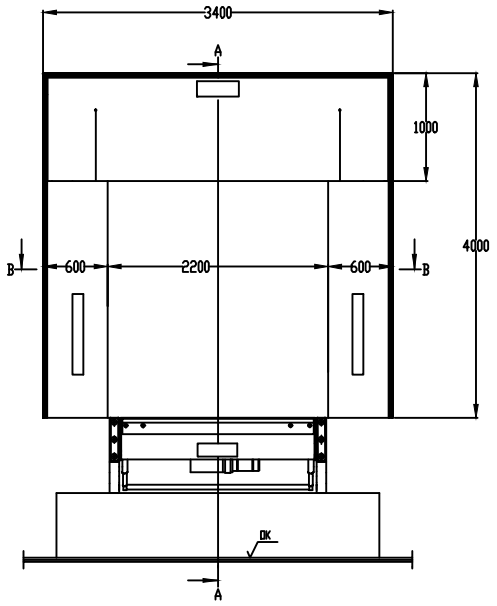


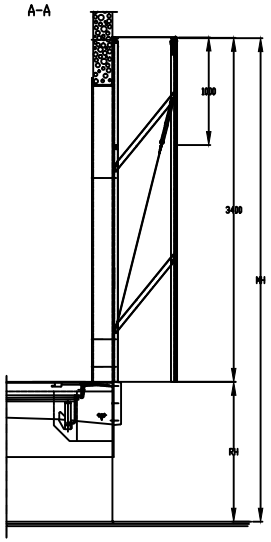

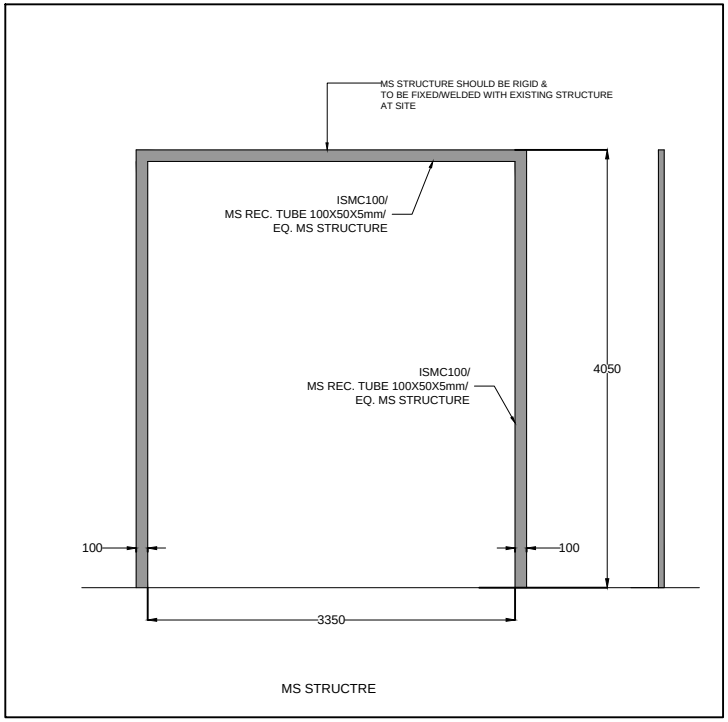

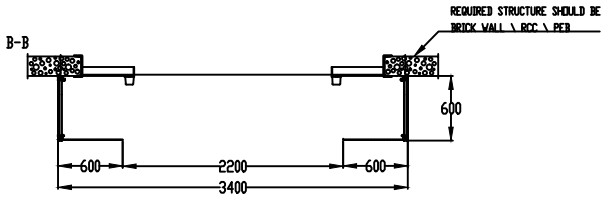

NW	NH	QTY
3400	4000	03 NOS

NOTE:- REQUIRED MS STRUCTURE , FITTING & ALL CIVIL WORK IS IN CLIENT SCOPE .

TOLERANCE - ±10mm

This drawing & design is the property of NIHVA TECHNOLOGIES. Not to be sold or copied to any other concern.

TITLE: DOCK SHELTER WITH MS STRUCTURE

NIHVA TECHNOLOGIES PVT. LTD.
NIHVA TECHNOLOGIES PVT. LTD. PUNE
Tel : 020 66304033
Email:- info@nihva.com
Website:- www.nihva.com

	NAME	SIGN	DATE
DRAWN	S.M.S.		10.12.2020
CHECK	A.P.		10.12.2020
APPRD.			

CLIENT - SCON PROJECTS PVT LTD
PROJECT - SCON PROJECTS PVT LTD
SITE LOCATION - PUNE

If any queries contact : projectsupport@nihva.com
DWG. NO. : NIHVA/20-21/0107 REV- R00
ALL DIMENSION ARE IN mm
SCALE: NTS WT: SHEET: 01 OF 01