



TOLERANCE :- ± 10mm

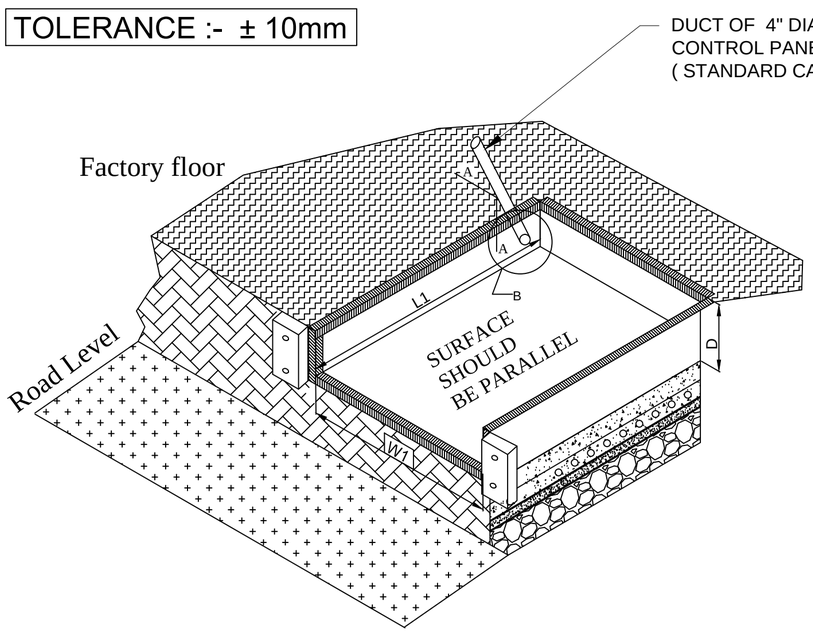


PIT DRAWING (CLIENT SCOPE)

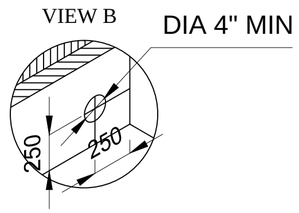

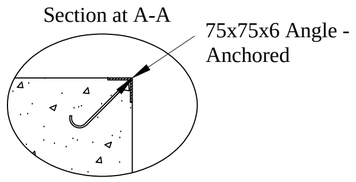


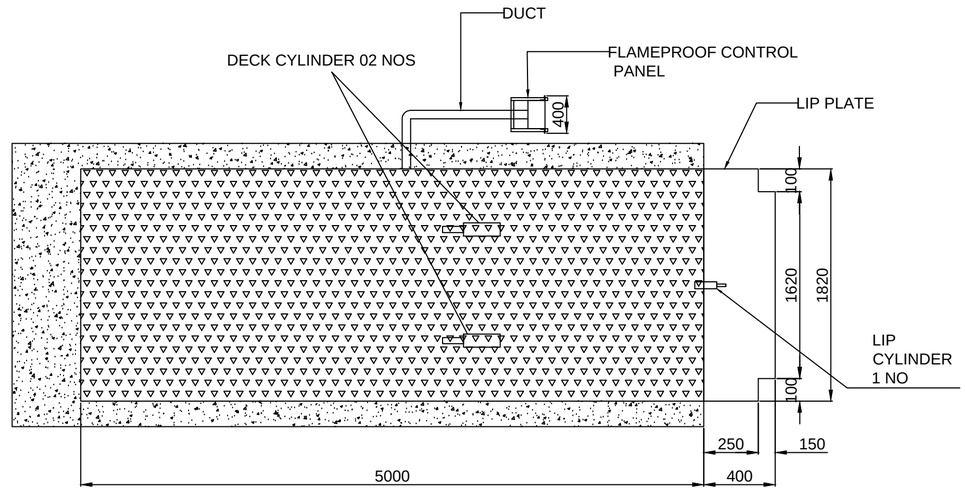

DOCK LEVELER TOP VIEW

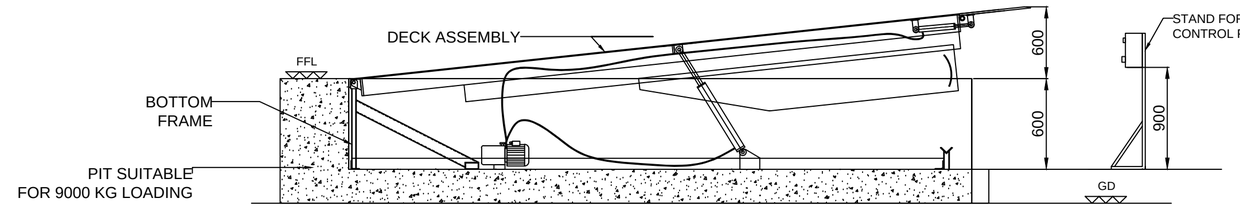


DOCK LEVELER LIP UP FRONT VIEW

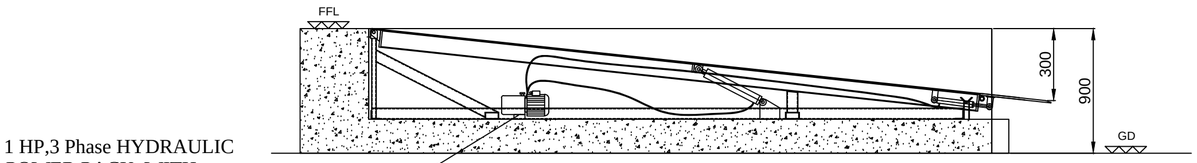

DOCK LEVELER LIP DOWN FRONT VIEW

SPECIFICATIONS OF DOCK LEVELER		
SR NO	**PARAMETER**	**REMARK**
1	TYPE OF DOCK LEVELER	PIT MOUNTED HYDRO-ELECTRIC DOCK LEVELER
2	CAPACITY	6 TON
3	DECK OPERATION	LIFTING BY HYDRAULIC CYLINDER
4	LIP OPERATION	OPERATED BY HYDRAULIC CYLINDER
5	OPERATION CONTROL	BY PUSH BUTTONS ON CONTROL PANEL
6	CHEQUERED PLATFORM SIZE	1820 MM (W) X 5000 MM (L)
7	DOCK HEIGHT	600 MM
8	LIP UP (+)	600 MM
9	LIP DOWN (-)	300 MM
10	PLAIN TOP LIP SIZE	1820 MM (W) X 400 MM (L)
11	LEVEL OF FACTORY FLOOR FROM GROUND	900 MM
12	PIT SIZE	1870MM (W) X 5100 MM (L) X 605 MM (H)
13	MATERIAL OF CONSTRUCTION	MILD STEEL
14	PAINT	FIROZI BLUE
15	QTY	2 NOS

NOTE: -
1. PROPER DRAINAGE SHOULD BE DONE.
2. TRENCH AS SHOWN SHOULD BE MADE BY DECIDING THE POWER PACK POSITION (SUPPLY CABLE LENGTH STD. 5000 MM).
3. LEVEL OF THE PIT SHOULD BE PLAIN AND SHOULD TAKE AT LEAST 9000 KG FLOOR LOADING .
4. MOUNTING ARRANGEMENT FOR BUMPERS SHOULD BE MADE AS PER BUMPER DRAWING.
5. FABRICATION TOLERANCE FOR PLATFORM SIZE WILL BE + 10 MM.
6. DOCK LEVELER CAPACITY IS OF 6 TON AFTER RESTING OF LIP ON DOCK LEVELER.
7. CYLINDERS PROVIDED ARE USED ONLY FOR LIFTING OF BARE DOCK (NO LOAD ON DECK) & CAN NOT LIFT DECK IN LOADED CONDITION WITH OTHER LOADS.
8 . REQUIRED DUCT , BOLT FOR ANCHORING ANGLE , PIT & ALL CIVIL WORK IS IN CLIENT SCOPE.
9 . ALL STRUCTURE PAINT COLOR IS FIROZI BLUE AS PER STANDARD & OTHER BOUGHTOUT COLOUR WILL BE AS PER ORIGINAL EQUIPMENT MANUFACTURER STANDARD .

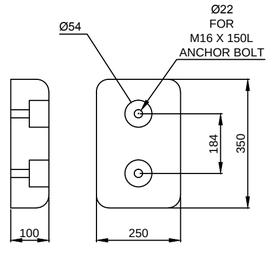

BUMPER DETAILS

DOCK LEVELER SIZE	WIDTH (W)	LENGTH (L)	HEIGHT (H)	LIP (C) LENGTH	BUMPER SIZE
	1820	5000	600	400	250X350X100

PIT DIMENSION	WIDTH (W 1)	LENGTH (L 1)	DEPTH (D)	ALL DIMENSIONS ARE IN mm
	1870	5100	605	

This drawing & design is the property of NIHVA TECHNOLOGIES. Not to be sold or copied to any other concern.

TITLE				
DOCK LEVELER - 6 TON				NIHVA TECHNOLOGIES PVT. LTD. PUNE Tel : 020 66304033 Email:- info@nihva.com Website:- www.nihva.com
	NAME	SIGN	DATE	
DRAWN	S.M.S.		13.2.2021	CLIENT - L & T HYDRO CARBON ENGG. LIMITED
CHECK	A.K.		12.2.2021	PROJECT - HPCL RUF
APPRD.				SITE LOCATION - VISAKHAPATNAM
If any queries contact : design@nihva.com				DWG. NO. : NIHVA/20-21/0157 REV- R00
ALL DIMENSION ARE IN mm				SCALE: NTS WT: SHEET: 01 OF 01