


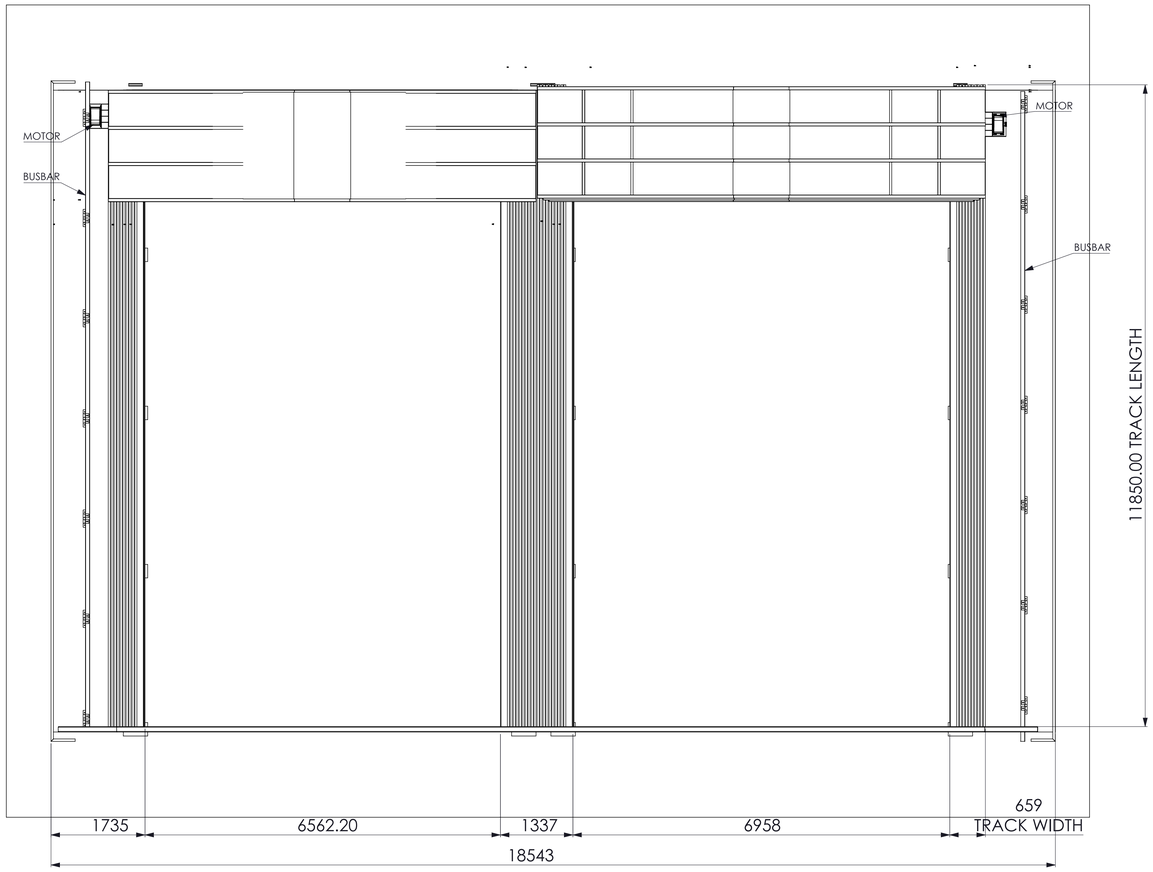


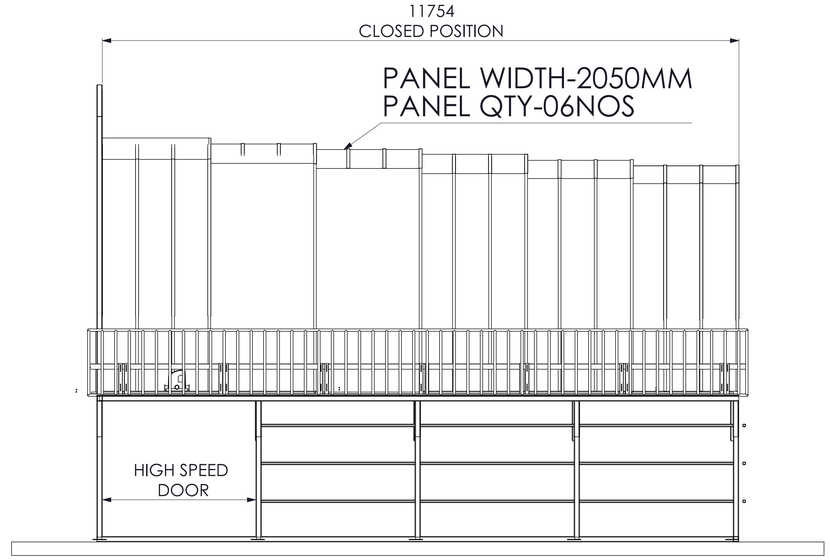

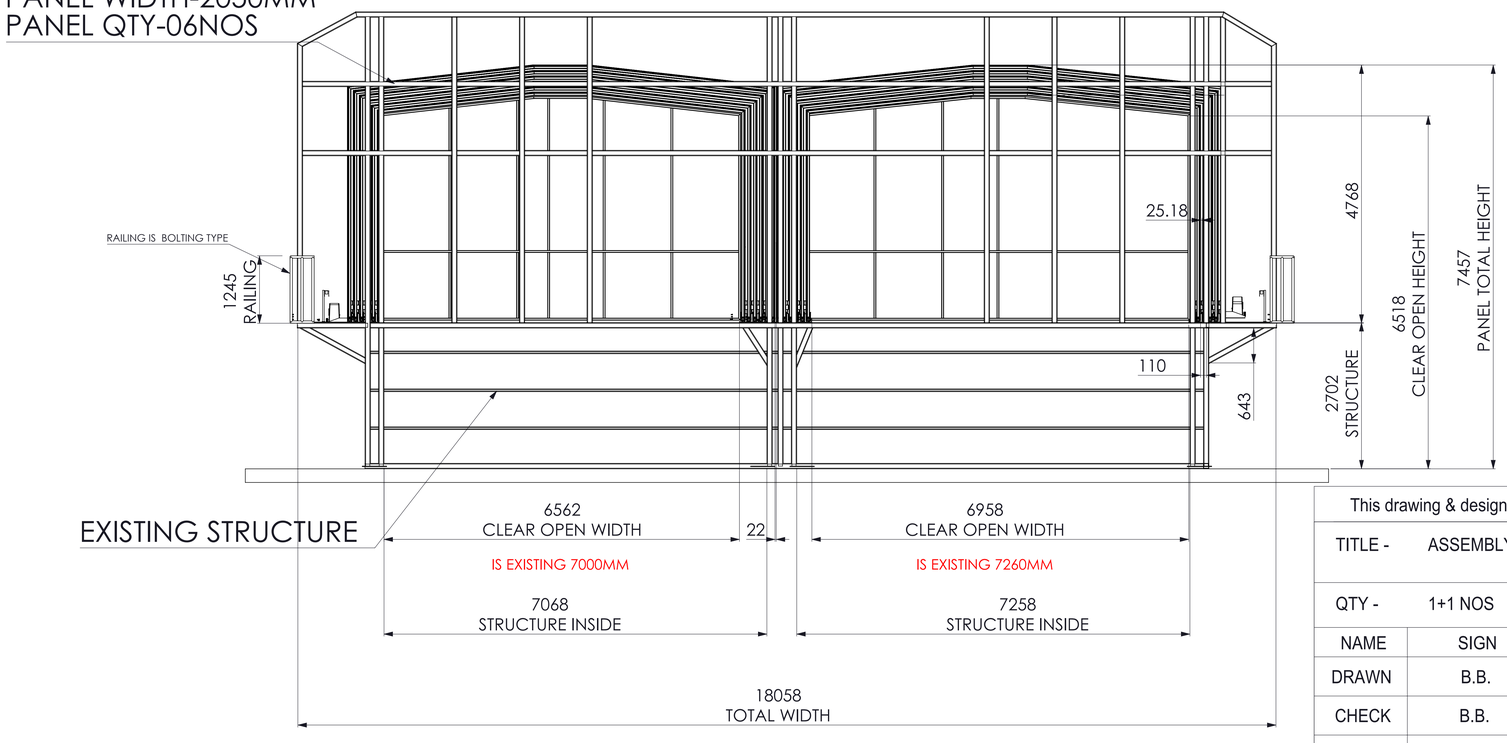

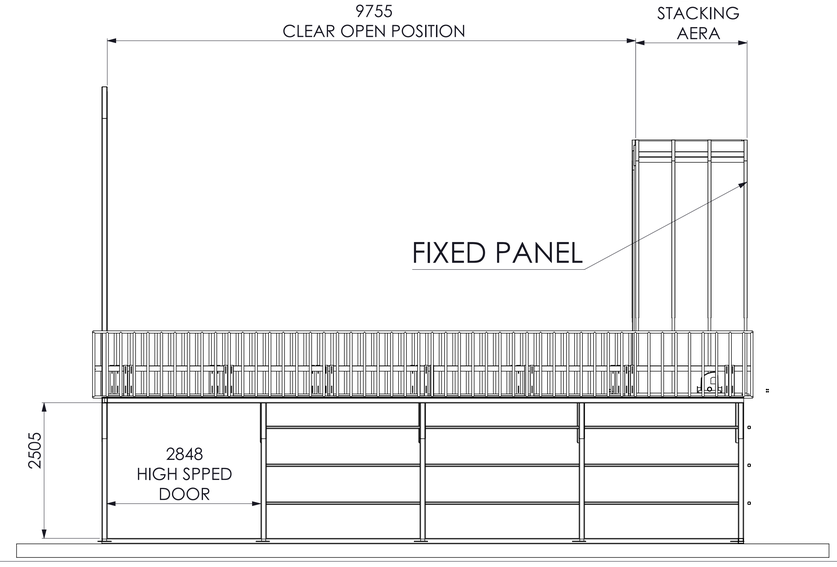

This drawing & design is the property of NIHVA TECHNOLOGIES. Not to be sold or copied to any other concern.

TITLE - ASSEMBLY LINE 3 & 4 ROOF ENCLOSURE				NIHVA TECHNOLOGIES PVT. LTD.
QTY - 1+1 NOS				
NAME	SIGN	DATE		
DRAWN	B.B.	20/09/24		CLIENT - NTPL - 202407-T & R
CHECK	B.B.	20/09/24		LOCATION -
APPRD.	V. T.	20/09/24		PRODUCT - ASSEMBLY LINE 3 & 4 ROOF ENCLOSURE
				DWG NO - NTPL-202407-T & R / REV- 02
ALL DIMENSION ARE IN mm				SCALE: / SHEET: