



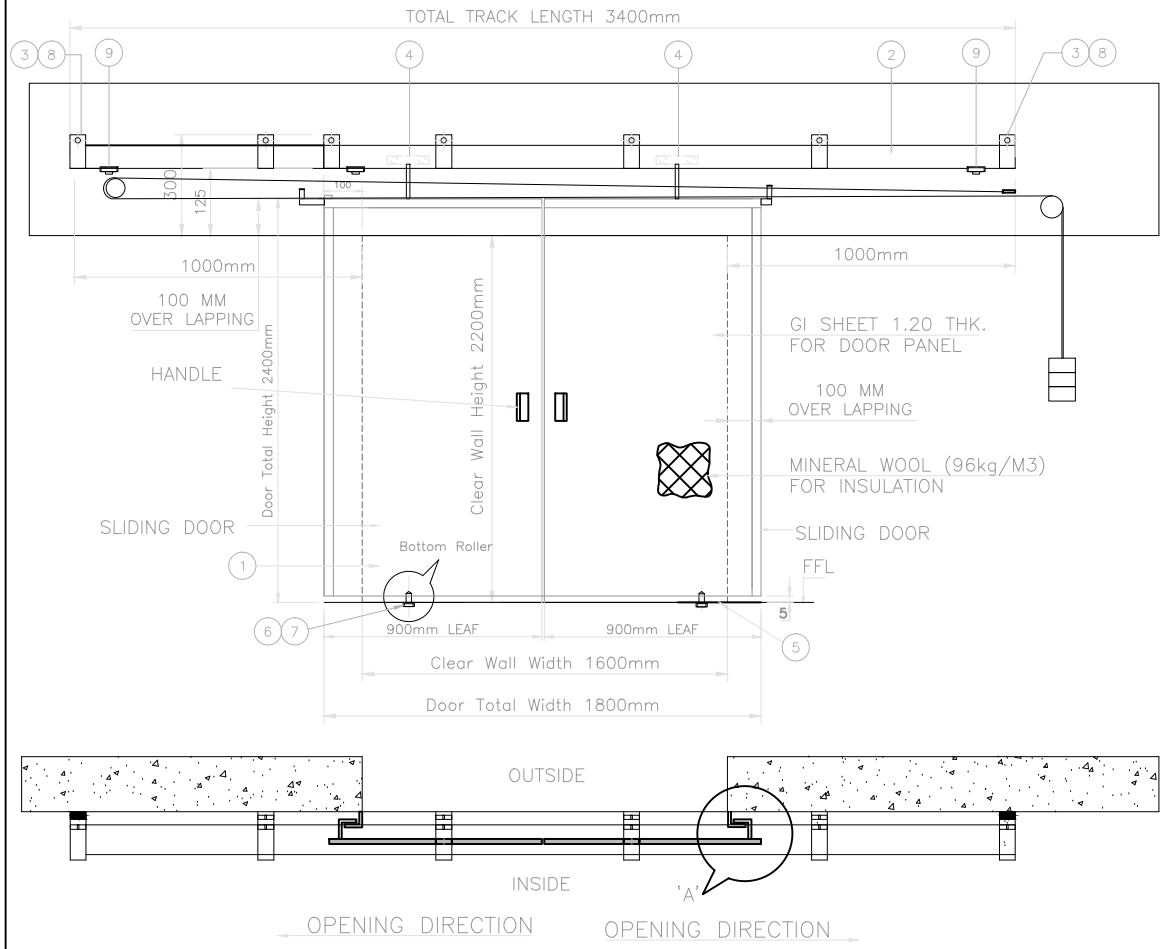


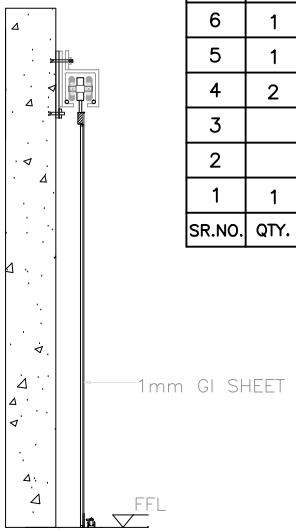

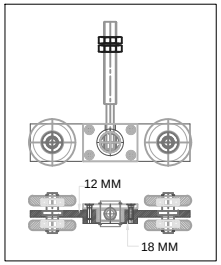


DETAIL AT 'B'

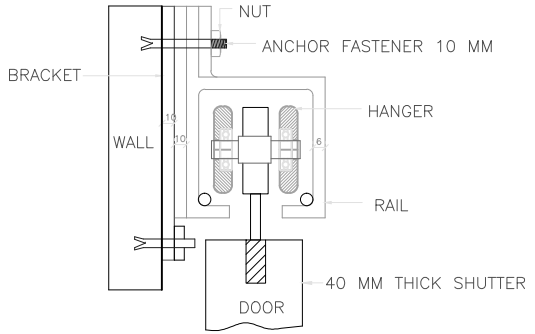

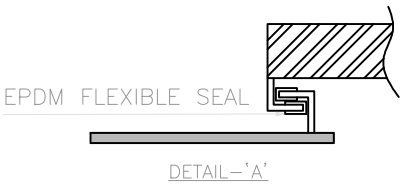

DETAIL–'A'

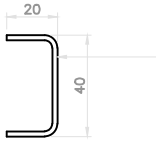

'C' SECTION USING AGAINST HOLLOW SECTION 70x40.

DETAIL–C PROFILE FOR FRAME

9	1	STOPPER (FOR HANGER ASSLY.)
8	1	COVER (FOR TRACK BKT.)
7	1	BOTTOM ROLLER MTG. FLAT (BOTTOM ROLLER BKT.)
6	1	BOTTOM ROLLER ASSLY.
5	1	'Z' SECTION
4	2	HANGER ROLLER ASSLY./PANEL
3		TRACK BRACKET
2		SLIDING TRACK
1	1	SLIDING DOOR & FRAME / BACK SUPPORT SQ. TUBE
SR.NO.	QTY.	DESCRIPTION

NOTE : DOOR OVERLAPING 100mm AT RH & LH AND TOP SIDE
ALL DIMENSIONS ARE IN MM.
CLIENT SHOULD CONFIRM DOOR OPENING DIRECTION.

TOLERANCE:- ± 10mm

DOOR DIMENSION		
CLEAR WIDTH	CLEAR HEIGHT	
1600mm	2200mm	01NOS

Panel Make : - Radient Safe Door Make

REV	DESCRIPTION	DRAWN	DATE
R03	AL DROP LOCKING ARRANGEMENT REMOVE	A.K.	05.15.2018
R02	DRG. REVISED AS PER MARK.	A.K.	29.11.2018
R01	PANEL DETAIL ADDED	A.K.	28.11.2018

This drawing & designing is the property of NIHVA TECHNOLOGIES. Not to be sold or copied to any other concern.

TITLE			
AUTOMATIC SLIDING DOOR			
	NAME	SIGN	DATE
DRAWN	SURAJ		21/11/18
CHECK	P.A		20/11/18
APPROVAL	R.D		20/11/18

NIHVA TECHNOLOGIES PVT. LTD. PUNE
Tel : 020 66304033
NIHVA TECHNOLOGIES PVT. LTD.
Website:- www.nihva.com
Email:- info@nihva.com

CLIENT - RATNARUP PROJECT PVT. LTD.
PROJECT -RATNARUP PROJECT PVT. LTD.
SITE - BANNER,PUNE.

If any queries contact : design@nihva.com
ALL DIMENSION ARE IN mm
DWG. NO. : NIHVA/18-19/0181/R02 | REV-02
SCALE: NTS | WT: | SHEET: 01 OF 01