



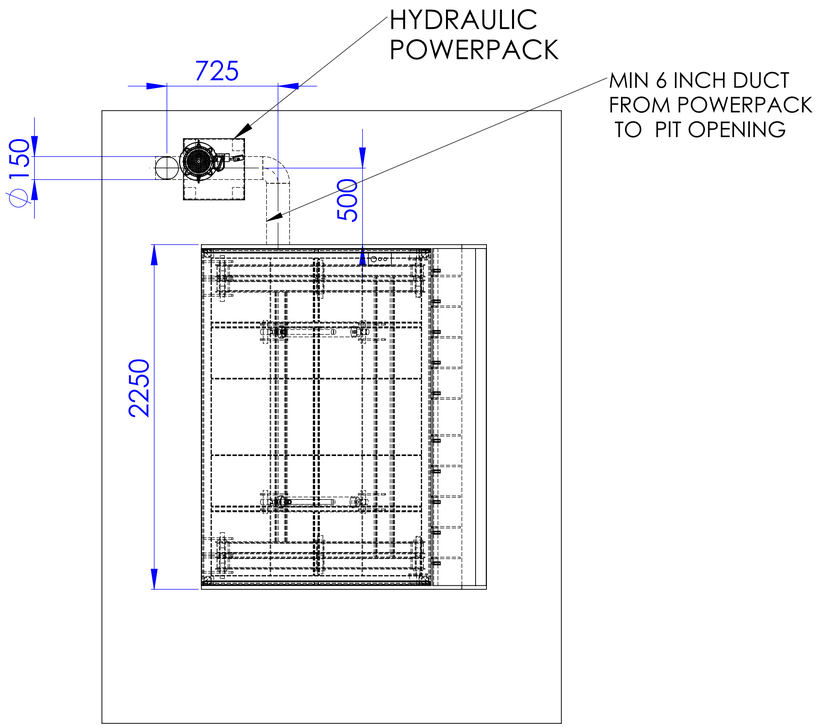


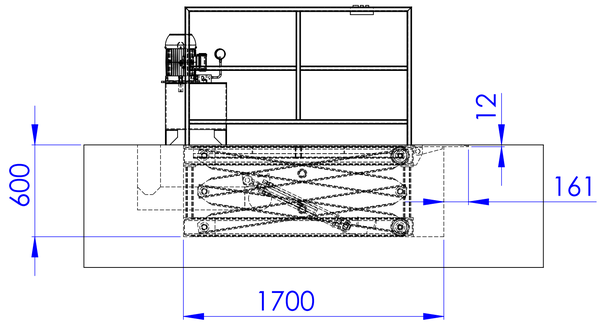


INSTALLATION LAYOUT

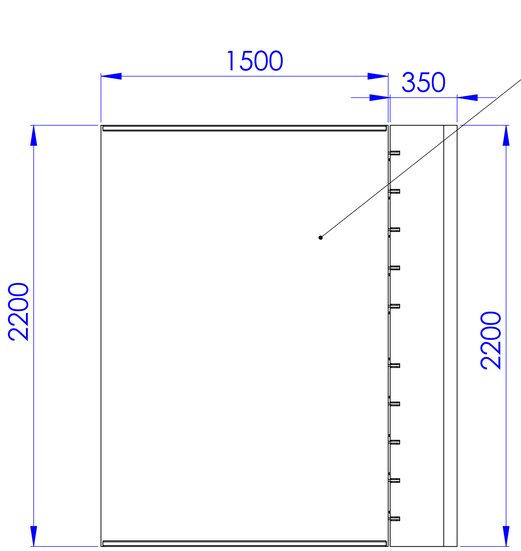

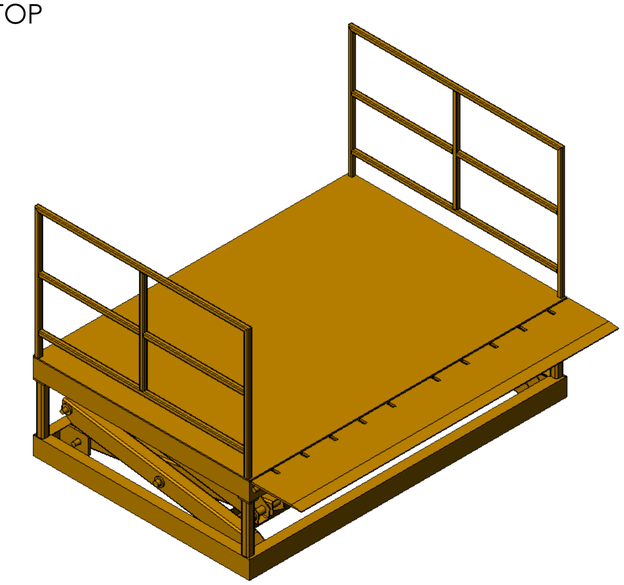

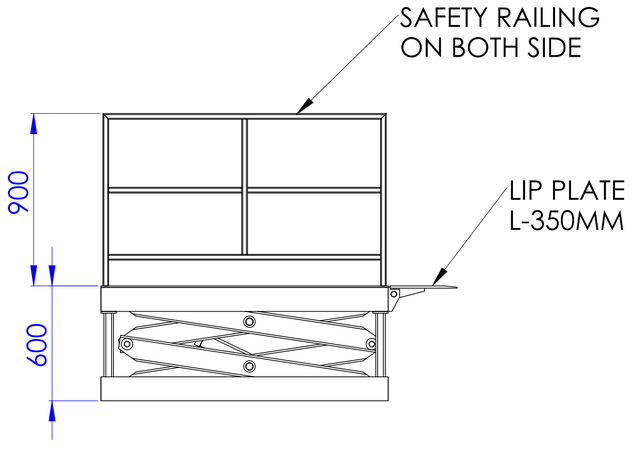

SCISSOR LIFT

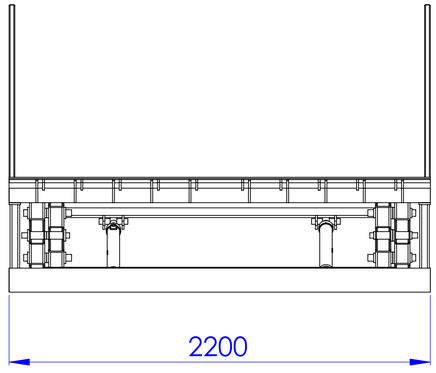

SPECIFICATION OF PIT MOUNTED ELECTRO-HYDRAULIC SCISSOR LIFT-

1. PLATFORM SIZE- 1500LX2200W
2. CAPACITY - 3 TON
3. CLOSE HEIGHT - 600 MM
4. LIFT HEIGHT - 1500 MM
5. TOTAL HEIGHT FROM PIT BOTTOM - 2100MM
6. PLATFORM LIFTING BY 2 NOS OF HYDRAULIC CYLINDER
7. OPERATION CONTROL - PENDANT WITH PUSH BUTTON MOUNTED ON RAILING
8. HYDRAULIC POWERPACK - 1HP , 3 PHASE AC
9. LIFTING TIME - 60 SEC
10. MANUAL LIP ON ONE SIDE , LIP LENGTH-350 MM
11. CLEAR PIT DIMENSION - 1700LX2250WX600D
12. REQUIRED PIT , DUCT FOR HOSES & ALL CIVIL WORK IS IN CLIENT SCOPE .
13. DETAILED CIVIL DRAWING WILL BE PROVIDED AFTER CONFIRMATION OF ORDER.
14. FINISH- PAINTING WITH GOLDEN YELLO (RAL 1004) , IF OTHER PLEASE SPECIFY .

UNLESS OTHERWISE SPECIFIED:
DIMENSIONS ARE IN MILLIMETERS
SURFACE FINISH:
TOLERANCES:
LINEAR:
ANGULAR:

NIHVA
We Make Possible

DEBURR AND BREAK SHARP EDGES

DO NOT SCALE DRAWING | REVISION

	NAME	SIGNATURE	DATE
DRAWN	SIDDHESHWAR		28.6.2021
CHK'D	V.T.		28.6.2021
APPV'D			
MFG			
Q.A			

MATERIAL:

WEIGHT:

TITLE:
PIT MOUNTED SCISSOR LIFT 3 TON

DWG NO. NIHVA/21-22/028/SL

A1

SCALE:1:20 | SHEET 1 OF 1