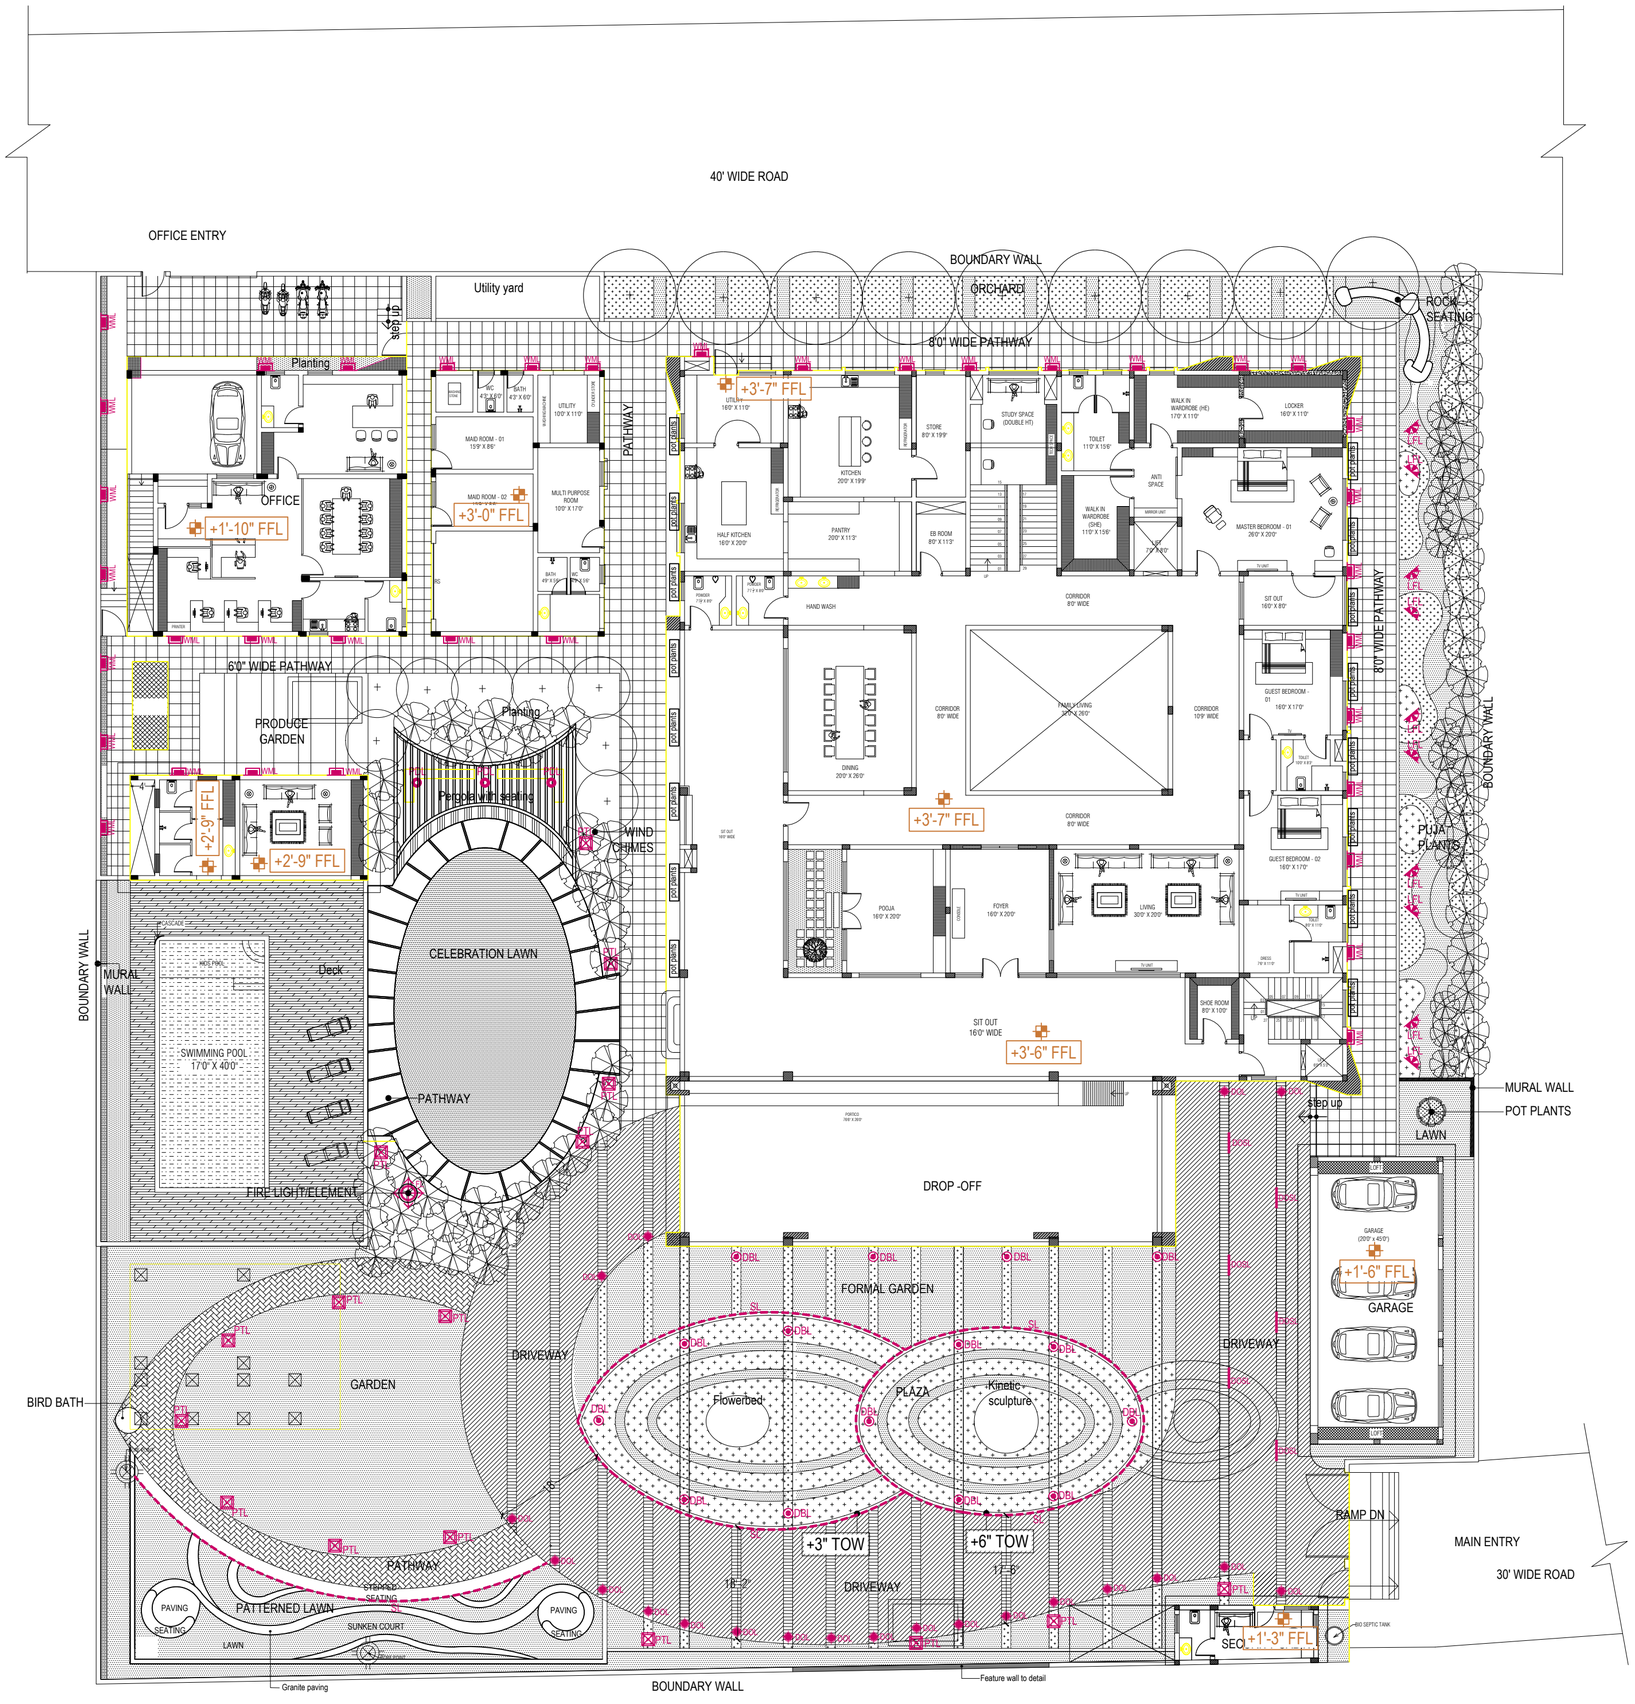


LIGHTING SCHEDULE

S.No	Symbol	Description	Quantity
01	PTL	Post top Light	16 nos
02	DBL	Decorative Bollard Light	15 nos
03	SL	Strip Light	97 RM
04	LFL	Landscape focus Light	10 nos
05	FL	Fire Light	1 nos
06	PDL	Pergola down light	3 nos
07	WML	Wall mounted light	37 nos
08	DOL	Drive Over Light	21 nos
09	DOSL	Drive Over Strip Light	6 RM

NOTE:

- WML fixing above the lintel height

This drg. is the property of RAVIKUMAR AND ASSOCIATES and shall not be passed on to any person not authorised by us to recieve it. It shall not be copied / modified in part or full without our prior permission.The details furnished in this drg. are for this PROJECT only.

DRAWING STATUS

SCHEME FOR APPROVAL	✓
ONLY FOR TENDER	
ADVANCE COPY	

No	Date	Revision	Drawn
01	03.04.26	Scheme revised as per client's feedback	Abarna

NOTES:

1. All dimensions are in feet & inches.
2. All levels are in feet & inches.
3. All levels indicated are finished levels.
4. Only written dimensions to be followed,
5. Refer STRUCTURAL CONSULTANT'S drawings & details for all FOUNDATIONS,SUB BASES all other structural elements including ROOF Water proofing & other related works.
6. Refer MEP Consultant's drawing/details for all Storm water drains, catch basins, swales, RWP etc/ Electrical routing & other entities etc.
7. For items mentioned as 'VENDORS SHOP DRAWINGS' shall be vetted by the Landscape Architect before execution.
8. This drg has to be read and co-ordinated with the following revised and updated detail dwgs.
   a. Material finishes
   b. Hard landscape sections and details
   c. Settingout plans
   d. Soft landscape details
   e. Planting schedules
   f. BOQ and Specifications
   g. Irrigation layout
   h. Lighting schedule
   i. Grading plan
   j. External service coordination
   k. Other structural, MEP and other Service consultant's details
9. Any discrepancies noticed in the drawing shall be brought to the notice of the Landscape Architect & Architect immediately.
10. Mock work shall be prepared on site for all landscape works and approval of Landscape Architect before taken up for construction.
11. Setting out / Marking should be done on site for all landscape works for approval of Landscape Architect before taken up for construction.

Architects
mta
ARCHITECTURE
INTERIOR DESIGN
ENGINEERING
PROJECT MANAGEMENT
Chennai Tirupur Bangalore

Project:

GURU VILLA
COIMBATORE

Drawing Title

DETAILED LANDSCAPE SCHEME WITH LIGHTING
GROUND LEVEL

Job.no : 1008/24	Drawn - Abarna	North -	CHK BY :
Drg.no: LA-07 R1	Date - 25.03.2026	Scale - 1"0"=18'0"	GPJ

File name :
Z:\1. PROJECTS\Gnanaguru Residence\Drawings\4 - HARD LANDSCAPE CONSTRUCTION DRAWINGS\NON - ISSUED\LA-07 R1,08 R1,09 R1 Detailed Landscape Scheme with lighting, grading plan, settingout plan - Ground level (03.04.2026)

Landscape Architects
RaA
Ravikumar and Associates
LANDSCAPE ARCHITECTURE
ENVIRONMENTAL DESIGN
MASTER PLANNING
14, NORTH AVENUE, SRINAGAR COLONY, SAIDAPET, CHENNAI -15
P +91 44 22353350 / +91 44 22353305 / raa@ravikumarassociates.net / www.ravikumarassociates.net