

SECOND FLOOR PLAN FOR ROOF DESIGN.

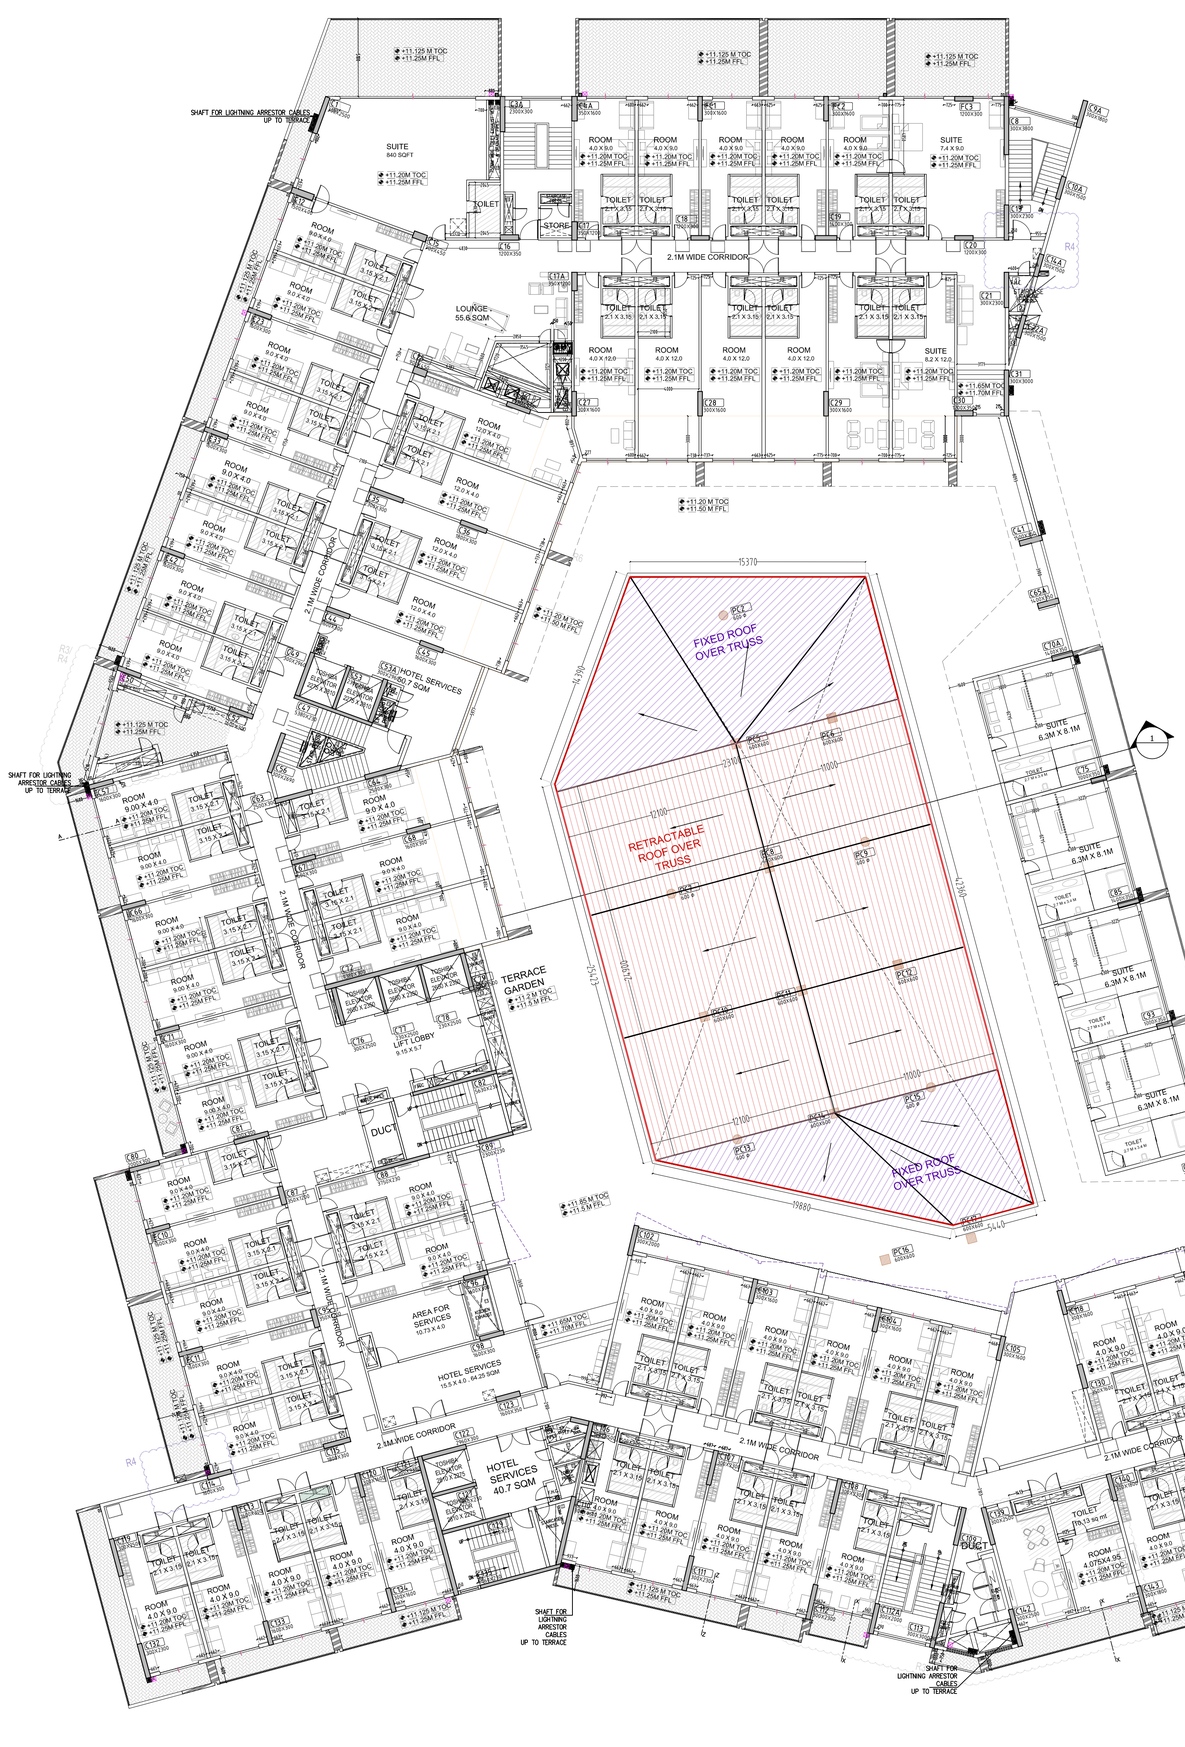

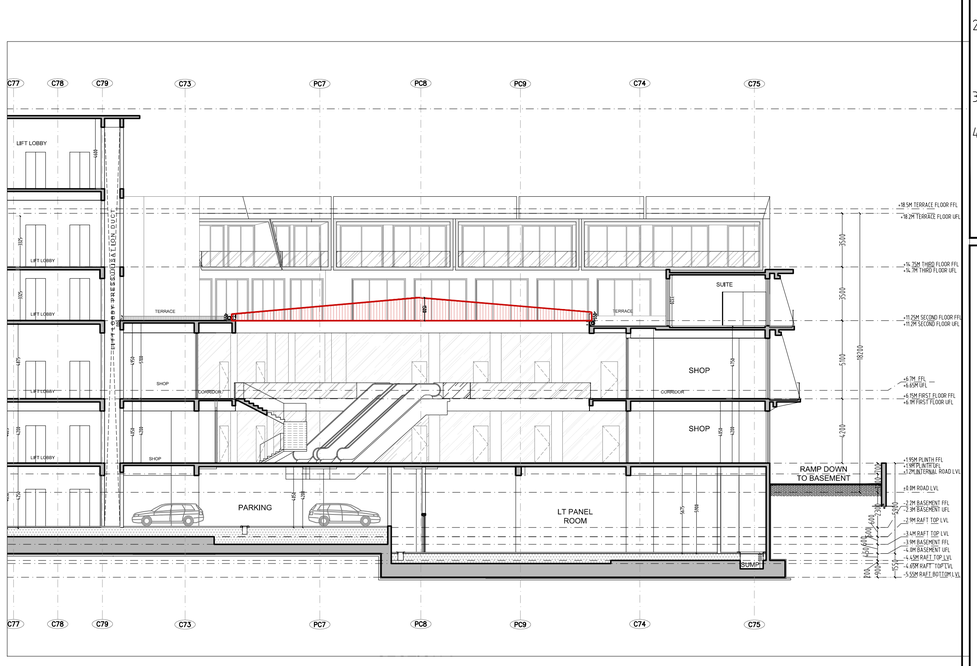

SECTION 1 (THROUGH ATRIUM)
SCALE : 1:200

AREAS :
FIXED ROOF- 334.44 SQM. / 3599.88SQFT.
RETRACTABLE - 576.75 SQM. / 6208.08 SQFT.
TOTAL ROOF AREA - 911.19 SQM. / 9807.96 SQ FT.

NOTE: ALL DIMENSIONS ARE IN MM.

DRAWING NO.

ANJAY PURI ARCHITECTS

NOTES
1. THIS DRAWING IS THE COPYRIGHT OF SANJAY PURI ARCHITECTS PVT. LTD. AND MUST NOT BE RETAINED OR COPIED WITHOUT THE PERMISSION OF THE ABOVE CONSULTANTS.
2. DO NOT SCALE FROM THE DRAWINGS. ALL DIMENSIONS ARE IN MILLIMETRES AND LEVELS IN METRES UNLESS OTHERWISE NOTED.
3. ALL DIMENSIONS TO BE VERIFIED ON SITE AND APPROVED BY THE ENGINEER.
4. THIS DRAWING SHOULD BE READ IN CONJUNCTION WITH OTHER RELEVANT ARCHITECTURAL, STRUCTURAL, MECHANICAL, ELECTRICAL AND CIVIL DRAWINGS AND ALL RELEVANT SECTIONS OF THE STRCUTURAL AND SERVICES DWGS

KEY PLAN

REV.	DESCRIPTION	DATE	REV. BY

NORTH N

SCALE 1:200 A1

PROJECT NUMBER	NS-HO-03
CLIENT	CIE
PROJECT NAME, LOCATION	LEGEND RESORTS SRINAGAR
DATE	10-02-2022
CHECKED BY:	
DRAWN BY:	
DRAWING NAME	SECOND FLOOR PLAN .
DRAWING NO.	
REVISION	
DRAWING STATUS	

sanjay puri architects ltd. 20 famous studio lane off dr. e moses road mahalakshmi mumbai - 400011 t: +91-22-2496-5840 / 41 / 42 / 43 f: +91-22-2496-5896 e: snstudio@sanjaypuriin | i: www.sanjaypuriarchitects.com