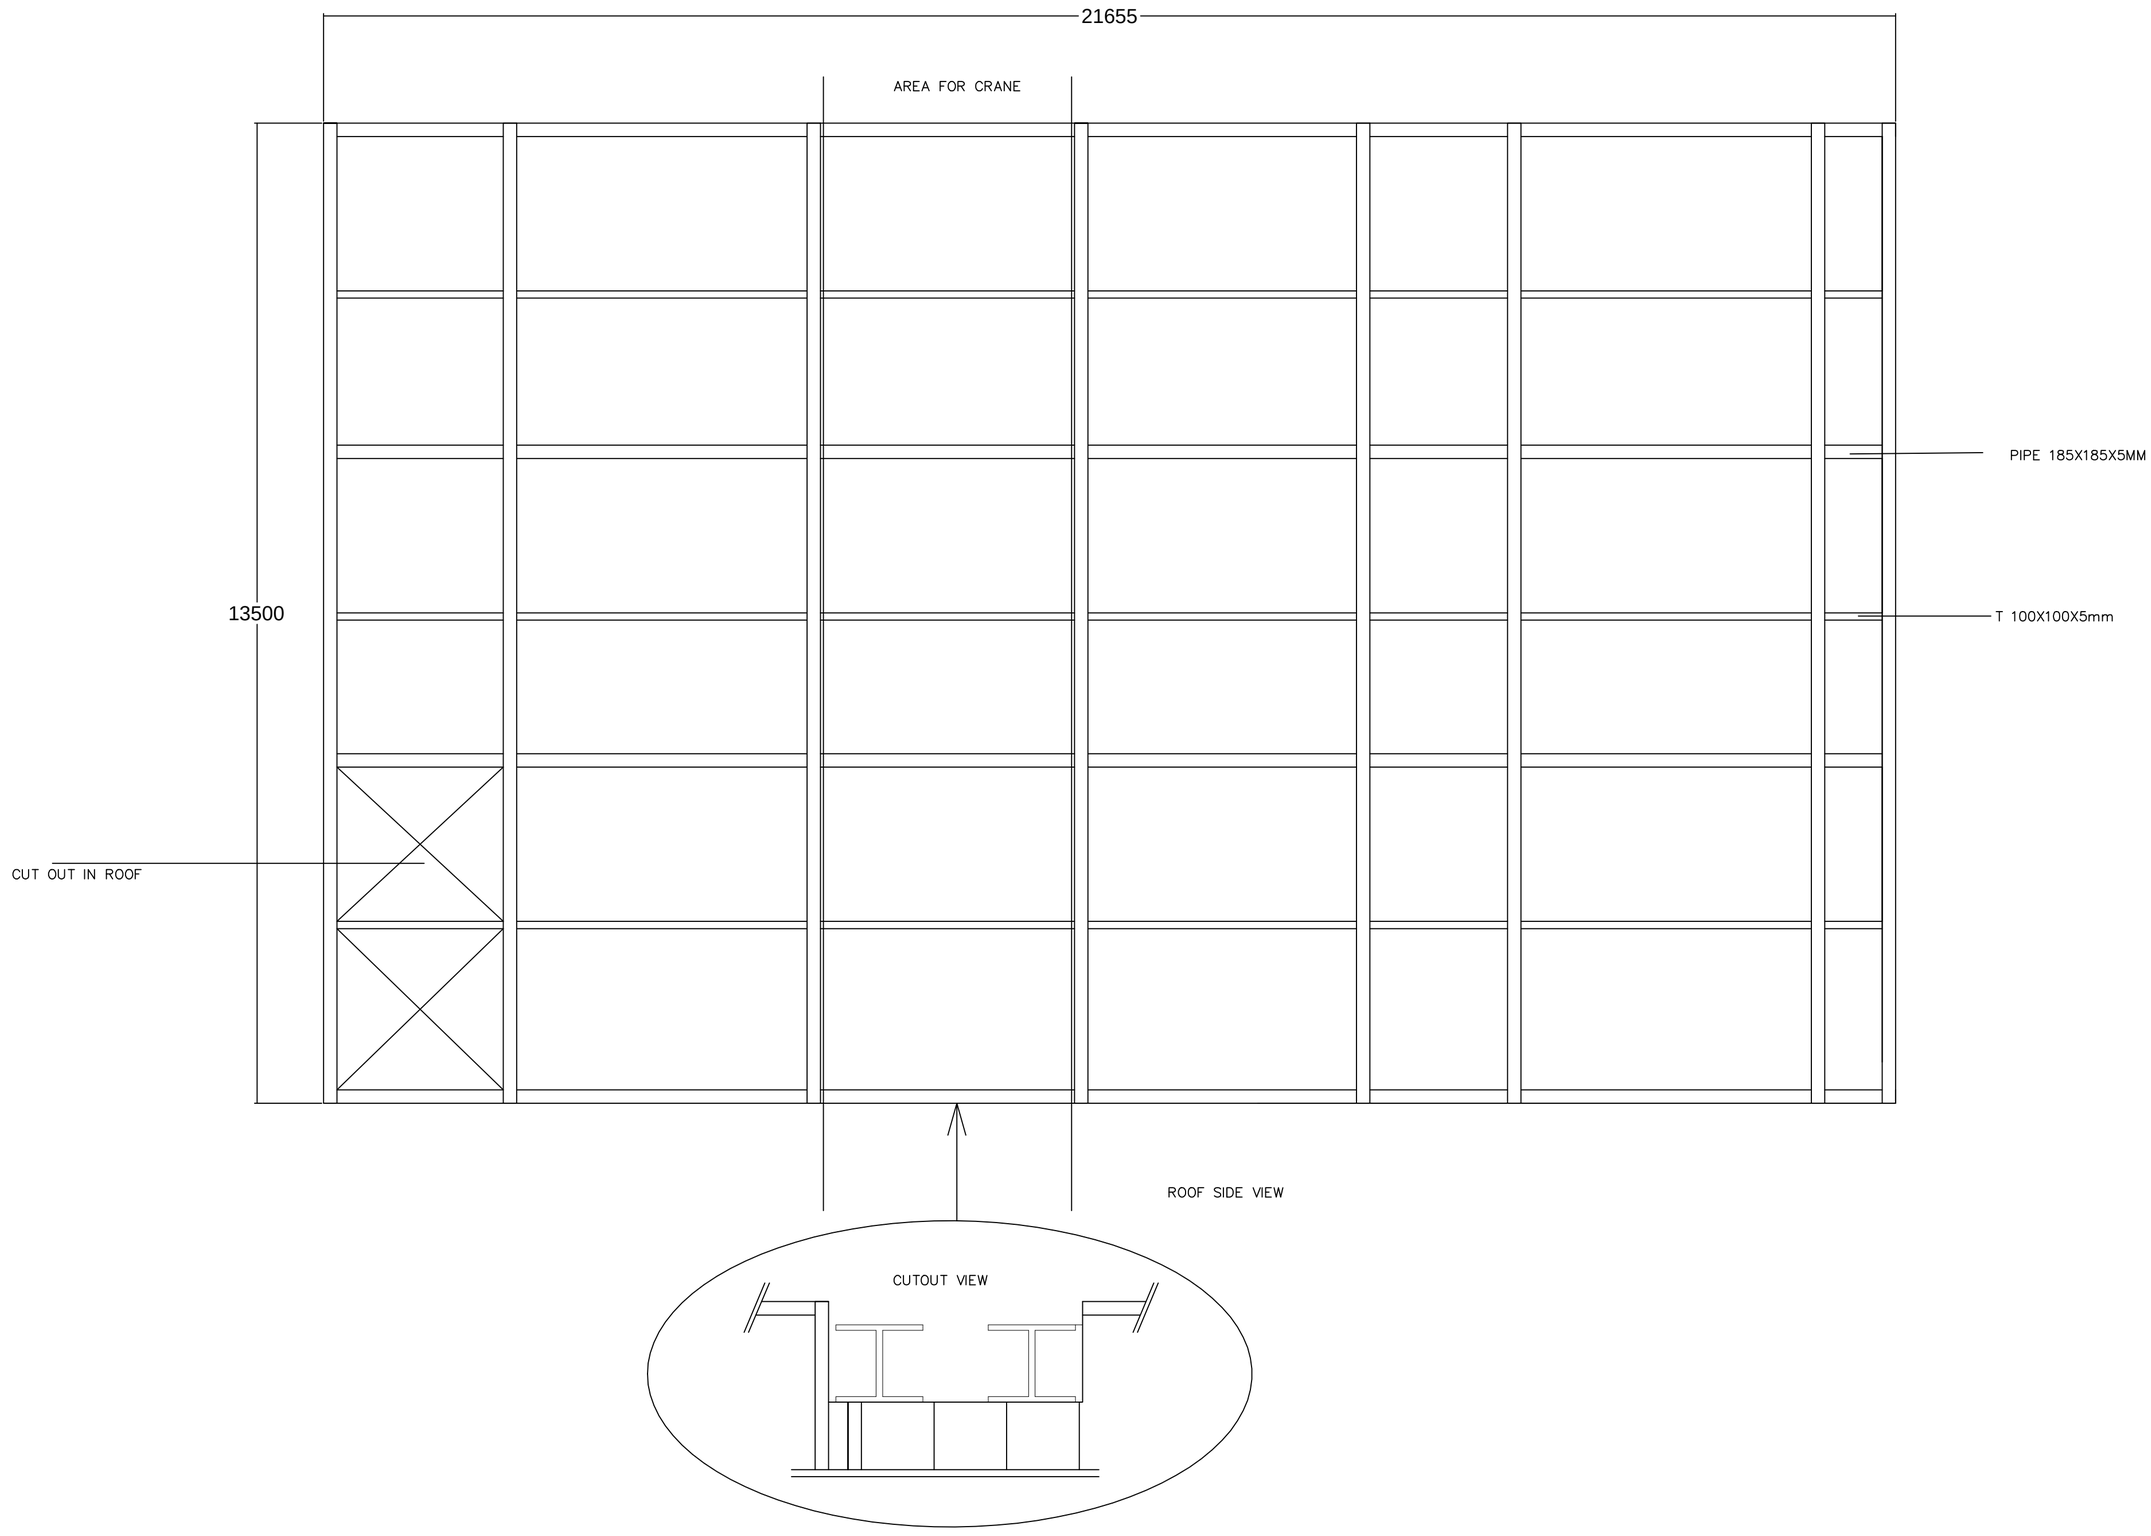
21655
AREA FOR CRANE
13500
PIPE 185X185X5MM
T 100X100X5mm
CUT OUT IN ROOF
ROOF SIDE VIEW
CUTOUT VIEW