

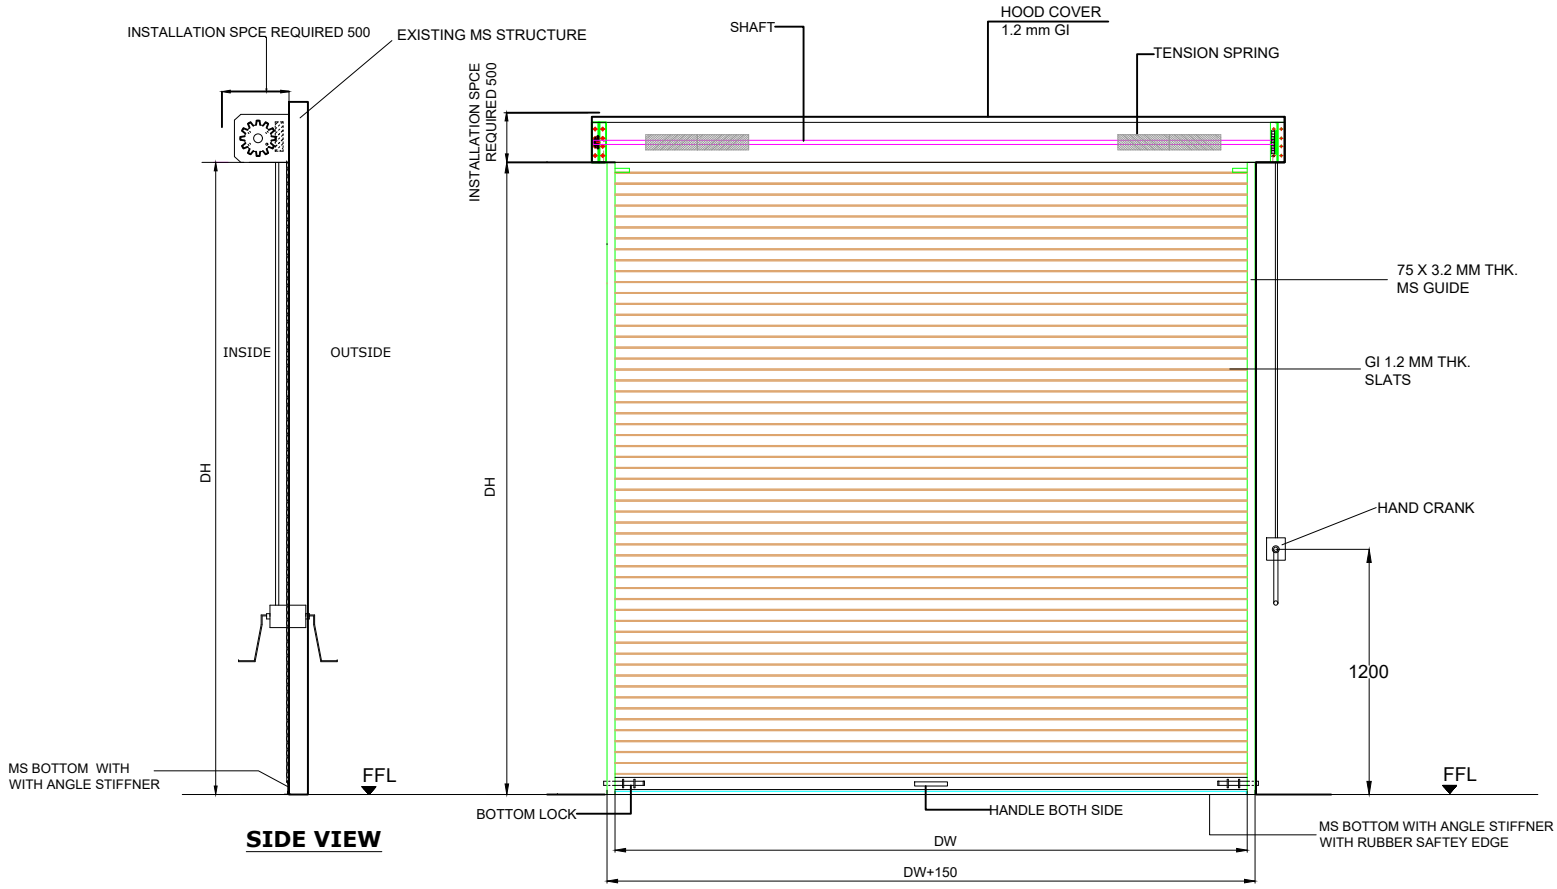


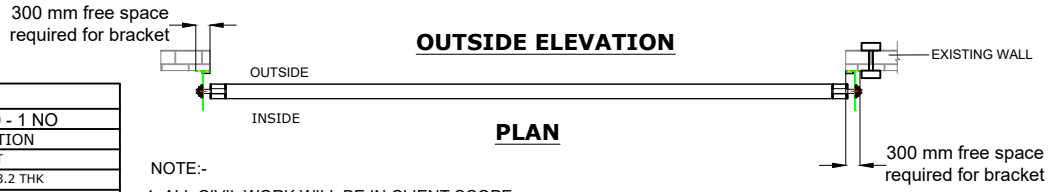

OUTSIDE ELEVATION


PLAN

Curve Type MS Shutter SLATS

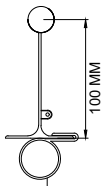

M.S. BOTTOM RAIL PROFILE 2MM

HEAVY RUBBER GAS KIT

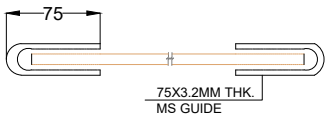

TECHNICAL SPECIFICATIONS		
SHUTTER SIZE - DW 4000 x DH 4000 - 1 NO		
SR NO	DESCRIPTION	SPECIFICATION
1.	SOLID SLAT & QTY	1.2 mm THK GI. SLAT
2.	M.S.GUIDE TYPE & SIZE	U GUIDE OF 75X35X3.2 THK
3.	HOOD COVER 1.2 mm GI	1/SHUTTER
4.	BOTTOM	MS BOTTOM 2 mm THK WITH ANGLE STIFFNER WITH RUBBER SAFTEY EDGE
5.	HAND CRANK	CONSIDERED
6.	HAND CRANK	RH SIDE
7.	SHUTTER MTG LOCATION	INSIDE
8.	SHUTTER MOUNTING BASE	RCC WALL (IN CLIENT SCOPE)
9.	APPROVED RAL SHADE	AS CLIENT APPROVED RAL 9001 : Cream

NOTE:-

1. ALL CIVIL WORK WILL BE IN CLIENT SCOPE.
2. SURFACE FINISH: POWDER COATING OF APPROVED RAL 9001 : Cream.
3. MOUNTING: MS STRUCTURE
4. GALVANIZATION SHALL BE MIN 230g/Sqm
5. ROLLING SHUTTER SHALL WITHSTAND A BASIC WIND SPEED OF 50 m/s

TOLERANCE - ±10mm

REV.NO	REVISION	DATE	REVISED BY
2.	CLEAR HEIGHT 4000 WAS 3500 BEFORE & QTY CHANGED TO 1 NO	20/07/2023	NIRMALA
1.	MS GUIDE THICKNESS HAS BEEN CHANGED FROM 2MM TO 3.2	14/07/2023	SUJATA

CLEAR WIDTH (DW)	CLEAR HEIGHT (DH)	QTY
4000	4000	1 NO

This drawing & designing is the property of NIHVA TECHNOLOGIES. Not to be sold or copied to any other concern.

TITLE :-
GEAR OPERATED ROLLING SHUTTER

NIHVA
NIHVA TECHNOLOGIES PVT. LTD.

	NAME	DATE
DRAWN	SUJATA	06/07/2023
CHECK		
APPROVAL		

CLIENT - RKM Premier Constructions Pvt Ltd
PROJECT - Rolling shutter
SITE -Kanpur
DWG. NO. : NIHVA/23-24/CLT/0142 REV-02
If any queries contact : design1@nihva.com
SCALE: NTS WT: SHEET: 01 OF 01
ALL DIMENSION ARE IN mm