
LOCATION AREA :- SEZ 1 C - FIRST FLOOR- ENTRY

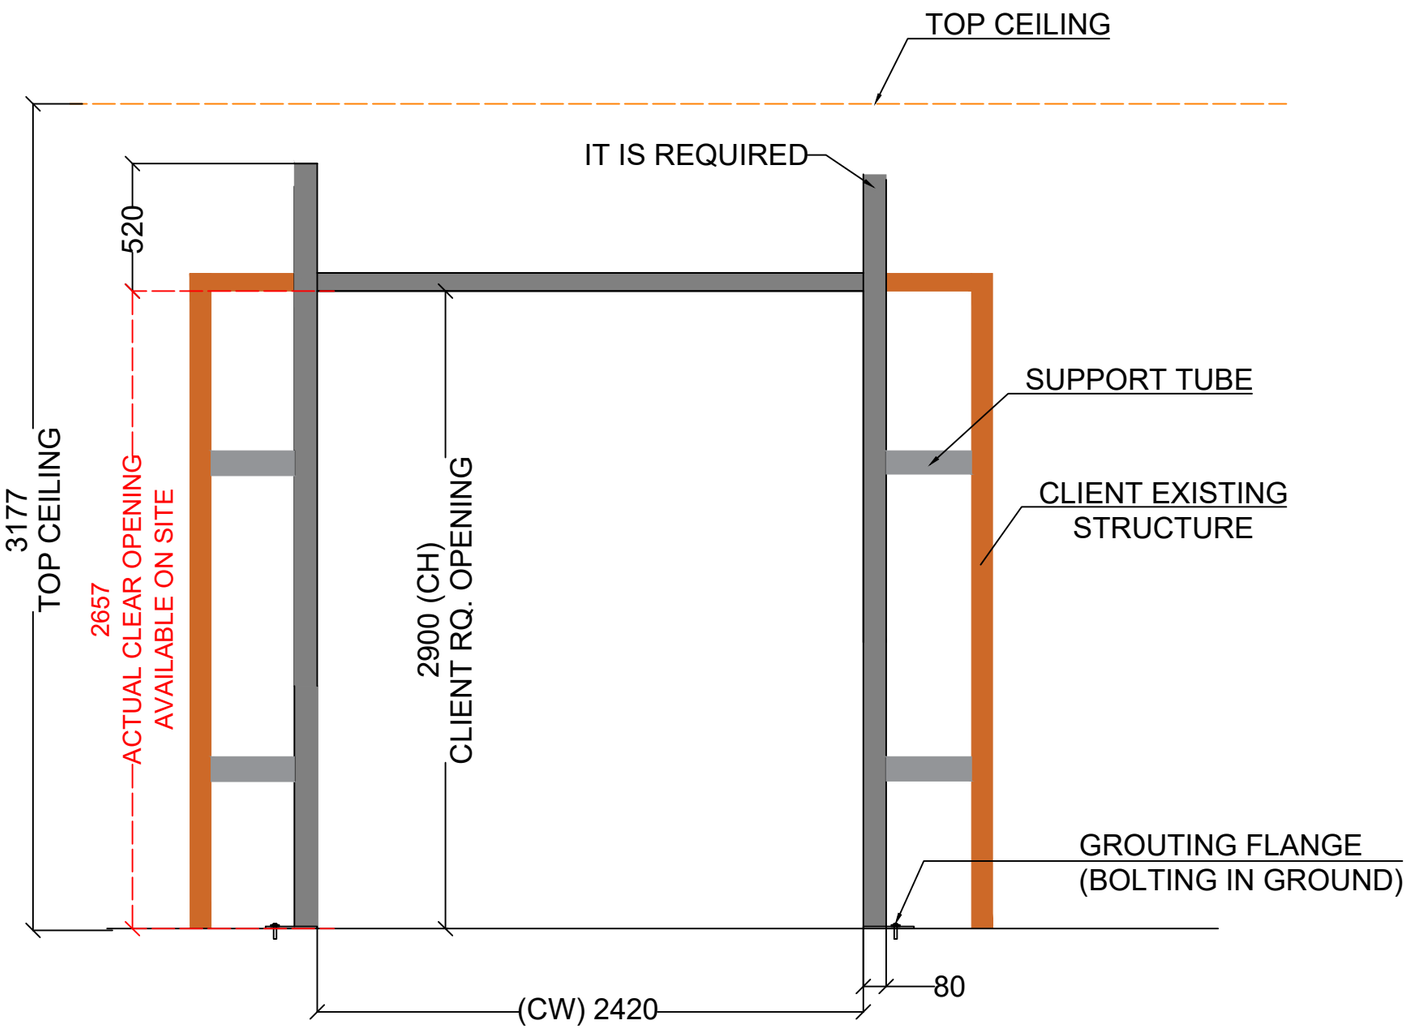

M.S. STRUCTURE DETAILS

Clear Width (CW)	Clear Height (CH)	QTY
2420	**2900**	01

NOTE :-

1. ALL DIMENSIONS ARE IN MM
2. THIS DRAWING IS SOLELY MEANT TO BE UNDERSTOOD.
3. REQUIRED HEIGHT & ACTUAL HEIGHT PLEASE CONFIRM BY CLIENT

This drawing & design is the property of NIHVA TECHNOLOGIES. Not to be sold or copied to any other concern.

TITLE:- HIGH SPEED DOOR STRUCTURE DRAWING			
	NAME	SIGN	DATE
DRAWN	S.J		14.11.2024
CHECK	S.W.		14.11.2024
APPRD.	V.T		14.11.2024
If any queries contact : projectsupport@nihva.com			
ALL DIMENSION ARE IN mm			

NIHVA TECHNOLOGIES PVT. LTD.
NIHVA TECHNOLOGIES PVT. LTD. PUNE
Tel : 020 66304033
Email:- info@nihva.com
Website:- www.nihva.com

CLIENT - SERUM INSTITUTE OF INDIA PVT.LTD			
PROJECT - HIGH SPEED DOOR ST.			
FORMAT NO - NIHVA-DD-F-03			
DWG. NO. : NIHVA/24-25/SM/24100201	REV- R00		
SCALE: NTS	WT:	SHEET:	