


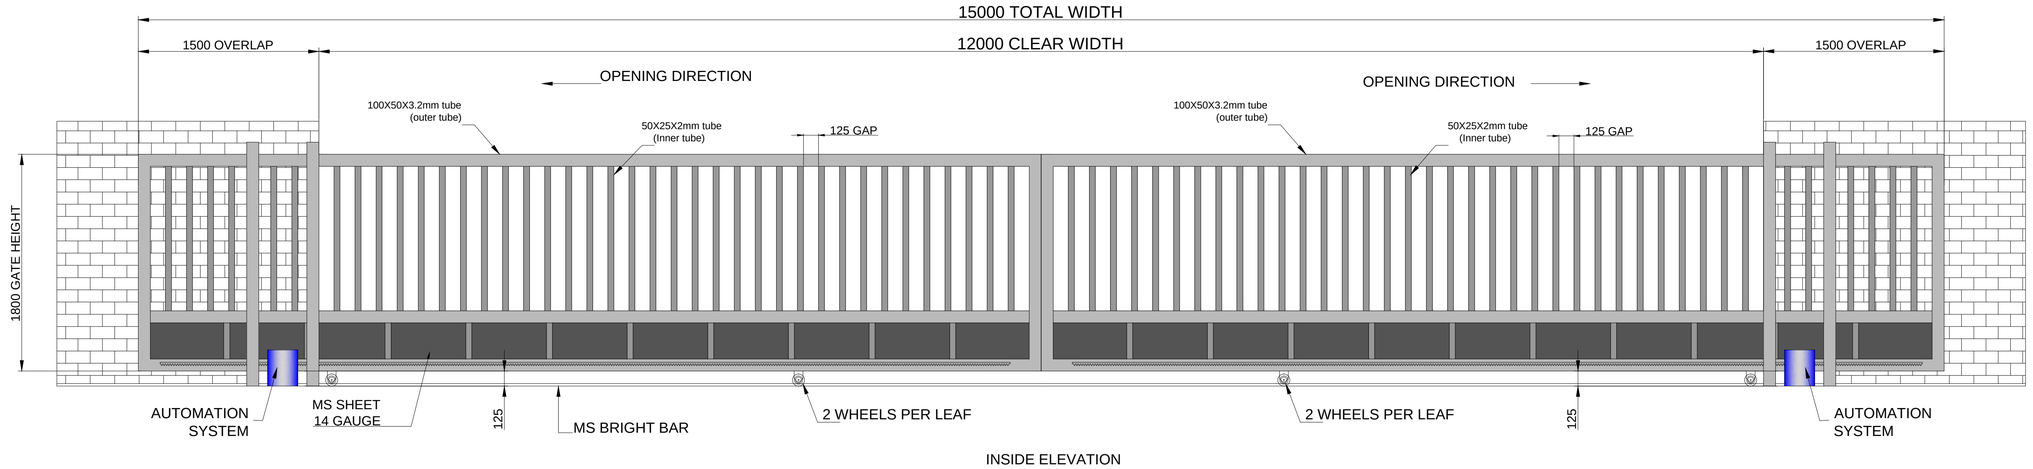


INSIDE ELEVATION

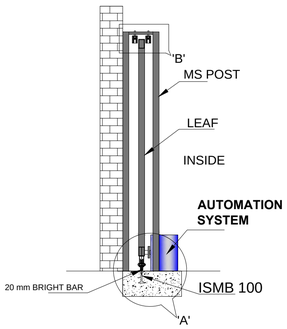


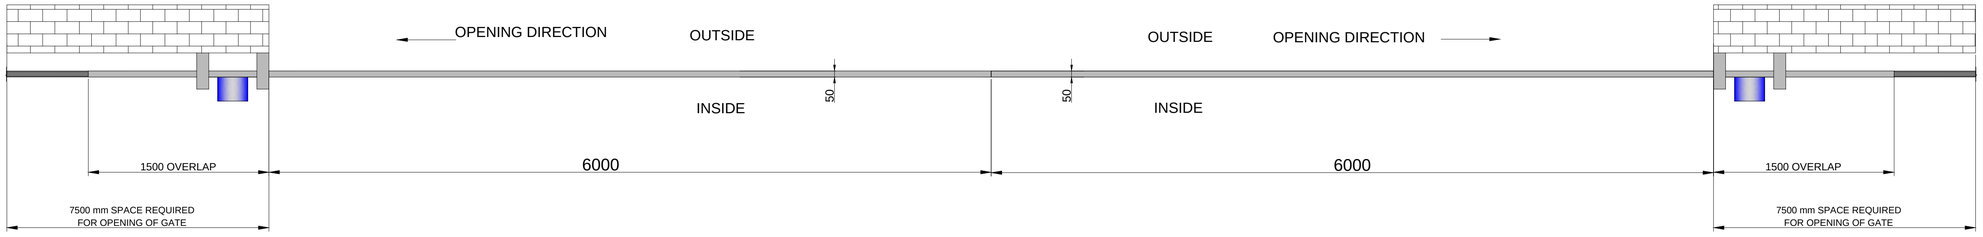

PLAN

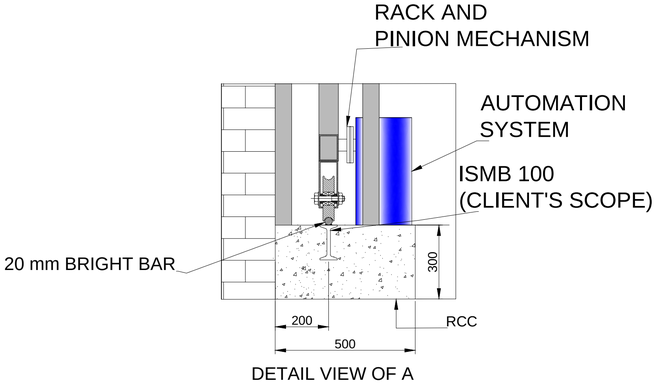

DETAIL VIEW OF A

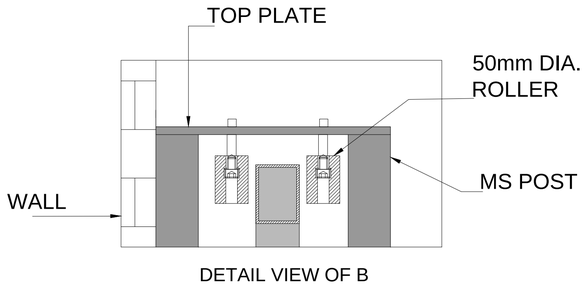

DETAIL VIEW OF B

TOLERANCE- ±10mm

SR NO	TUBE SPECIFICATION	
1	100X50X3.2mm	OUTER FRAME
2	50X25X2mm	INNER PATTERN
3	100X50X3.2mm	FOR MS POST

TOTAL NO OF POST ARE 4 + 4

NOTE-
1. ALL REQUIRED CIVIL WORK WILL BE IN CLIENTS SCOPE.
2. ONE COAT OF RED OXIDE & TWO COAT OF APPROVED RAL SHADE WILL BE GIVEN TO THE GATE.

CLEAR WIDTH	CLEAR HEIGHT	QUANTITY
12000mm	1800mm	1 NOS

This drawing & design is the property of NIHVA TECHNOLOGIES. Not to be sold or copied to any other concern.

TITLE
AUTOMATIC DOUBLE LEAF SLIDING GATE

	SIGN	DATE
DRAWN	SURAJ	01/09/17
CHECK	SAGAR P.	01/09/17
REV.		
APPROVAL	SHEKHAR	01/09/17

If any queries contact : projects@nihva.com

ALL DIMENSION ARE IN mm

NIHVA TECHNOLOGIES PVT. LTD.
NIHVA TECHNOLOGIES PVT. LTD. PUNE
Tel : 020 66304033
Email:- info@nihva.com
Website:- www.nihva.com

CLIENT - ERICSSON INDIA PVT. LTD.
PROJECT -
SITE LOCATION -CHAKAN,PUNE
DWG. NO. : NIHVA/17-18/0194
SCALE: NTS | WT: | SHEET: 01 OF 01