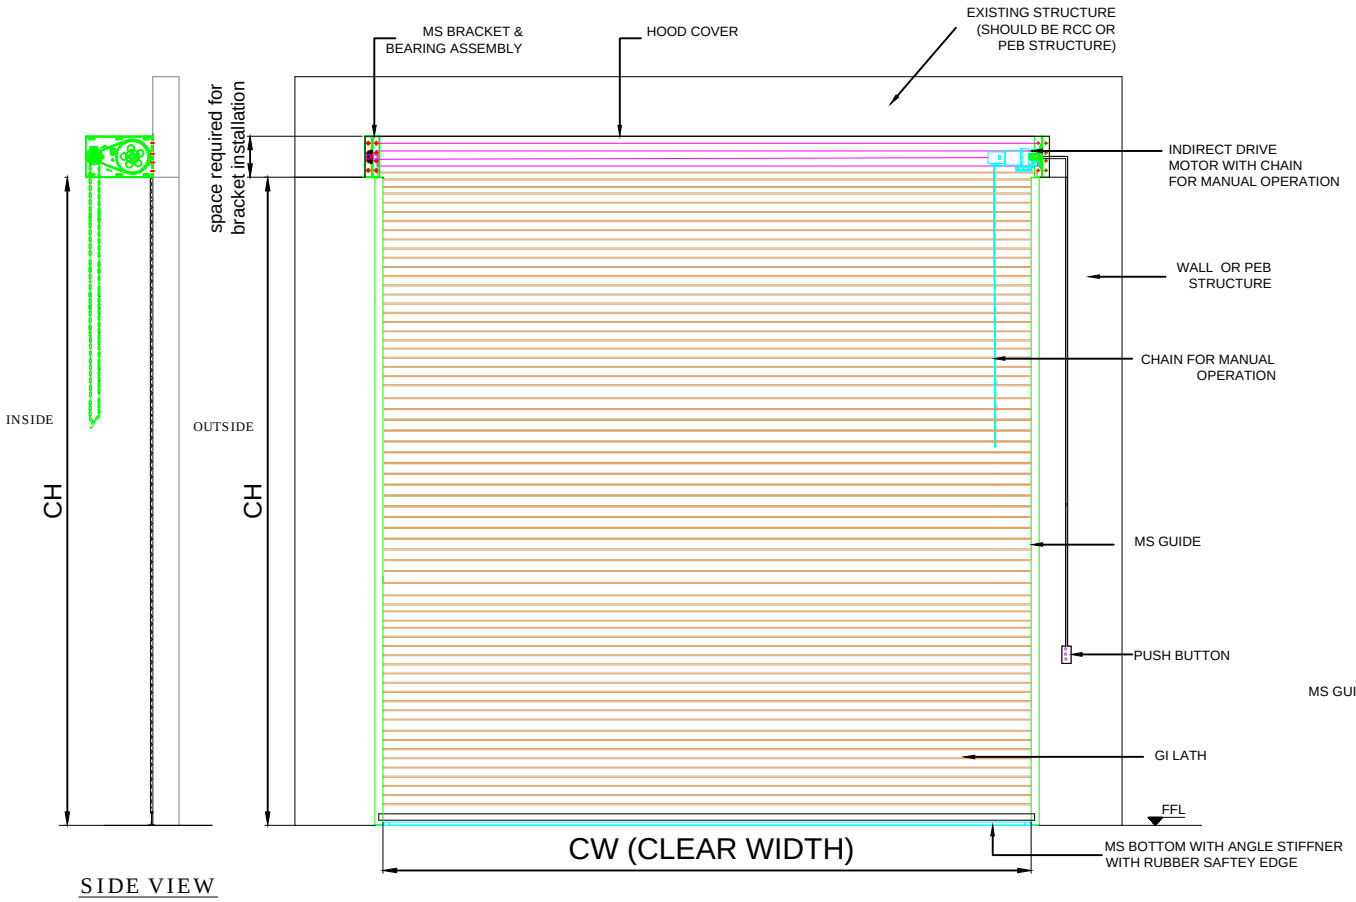
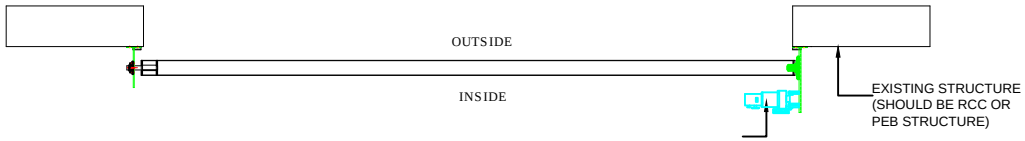
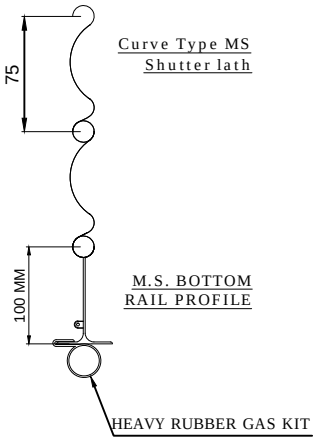


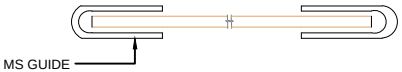

SIDE VIEW

INSIDE ELEVATION




PLAN




| CLEAR WIDTH (CW) | CLEAR HEIGHT (CH) | QUANTITY |
|---|---|---|
| 2000 | 2100 | 1 |

DIMENSION :

| CLEAR WIDTH | CLEAR HEIGHT | QUANTITY |
|---|---|---|
| 2000 mm | 2100 mm | 01 NOS. |

MATERIAL :

THICKNESS :

NOTE:
1.REQUIRED STRUCTURE FOR SHUTTER SHALL BE IN CLIENT SCOPE.

2.ONE COAT OF RED OXIDE PRIMER WILL BE GIVEN TO NON GI COMPONENT OF SHUTTER.

3.IN CASE OF 6X6 METER OR ABOVE ROLLING SHUTTER GUIDES SHOULD BE 150mm.

4.IN CASE OF SHUTTER WIDTH IS MORE THAN 6METER, IT IS PREFERABLE TO USE / INCORPORATE PERFORATED SHEET OR GRILL IN SHUTTER.

NIHVA TECHNOLOGIES PVT. LTD.
NIHVA TECHNOLOGIES PVT. LTD. PUNE
Email:- info@nihva.com
Website:- www.nihva.com

TITLE:

MOTORIZED ROLLING SHUTTER

CLIENT'S APPROVAL :

CLIENT - Infinity switch technologies pvt. ltd

PROJECT - Infinity switch technologies pvt. ltd

SITE LOCATION -PUNE.

DWG. NO. : NIHVA/17-18/0064

| SCALE: NTS | WT: | SHEET:1 OF 1 |
|---|---|---|

| DRAWN BY: SURAJ | DATE: 09-05-2017 |
|---|---|
| CHECK : SAGAR P | DATE: 09-05-2017 |
| APPROVED BY- R.K | DATE: 09-05-2017 |

If any queries contact : projects@nihva.com

NOTE: ALL DIMENSIONS ARE IN mm

THIS DRAWING & DESIGN IS THE PROPERTY OF NIHVA TECHNOLOGIES. NOT TO BE SOLD OR COPY TO ANY OTHER CONCERN.