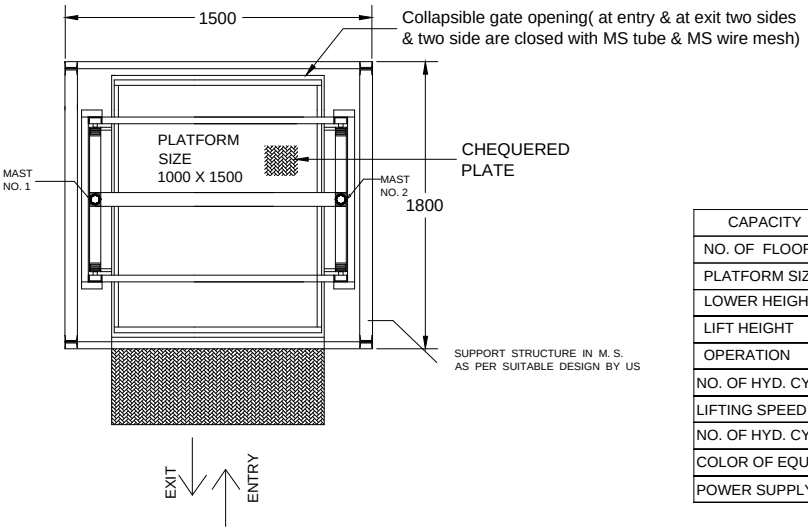

PLAN

CAPACITY	1000 KGS
NO. OF FLOORS	GROUND + 1 FLOOR
PLATFORM SIZE	1000 mm X 1500 mm
LOWER HEIGHT	200 mm
LIFT HEIGHT	3000 mm
OPERATION	3 HP A. C. POWERPACK
NO. OF HYD. CYLINDERS	2 NOS
LIFTING SPEED	50-60 mm/s
NO. OF HYD. CYLINDERS	2 NOS
COLOR OF EQUIPMENT	GOLDEN YELLOW RAL 1003
POWER SUPPLY	440VAC,3PH,50HZ

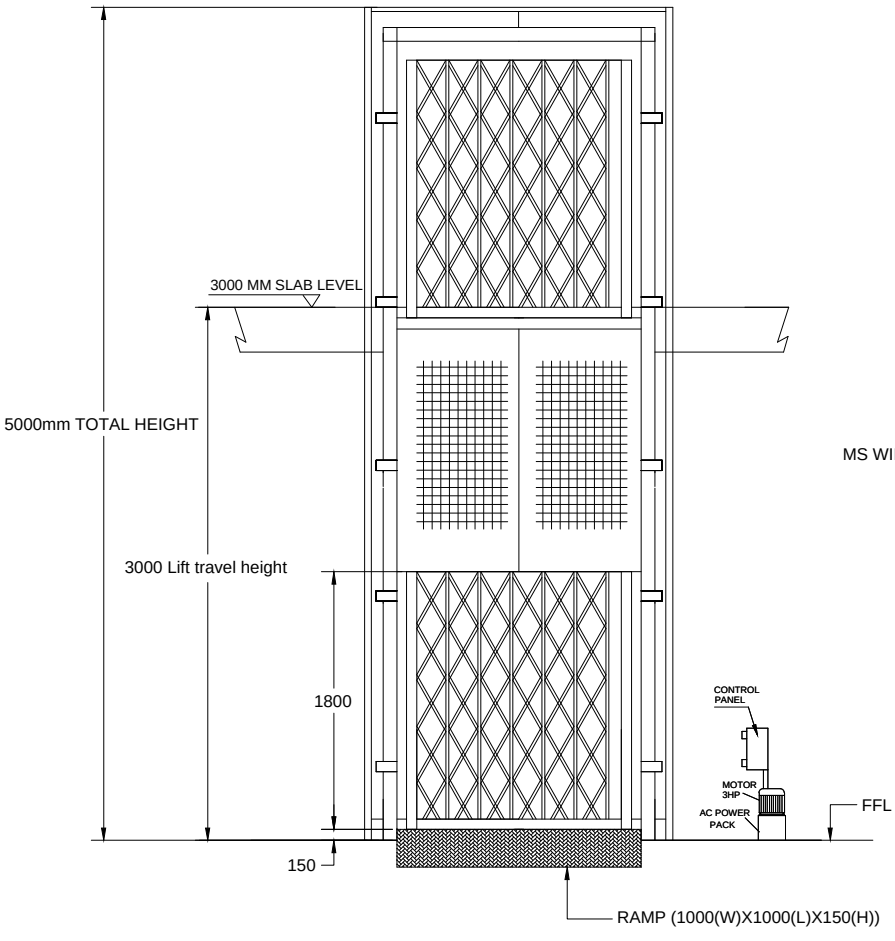

ELEVATION

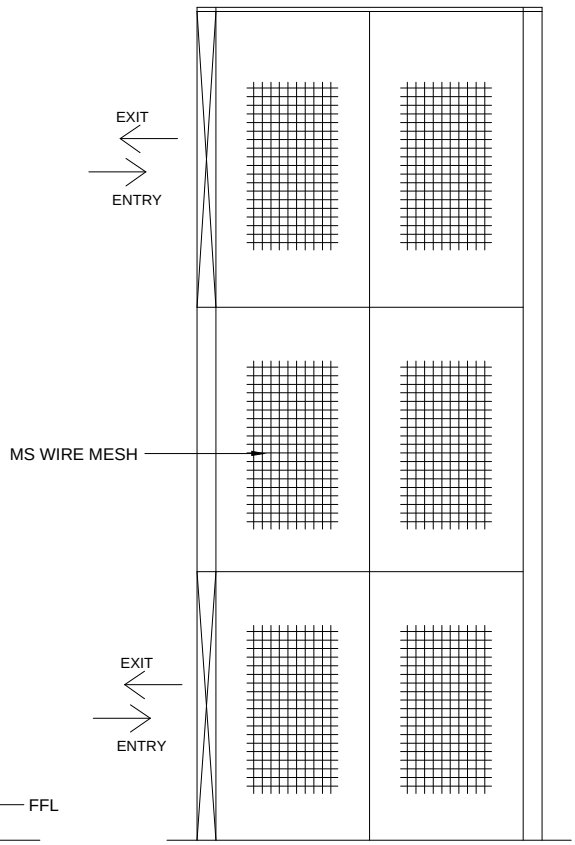

SIDE VIEW

This drawing & design is the property of NIHVA TECHNOLOGIES. Not to be sold or copied to any other concern.

TITLE

GOODS LIFT
G.A. DRG

CLIENT APPROVAL

ALL DIMENSION ARE IN mm

	SIGN	DATE
DRAWN	OMKAR	30/03/17
CHECK	SAGAR P.	30/03/17
REV.		
APPRD.	R.K.	30/03/17
MFG		
Ref. No.		

NIHVA TECHNOLOGIES PVT. LTD.
NIHVA TECHNOLOGIES PVT. LTD. PUNE
Tel : 020 66304033
Email:- info@nihva.com
Website:- www.nihva.com

CLIENT - FERRERO INDIA PVT. LTD.

PROJECT -

SITE - BARAMATI

DWG. NO. - NIHVA/16-17/198/R01

SCALE: NTS | WT: | SHEET: 01 OF 01

If any queries contact : projects@nihva.com