
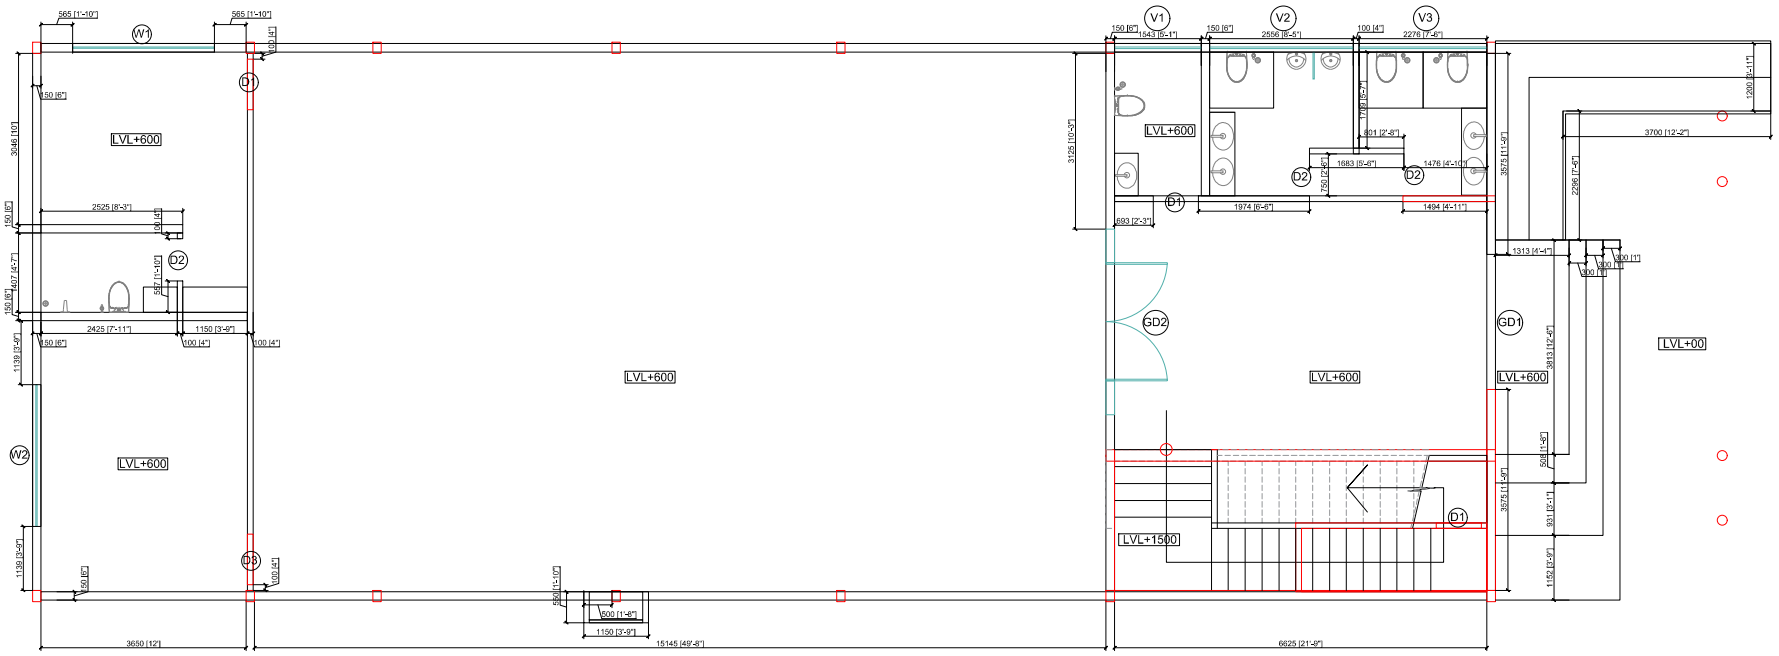


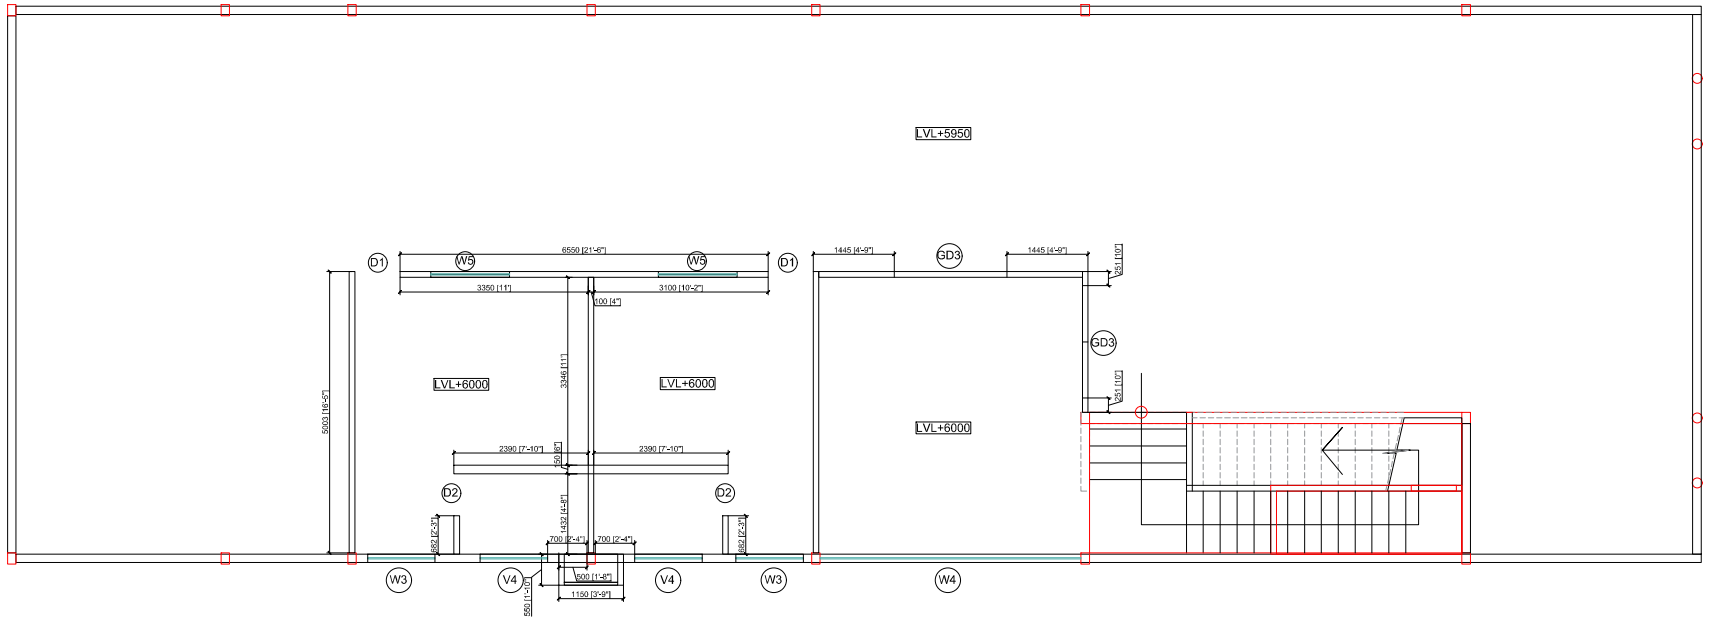

URVI
Architectural Services,
Patna - India
+91 96346 59272
ar.urvija.kriti@gmail.com

PROJECT NUMBER: U-121

PROJECT NAME : REFLECTION BANQUET

General Notes:

ALL DIMENSIONS ARE IN MM (MILLIMETER).

- DRAWING SHALL NOT BE SCALED AND ONLY WRITTEN DIMENSIONS SHALL BE FOLLOWED.
- ALL CENTERLINES ARE FROM THE CENTER OF COLUMN/ WALL AND THE DIMENSIONS GIVEN ARE CENTER LINE DIMENSIONS UNLESS OTHERWISE MENTIONED.
- IN CASE OF ANY DISCREPANCY FOUND IN DRAWINGS AND DETAILS, IT SHALL BE BROUGHT TO THE NOTICE OF THE ARCHITECT, AND RECTIFIED, PRIOR TO ITS EXECUTION.
- THIS DRAWING IS ISSUED STRICTLY WITH AN UNDERSTANDING THAT IT WILL BE USED ONLY FOR THE PURPOSE MENTIONED AND SHALL BE RETURNED AFTER COMPLETION.
- LARGER SCALE DRAWINGS AND DETAILS SUPERSEDE THE SMALLER SCALE DRAWINGS AND DETAILS.
- THIS DRAWING SHALL BE REFERRED ONLY FOR THE PURPOSE MENTIONED IN ITS TITLE (FLOORING PATTERN, FALSE CEILING, SHUTTERING PATTERN, ELECTRICAL, PLUMBING, ETC.)

DRAWING TITLE :

CIVIL LAYOUT

ISSUED / REVISION :

NO.	DATE	REMARKS
1.		
2.		
3.		
4.		
5.		

SCALE :

DRAWING NO. A 112

DRAWN BY:

CHECKED BY: URVIJA KRITI

STAMP SIGN :

DATE : 220105

N