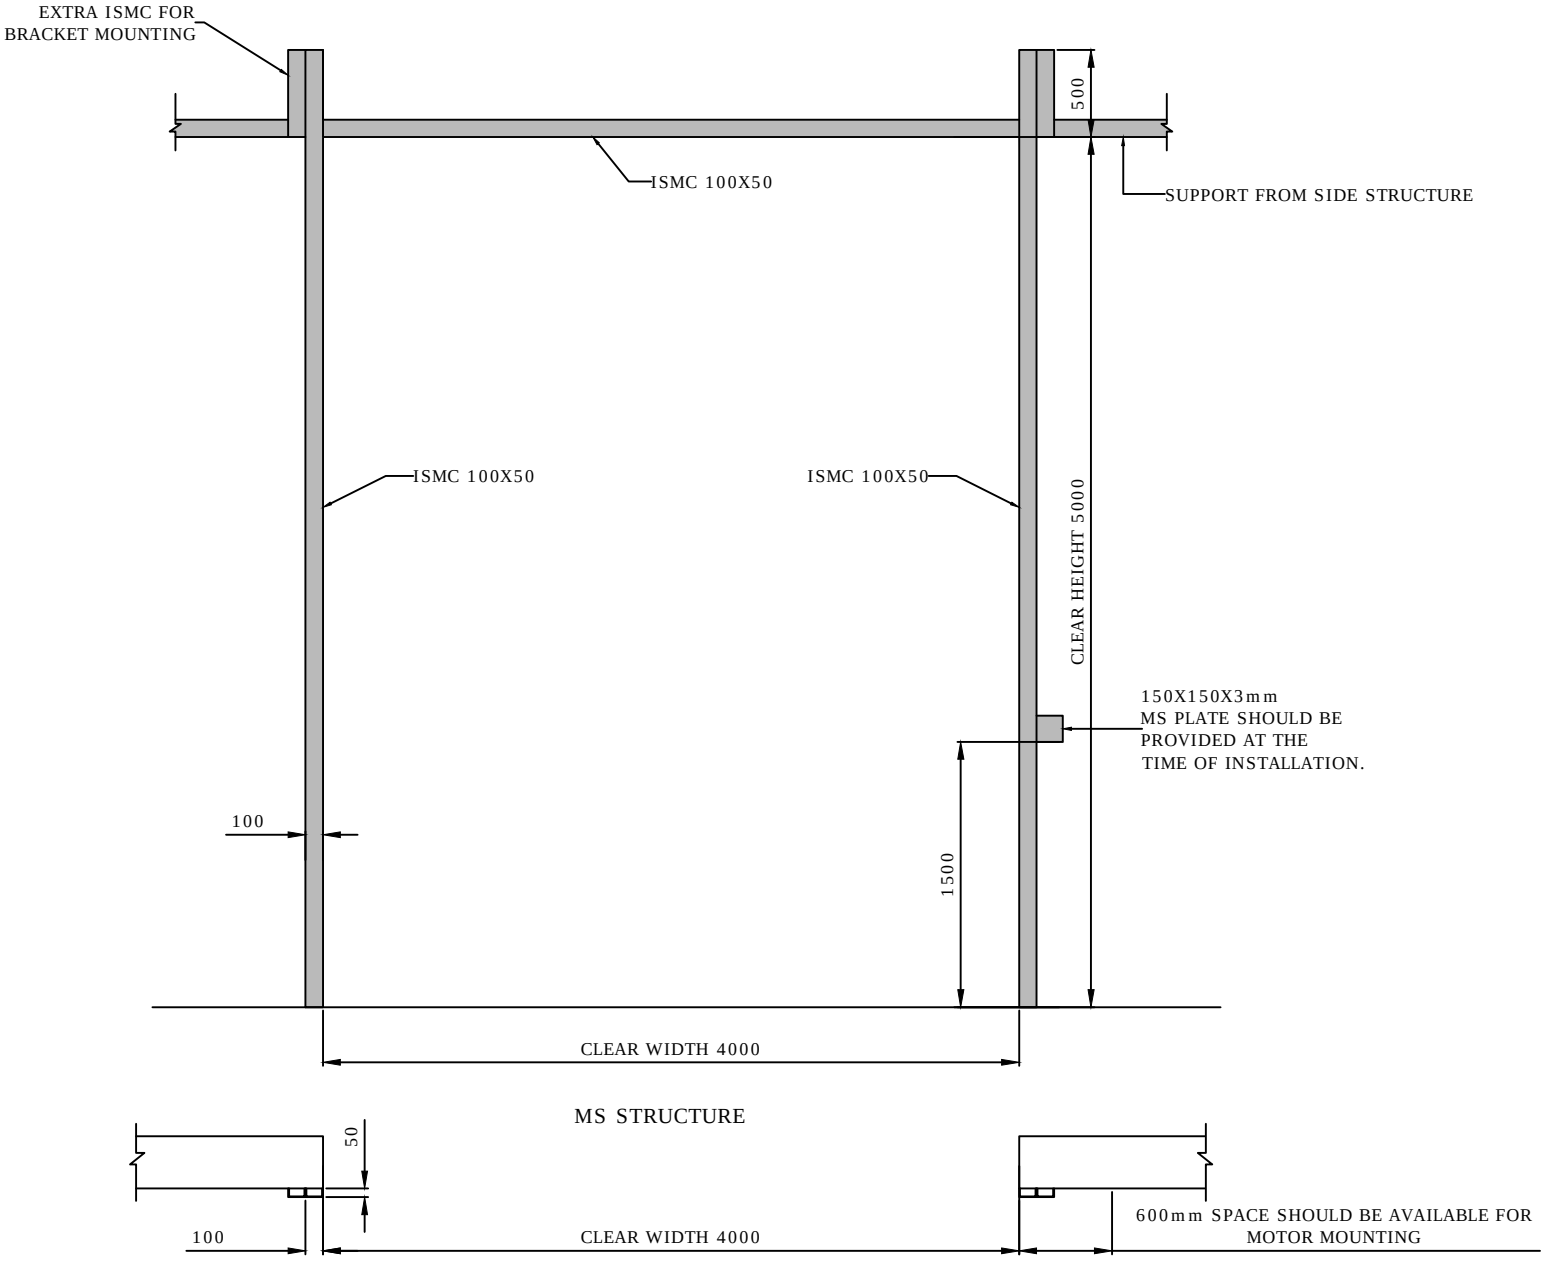

DIMENSION :

CLEAR WIDTH	CLEAR HEIGHT	QUANTITY
4000 mm	5000 mm	03 NOS.

MATERIAL :

THICKNESS :

NIHVA TECHNOLOGIES PVT. LTD.

NIHVA TECHNOLOGY
PVT. LTD. PUNE
Email:- info@nihva.com
Website:- www.nihva.com

TITLE:

STRUCTURE FOR
MOTORIZED ROLLING SHUTTER

CLIENT'S APPROVAL :

CLIENT - SS GHORPADE

PROJECT -

SITE LOCATION -

DWG. NO. : NIHVA/16-17/104

SCALE: NTS	WT:	SHEET:1 OF 1

DRAWN BY: OMKAR DATE: 17-11-2016

CHECK : ANIL DATE: 17-11-2016

If any queries contact : projects@nihva.com

NOTE: ALL DIMENSION ARE IN mm

THIS DRAWING & DESIGNING IS THE PROPERTY OF NIHVA TECHNOLOGIES. NOT BE SOLD OR COPY TO ANY OTHER CONCERN.