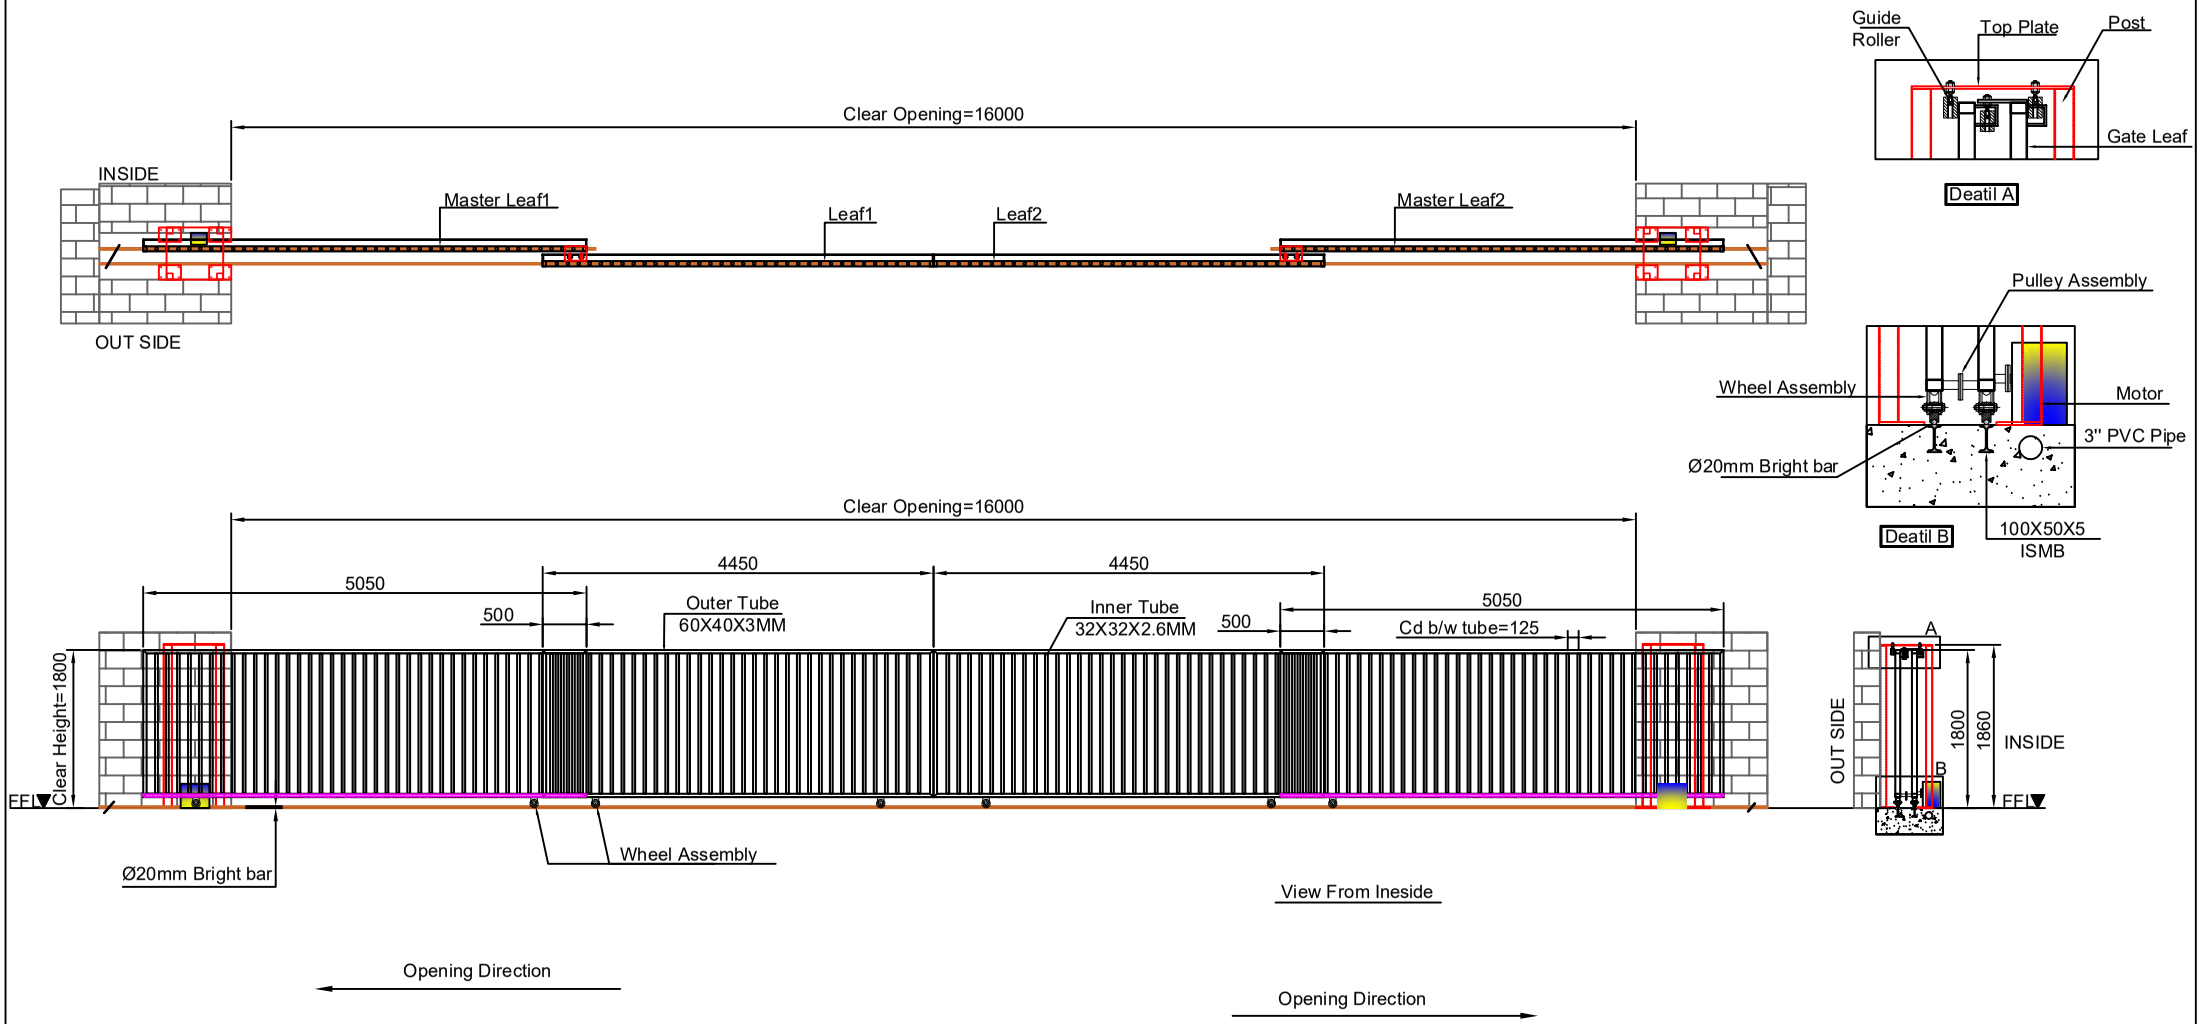


Note:-

1. All Dimension are in MM
2. Required all civil work will be in Client scope
3. Fabrication and Installation Tolerance will be ±20mm
4. Required Parking will be 5200mm both side
5. Gate Color will be Metalic color,shade stone gray(RAL7030)

TECHNICAL SPECS FOR TEL.SLIDING GATE		
SL NO.	SPECIFICATION	
1	OPENING LENGTH	16000MM
2	OPENING HEIGHT	1800MM
3	OUTER TUBE	60X40X3MM
4	INNER TUBE	32X32X2.6MM
5	OPERATION	MOTORIZED

This drawing & design is the property of NIHVA TECHNOLOGIES. Not to be sold or copied to any other concern.

TITLE:- Bi-Parting Tel.Sliding Gate

NIHVA TECHNOLOGIES PVT. LTD.

NIHVA TECHNOLOGIES PVT. LTD. PUNE
Tel : 020 66304033
Email:- info@nihva.com
Website:- www.nihva.com

	NAME	DATE	SIGN
DRAWN	SUJATA	18/06/2022	
CHECK			
APPRD.	M.S	18/06/2022	

If any queries contact : design@nihva.com

ALL DIMENSION ARE IN mm

CLIENT - NAVNEET EDUCATION LTD

LOCATION - PALGHAR

PRODUCT - TEL.SLIDING GATE

DWG NO:-NIHVA/22-23/CLT/0061 REV- 0

SCALE: NTS SCALE:-- 1:1 SHEET: 01 OF 01

Rev No.	Revision	Date	Revised By