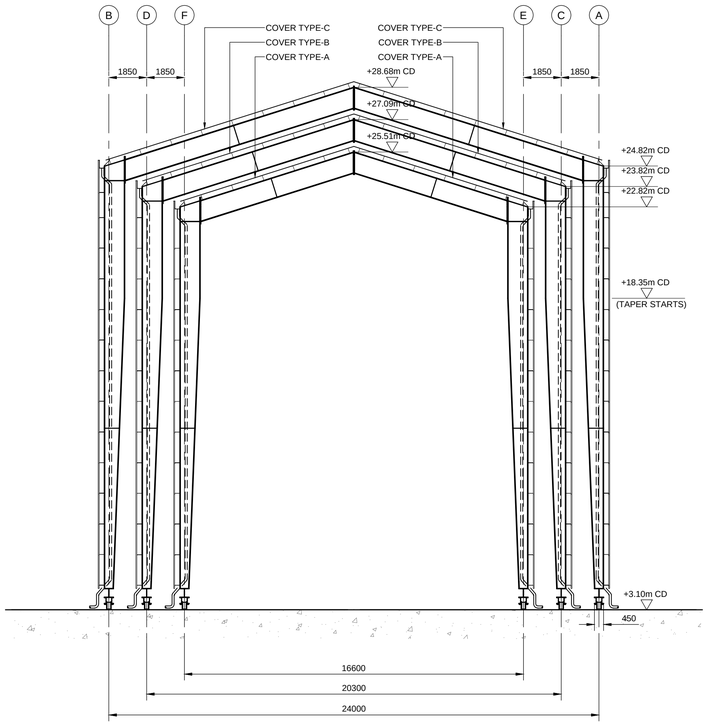
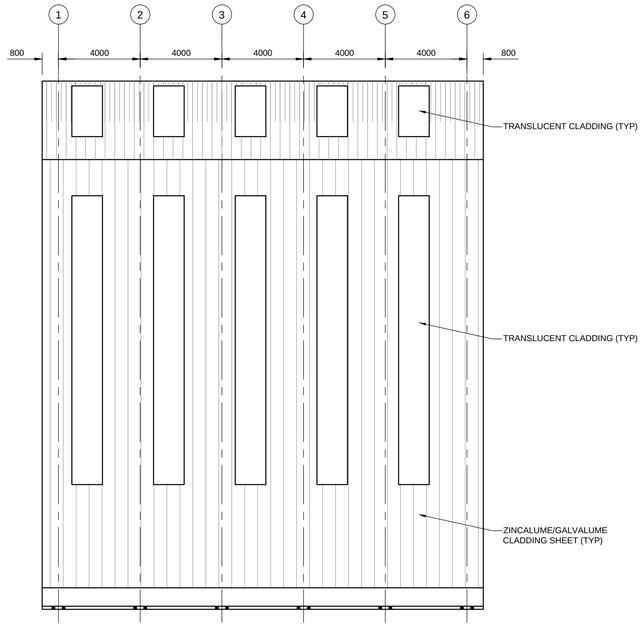
DRG No. RA1202/P4/3701


**DO NOT SCALE**



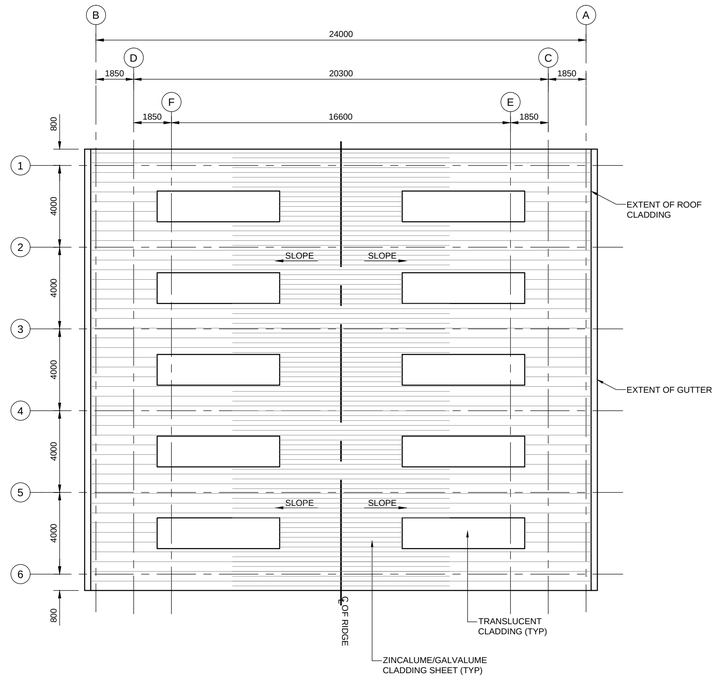

TYPICAL CROSS SECTION
THROUGH BERTH COVERS
SCALE 1:150





BERTH COVER
SIDE ELEVATION (TYPICAL)
SCALE 1:150



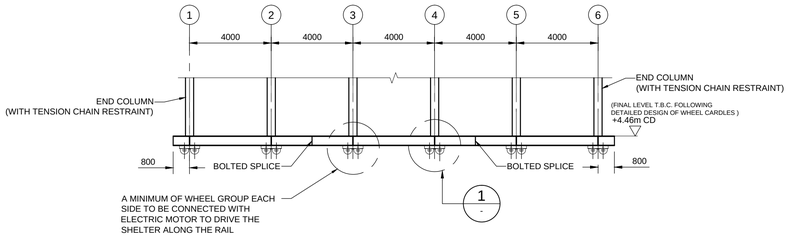

PLAN AT ROOF LEVEL
BERTH COVER (TYPICAL)
SCALE 1:150



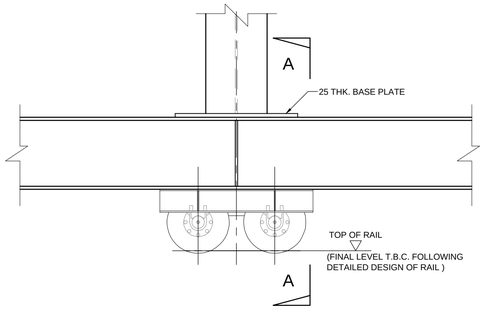
TYPICAL BERTH COVER
ELEVATION AT BASE
SCALE 1:150





DETAIL 1
SCALE 1:20

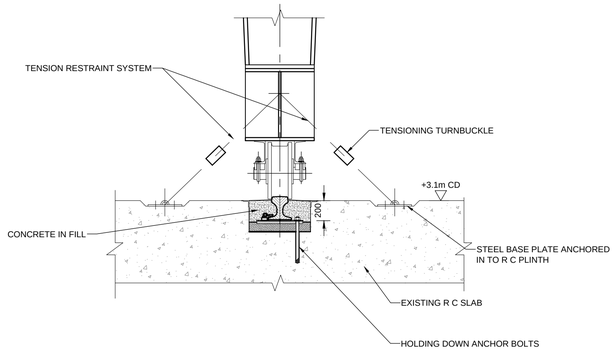


SECTION A-A
TYPICAL BASE DETAIL
SCALE 1:20

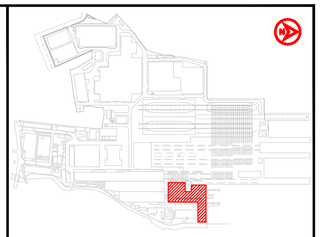© Haskoning UK Ltd.



KEY PLAN

NOTES:

1. ALL DIMENSIONS ARE IN MILLIMETRES UNLESS NOTED OTHERWISE.
2. ALL LEVELS ARE IN METRES UNLESS NOTED OTHERWISE.
3. ALL STEEL TO BE GRADE FE 410WA UNLESS NOTED OTHERWISE.

FOR TENDER

| REV | DATE | DESCRIPTION | BY | CHK | APP |
|---|---|---|---|---|---|
| T10 | MAY 16 | FOR TENDER | YSK | KK | SRD |

REVISIONS

CLIENT
GOA SHIPYARD LIMITED

PROJECT
GOA SHIPYARD
MODERNISATION PLAN
PHASE - 4

TITLE
MOVABLE SHELTER GA

HASKONINGDHV NEDERLAND B.V
Royal HaskoningDHV
Enhancing Society Together
502-505, 5th Floor, Platinum Techno Park
Plot 17 & 18, Sector 30 A, Vashi
Navi Mumbai - 400 703, INDIA
Tel +91 (0) 22 61395000
Email info.india@rhdhv.com
www.royalhaskoningdhv.com

| DRAWN | CHECKED | PASSED |
|---|---|---|
| YSK | KK | SRD |
| DATE | CLIENT'S REF. | |
| APR'16 | RA1202 | |
| SCALE AT A1 | AUTOCAD REF. | |
| AS SHOWN | RA1202 | |

DRAWING No. RA1202/P4/3701

REVISION T10