

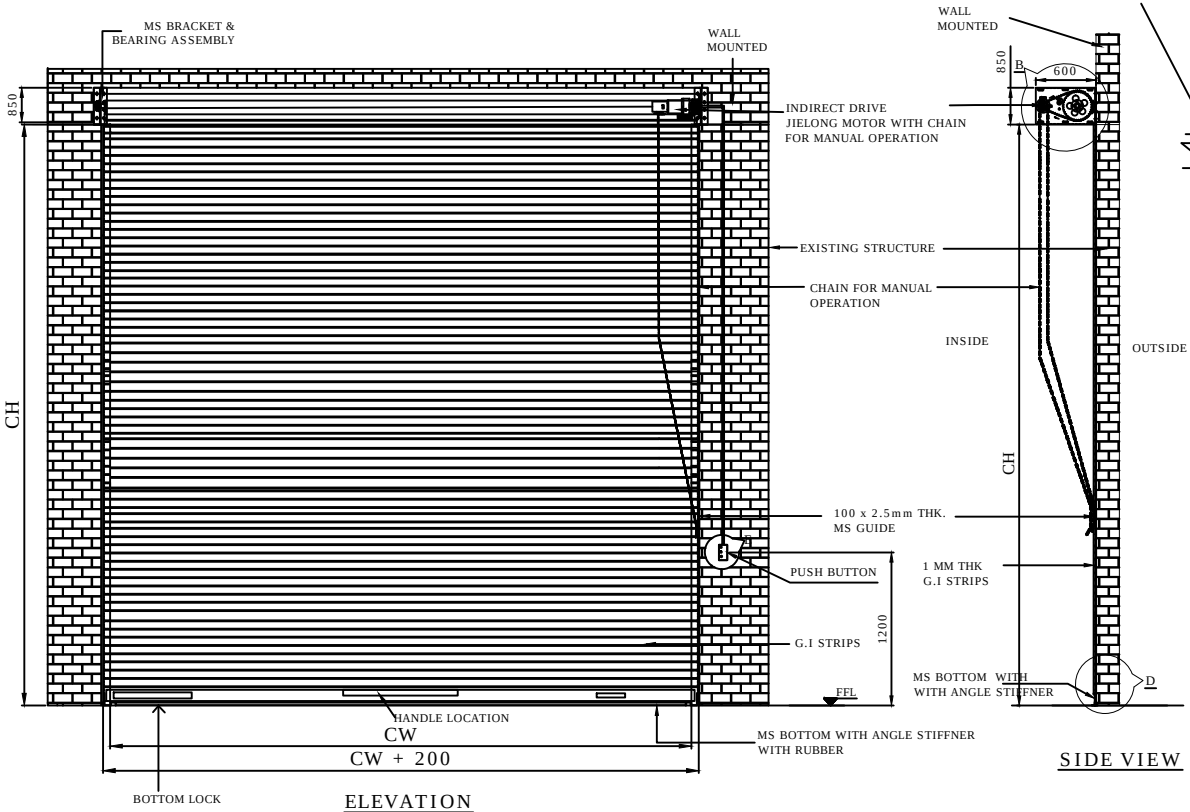


ELEVATION


SIDE VIEW

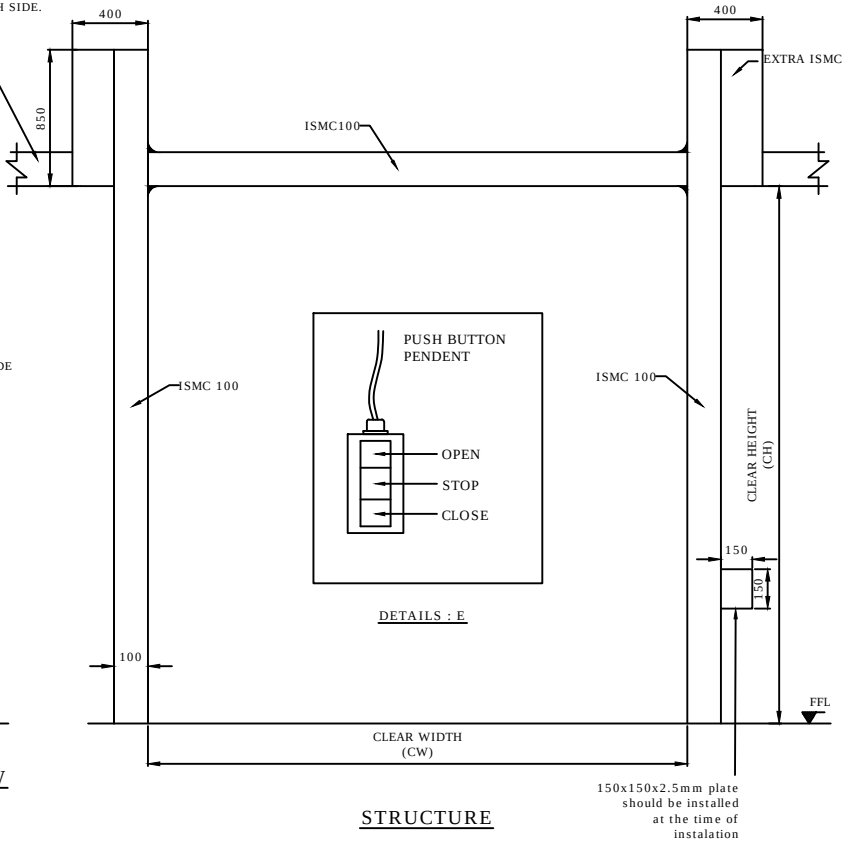


STRUCTURE

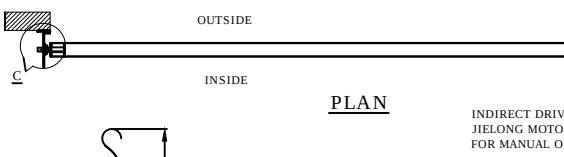


PLAN

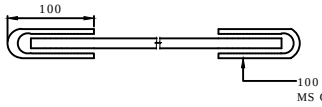


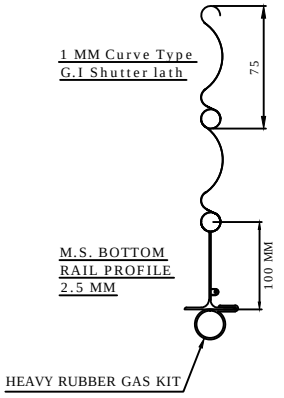

DETAILS : D

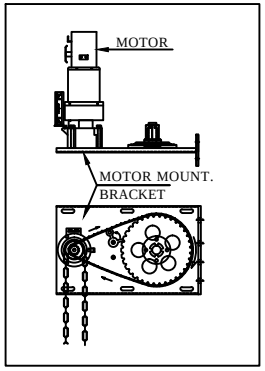

DETAILS : A & B

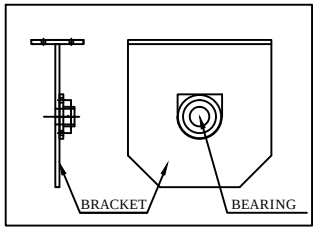

DETAILS : C

3000	3000	1	RAL - 5012
CLEAR WIDTH (CW)	CLEAR HEIGHT (CH)	QUANTITY	RAL COLOR

(NOTE: REQUIRED TECHANICAL STRUCTURE FOR SHUTTER IN CLIENT SCOPE)

REV NO	REV DATE	DRAWN	REMARK
R01	01.02.2020	P.A	2. RAL CODE ADD 1. SHUTTER MOUNTING CLEAR

This drawing & design is the property of NIHVA TECHNOLOGIES. Not to be sold or copied to any other concern.

TITLE: MOTORIZED ROLLING SHUTTER

NIHVA TECHNOLOGIES PVT. LTD.
NIHVA TECHNOLOGIES PVT. LTD. PUNE
Tel : 020 66304033
Email:- info@nihva.com
Website:- www.nihva.com

	NAME	SIGN	DATE
DRAWN	P.A		19.11.2019
CHECK	G.J		19.11.2019
APPRD.			

CLIENT - WANI
PROJECT - BRIDGESTONE
SITE LOCATION - CHAKAN
If any queries contact : design@nihva.com
DWG. NO. : NIHVA/19-20/0154/R01
REV- R01
ALL DIMENSION ARE IN mm
SCALE: NTS
WT:
SHEET: