


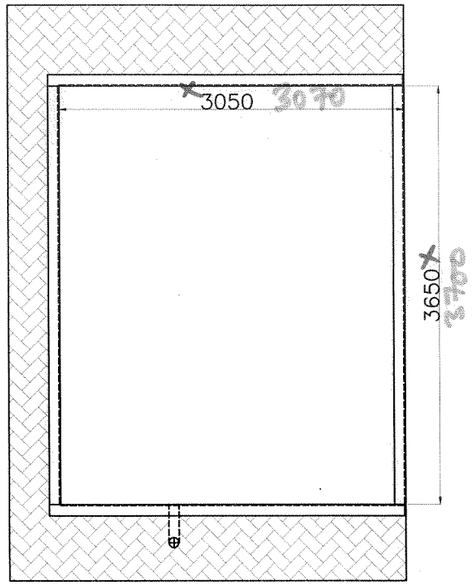


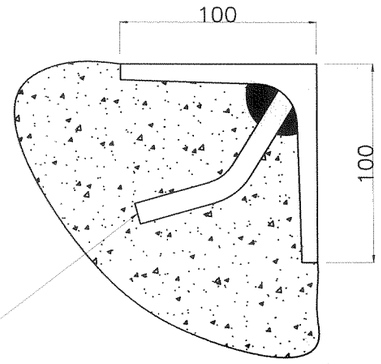

BEND THE M,S.SHEET 4THK.x 60 x 75 LG.
WELD TO THE ANGLE AT AN INTERVAL
OF 500mm FOR BETTER ANCHORING.

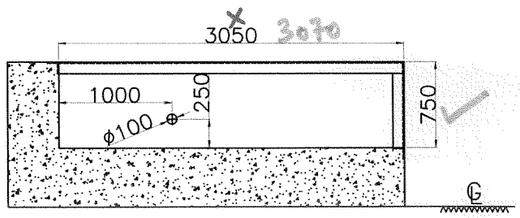

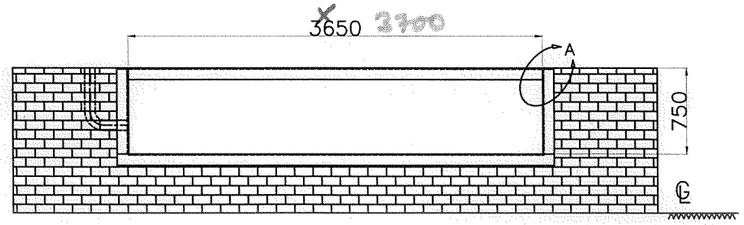

1. CURB ANGLE SIZE 100 X 100 X 10
2. PERIMETER OF PIT FLOOR MUST BE KEPT LEVEL.
3. PROVIDE ONE ϕ100 mm CONDUIT FOR HYDRAULIC HOSE
*4. ROUTING OF HOSE AS PER POWERPACK POITION.
CUSTOMER TO DECIDE

P.O No. : 12-13/3F/10000278
P.O Date : 26.03.2013

Item ref	Part No.	Description	Material	Qty.	Remarks
Designed by	Checked by	Approved by – date	Drawn By Srinivasaiah	Date 05.04.2013	

PUMA LIFT TRUCKS PVT.LTD.,
BANGALORE-560 099

Lift Table PIT Detail

Dwg. PL-3036-00-2 | Scale nts | model phit

Confirmed 10/04/13