

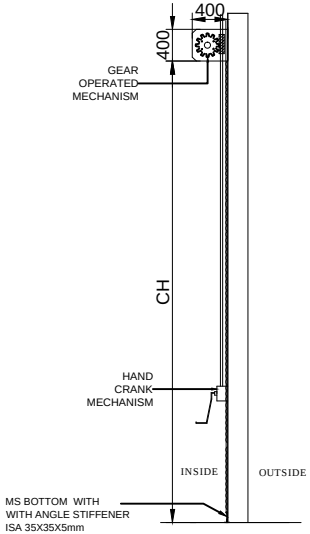



SIDE VIEW

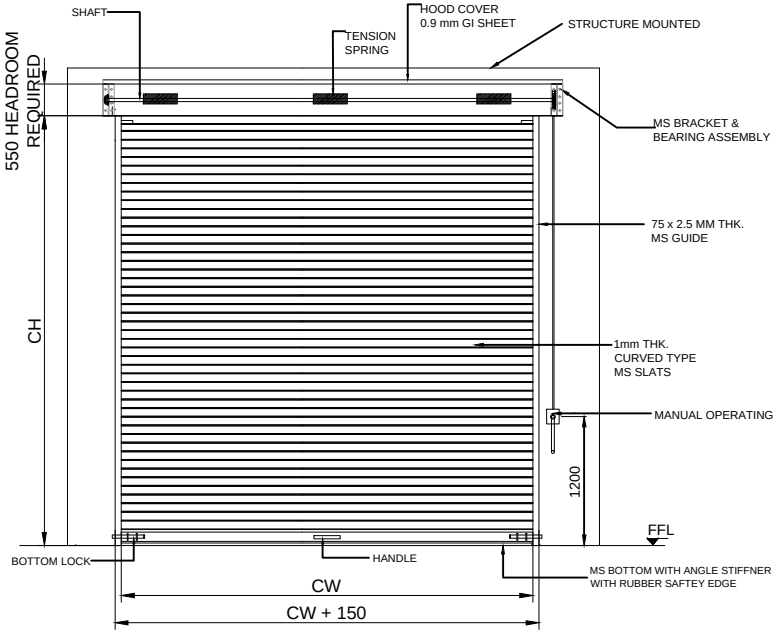


INSIDE ELEVATION

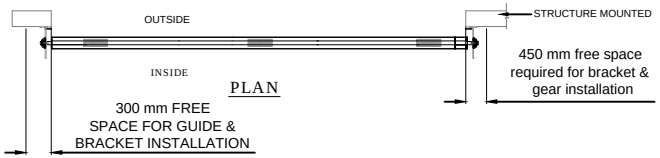

PLAN

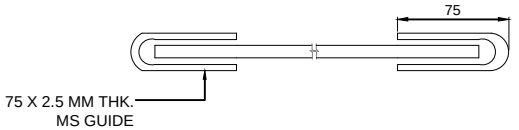

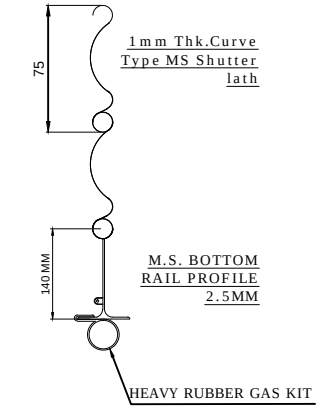

M.S. BOTTOM RAIL PROFILE 2.5MM

RAL 9002	GREY WHITE	APPROVED
RAL CODE	RAL COLOR	APPROVED

TOLERANCE - ±10mm

This drawing & design is the property of NIHVA TECHNOLOGIES. Not to be sold or copied to any other concern.

TITLE
GEAR OPERATED ROLLING SHUTTER

NIHVA TECHNOLOGIES PVT. LTD.

NIHVA TECHNOLOGIES PVT. LTD. PUNE
Tel : 020 66304033
Email:- info@nihva.com
Website:- www.nihva.com

	NAME	SIGN	DATE
DRAWN	S.S.		18.09.2020
CHECK	P.A		18.09.2020
APPRD.			

CLIENT -
PROJECT -
SITE LOCATION -
If any queries contact : design@nihva.com
DWG. NO. : NIHVA/20-21/VDR/0066
REV- R00
ALL DIMENSION ARE IN mm
SCALE: NTS
WT:
SHEET: 01 OF 01

SR NO	(CW) CLEAR WIDTH	(CH) CLEAR HEIGHT	QUANTITY
1	3000	3010	01 NO

NOTE-
1. ALL CIVIL WORK WILL BE CLIENT'S SCOPE.
2. STRUCTURE REQUIRED FOR SHUTTER IS IN CLIENT'S SCOPE.