


DRAWING

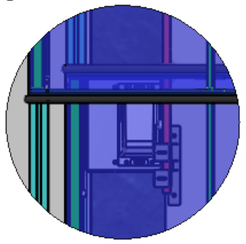


DETAIL C
SCALE 2 : 35

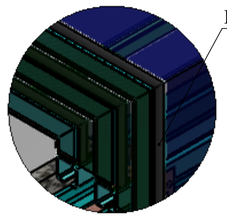


DETAIL D
SCALE 1 : 12

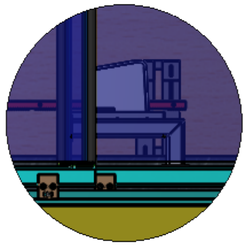


DETAIL E
SCALE 2 : 35

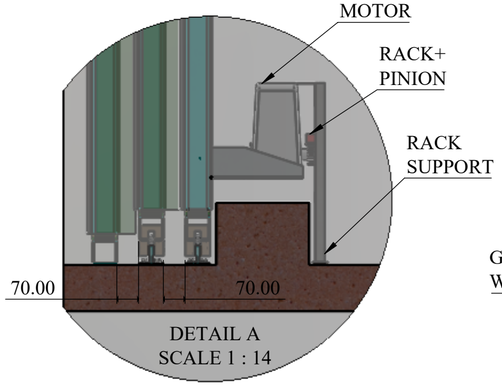


DETAIL A
SCALE 1 : 14

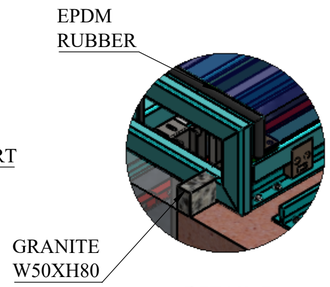


DETAIL F
SCALE 1 : 12

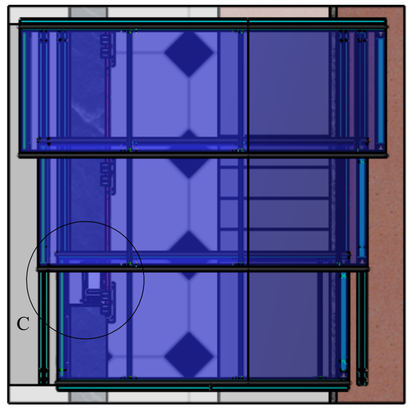


T.V.

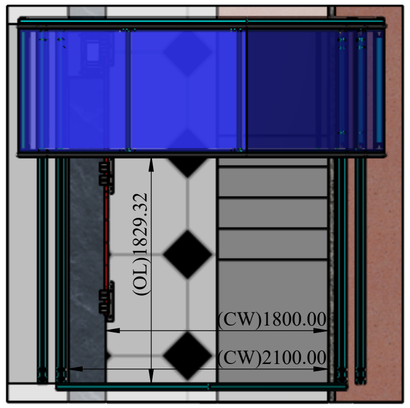


T.V.

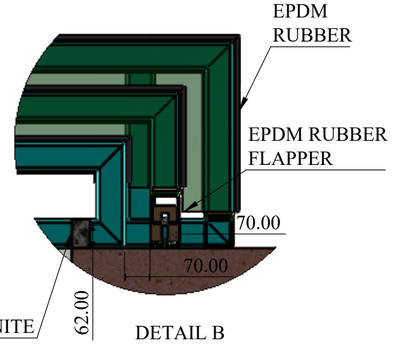


DETAIL B
SCALE 1 : 12

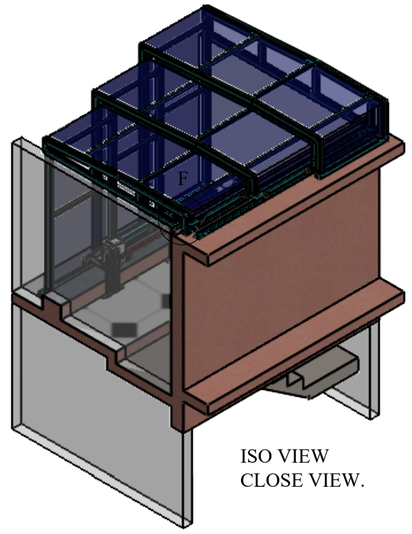


ISO VIEW
CLOSE VIEW.

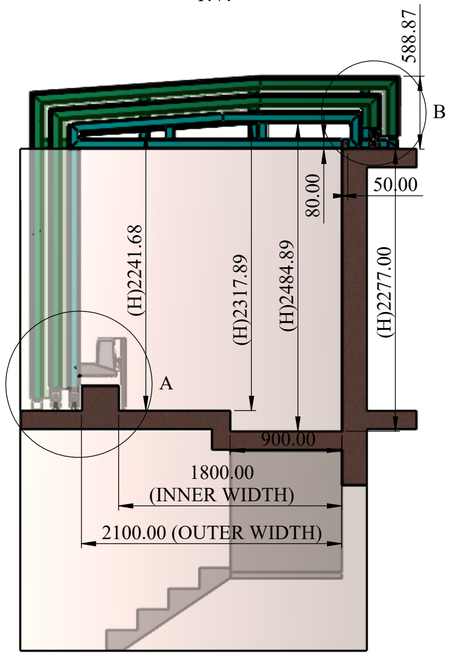


F.V.

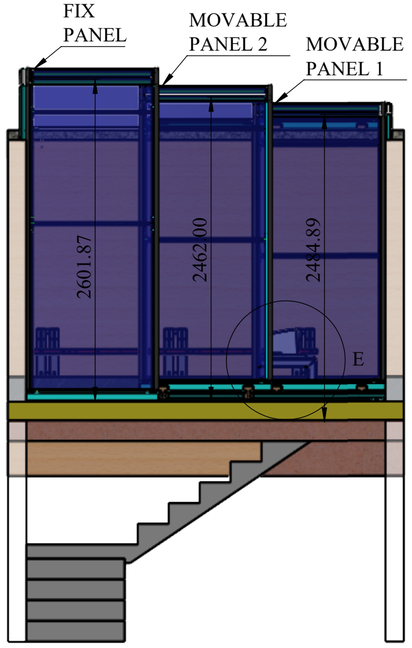

S.V.

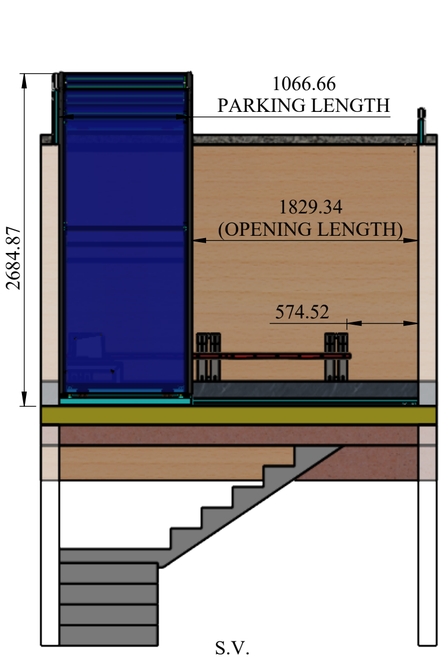

S.V.

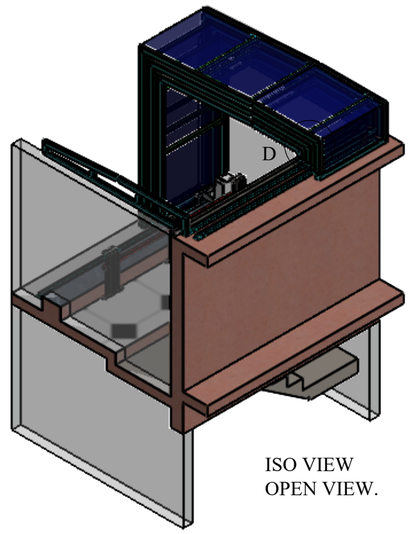

ISO VIEW
OPEN VIEW.

REV DESCRIPTION	DATE	REV NO
	01-08-2026	REV 00
1.		

NOTE :

THIS DRAWING IS FOR CLIENT APPROVAL.
BASE STRUCTURE IN CLIENT SCOPE.
EPDM RUBBER FLAPPER PROVIDED FOR WATER SEAL.
TOTAL SYSTEM WEIGHT - 2223 KG

SPECIAL INSTRUCTION'S :

This drawing & design is the property of NIHVA TECHONOLOGIES PVT. LTD. Not to be sold or copied to any other concern

TITLE - ROOF AUTOMATION

DWG NO - NTPL-

NIHVA TECHNOLOGIES PVT.LTD.PUNE
Website - www.nihva.com

	NAME	SIGNATURE	DATE
DRAWN	V.W.		01-08-2026
CHK'D	S.P.		03-08-2026
APPV'D	V.T.		03-08-2026

PRODUCT - L SHAPE ENCLOSURE
CLIENT NAME - LODHA GROUP.
SITE LOCATION - MUMBAI - MATUNGA.
MATRIAL - | QTY - 1

If any queries contact - info@nihva.com
ALL DIMENSION ARE IN mm | A2
PROJECTION METHOD:
SCALE :
SHEET 1 OF 1