ROOF MONITOR (TYP.)
PRE COLOR COATED STANDING SEAM ROOF SHEETING (TYP.)
EAVE HEIGHT ELEVATION +11.500
FINISH PLINTH LEVEL ELEVATION ± 0.000
FINISH ROAD LVL ELEVATION(-)0.450
18785
W101
600X3600MM WIDE WINDOW CANOPY (TYP.)
600X1800MM WIDE DOOR CANOPY (TYP.)
WINDOW CANOPY (TYP.)
1 2 3 4 5 6 7 8 9 10 11 12 13 14 15 16 17 18 19 20 21 22 23 24 25 26 27 28 29 30 31 32 33 34 35 36 37 38 39 40 41 42 43 44

03 ELEVATION
SCALE 1:250

ROOF MONITOR (TYP.)
PRE COLOR COATED STANDING SEAM ROOF SHEETING (TYP.)
EAVE HEIGHT ELEVATION +11.500
CANOPY BOTTOM LEVEL ELEVATION +5.000
FINISH PLINTH LEVEL ELEVATION ± 0.000
FINISH ROAD LVL ELEVATION(-)0.450
18335
CRANE GIRDER
25/35 TON HOOK HT. 07.50 MT.
4500
D101
RS101
W101
±0.000
WINDOW CANOPY (TYP.)
1 2 3 4 5 6 7 8 9 10 11 12 13 14 15 16 17 18 19 20 21 22 23 24 25 26 27 28 29 30 31 32 33 34 35 36 37 38 39 40 41 42 43 44

02 SECTION
SCALE 1:250

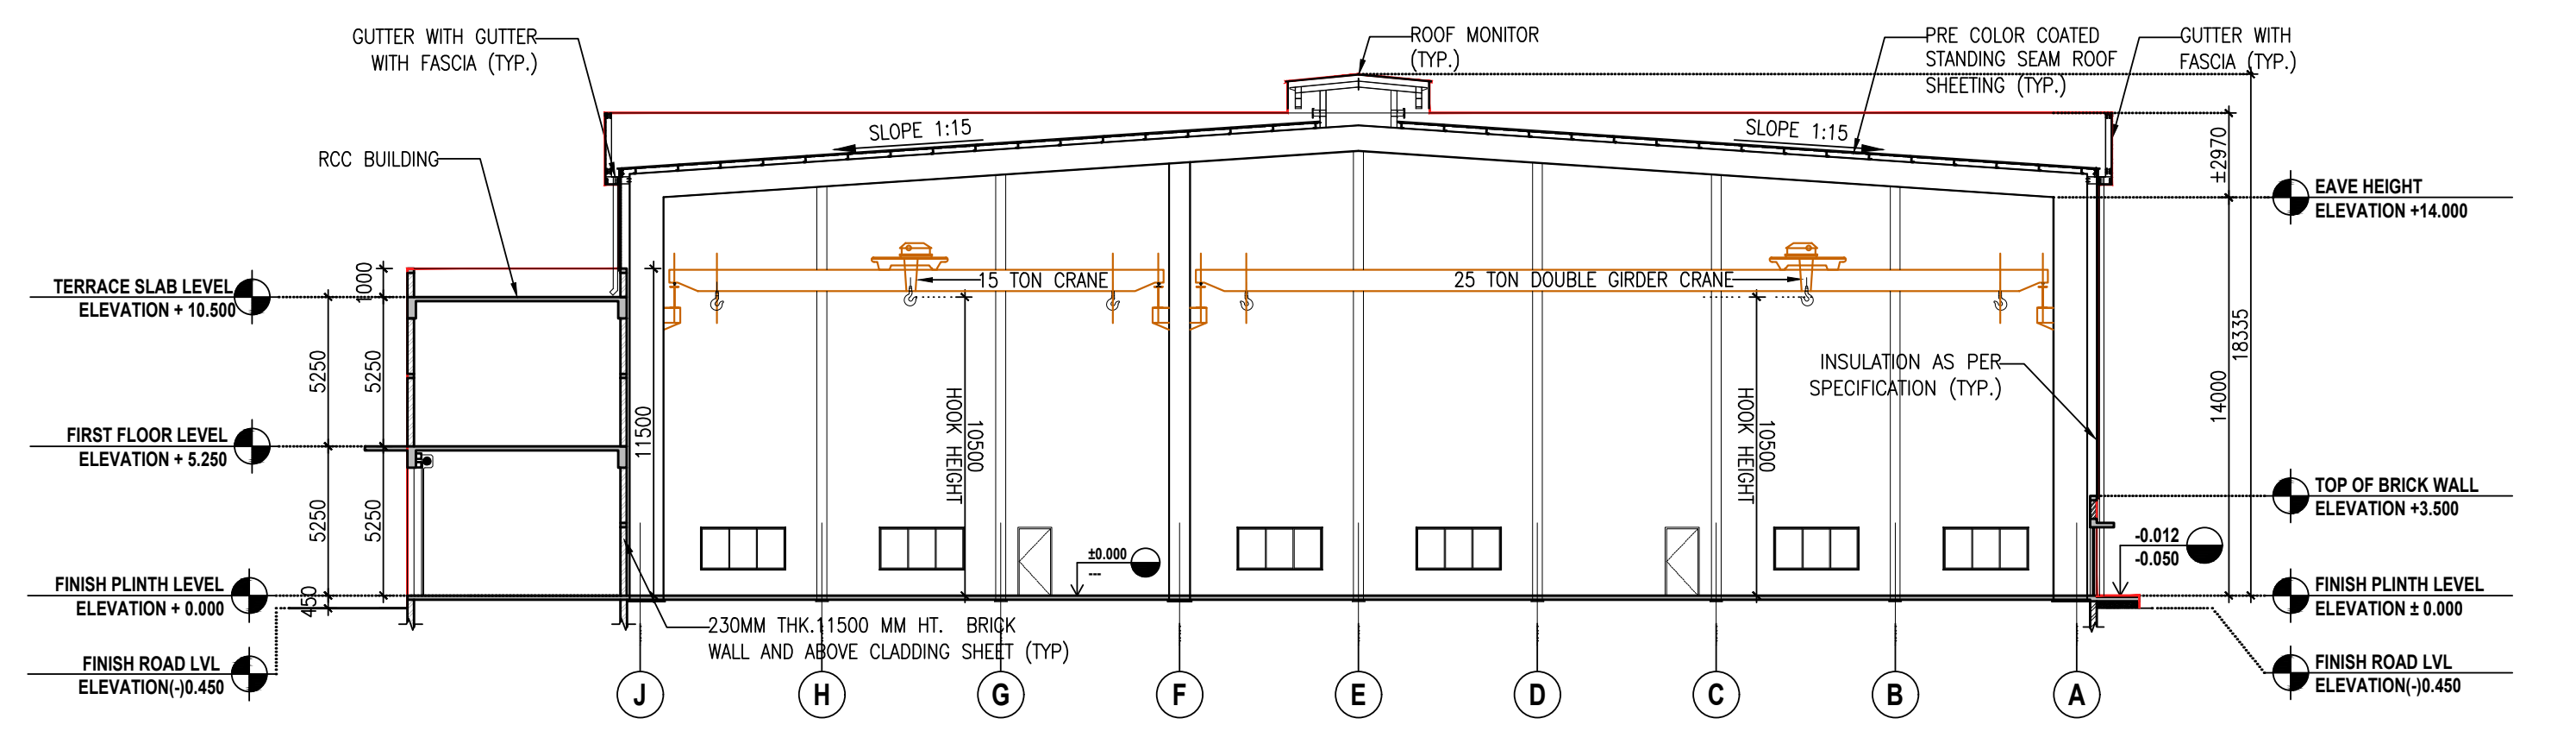
GUTTER WITH GUTTER WITH FASCIA (TYP.)
ROOF MONITOR (TYP.)
PRE COLOR COATED STANDING SEAM ROOF SHEETING (TYP.)
GUTTER WITH FASCIA (TYP.)
SLOPE 1:15
SLOPE 1:15
RCC BUILDING
TERRACE SLAB LEVEL ELEVATION + 10.500
FIRST FLOOR LEVEL ELEVATION + 5.250
FINISH PLINTH LEVEL ELEVATION + 0.000
FINISH ROAD LVL ELEVATION(-)0.450
15 TON CRANE
25 TON DOUBLE GIRDER CRANE
10500 HOOK HEIGHT
11500
INSULATION AS PER SPECIFICATION (TYP.)
EAVE HEIGHT ELEVATION +14.000
TOP OF BRICK WALL ELEVATION +3.500
FINISH PLINTH LEVEL ELEVATION ± 0.000
FINISH ROAD LVL ELEVATION(-)0.450
±2970
14000
18335
5250
1000
450
±0.000
-0.012
-0.050
230MM THK.11500 MM HT. BRICK WALL AND ABOVE CLADDING SHEET (TYP)
J H G F E D C B A

01 SECTION
SCALE 1:250

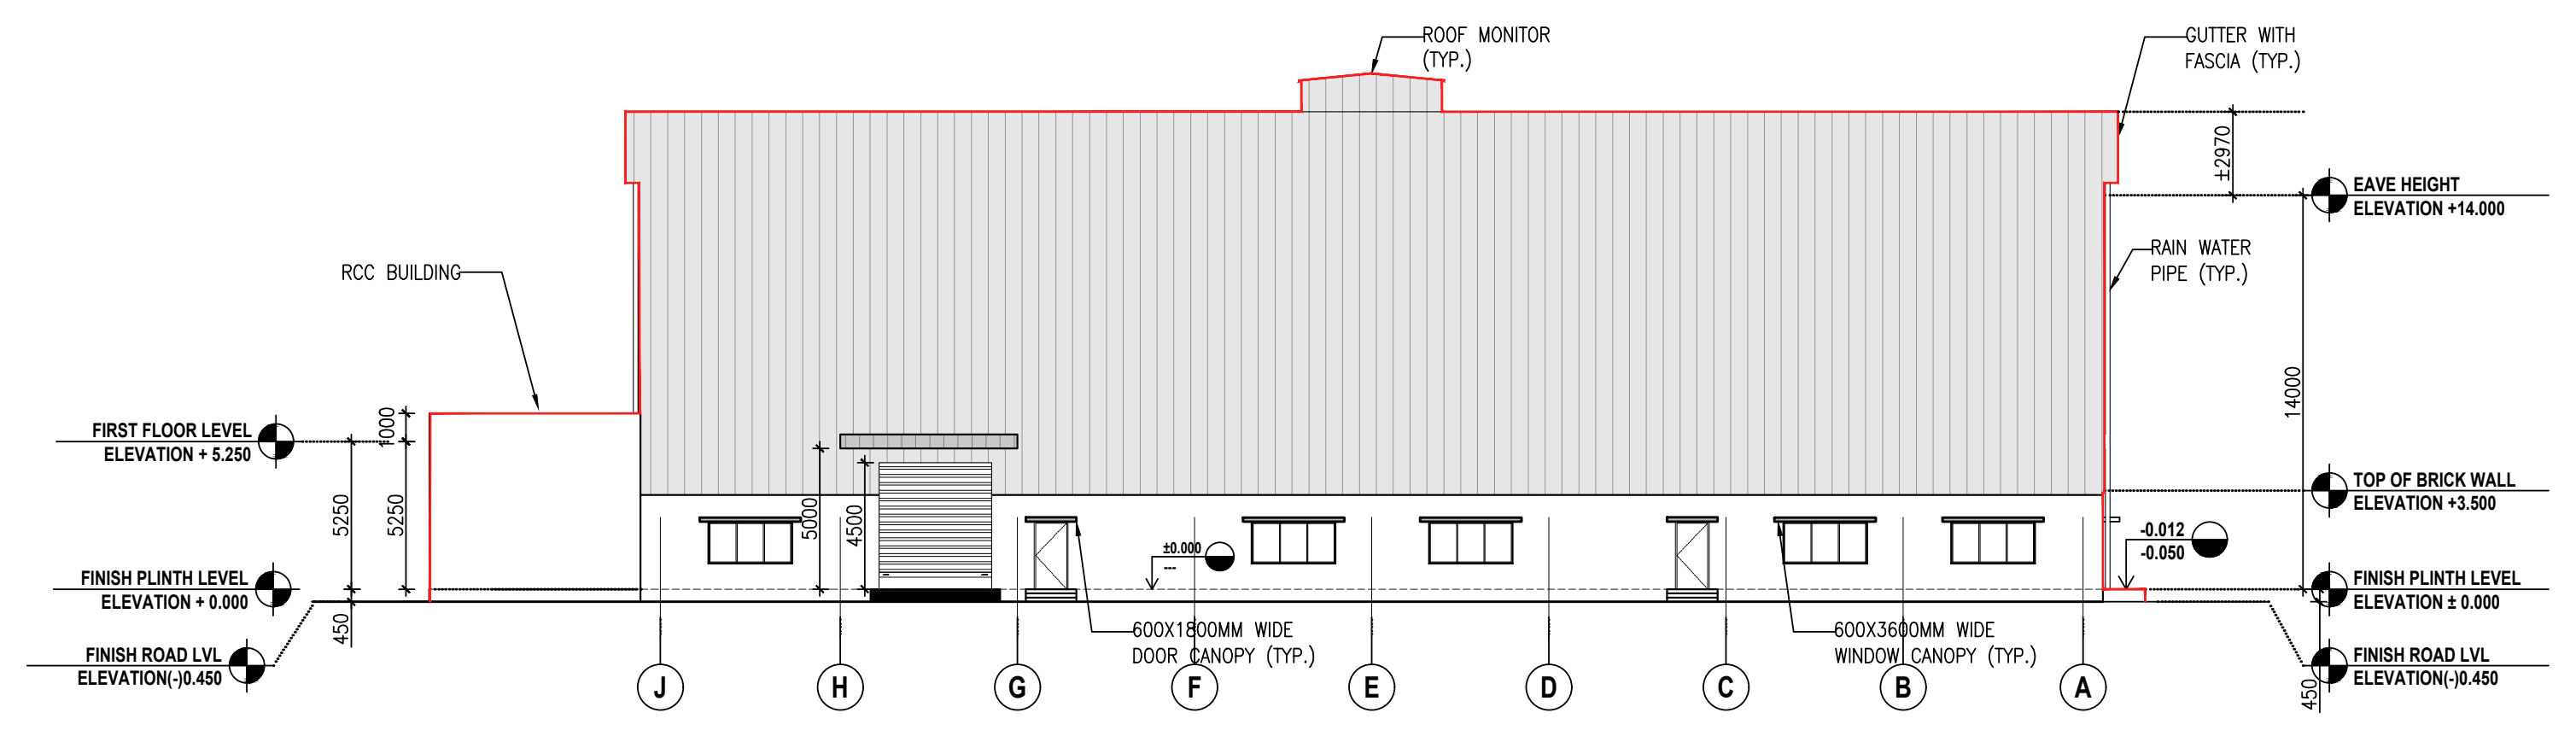
ROOF MONITOR (TYP.)
GUTTER WITH FASCIA (TYP.)
RCC BUILDING
RAIN WATER PIPE (TYP.)
FIRST FLOOR LEVEL ELEVATION + 5.250
FINISH PLINTH LEVEL ELEVATION + 0.000
FINISH ROAD LVL ELEVATION(-)0.450
EAVE HEIGHT ELEVATION +14.000
TOP OF BRICK WALL ELEVATION +3.500
FINISH PLINTH LEVEL ELEVATION ± 0.000
FINISH ROAD LVL ELEVATION(-)0.450
±2970
14000
5250
1000
5000
4500
450
±0.000
-0.012
-0.050
600X1800MM WIDE DOOR CANOPY (TYP.)
600X3600MM WIDE WINDOW CANOPY (TYP.)
J H G F E D C B A

04 ELEVATION
SCALE 1:250

THIS DRAWING & DESIGN IS THE SOLE PROPERTY OF VMS & SHALL NOT BE COPIED,
TRACED OR REPRODUCED BY ANY MEANS WITHOUT PRIOR WRITTEN CONSENT OF THE FIRM.

GENERAL NOTES :

1. ALL THE DIMENSIONS ARE UNFINISHED DIMENSIONS.
2. ALL DIMENSIONS ARE IN MM AND LEVELS ARE IN MT, UNLESS OTHERWISE MENTIONED.
3. ALL THE DIMENSIONS SHALL BE READ & NOT TO BE MEASURED.
4. IN CASE OF ANY DISCREPANCY, BRING IT TO THE NOTICE OF THE ARCHITECT IMMEDIATELY.
5. DETAIL DRAWING PRECEDES THE GENERAL DRAWING

FOR TENDER

NO.	DATE	DESCRIPTION	DRAWN BY	CHECKED BY
R0	-	-	-	-

REVISION HISTORY

KEY PLAN
SCALE : N.T.S.

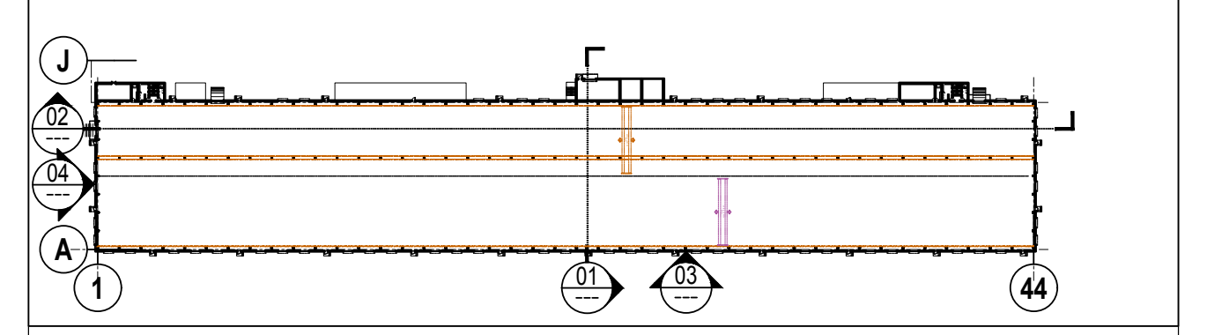

REFERENCE DRAWINGS :

01. ARCHITECTURAL :	-
02. STRUCTURAL :	-
03. HVAC :	-
04. ELECTRICAL :	-
05. UTILITIES :	-

SECTIONS & ELEVATIONS

HRM SHED

AGRAWAL METAL WORKS(P) LTD.

PROJECT NO.	SCALE :	DRAWN :	SURENDER Y.
3824	AS SHOWN	CHECKED:	BHAKTI B.
	DATE : 03-12-2024	APPROVED:	DARSH D.
		COORDINATION CHECKED:	DARSH D.

ENGINEERING + ARCHITECTURE
VMS ENGINEERING & DESIGN SERVICES (P) LTD.
CHITRAKOOT FLATS, B/H TIMES OF INDIA, OFF ASHRAM ROAD,
AHMEDABAD-380 009. PHONE: +91 (079) 2658-8829, 4023-6236
WWW.VMSCONSULTANTS.COM

SHEET SIZE	DRAWING NO.	TENDER	REVISION:
600x 1800	T.A.2.201	T	R0