




SIDE VIEW

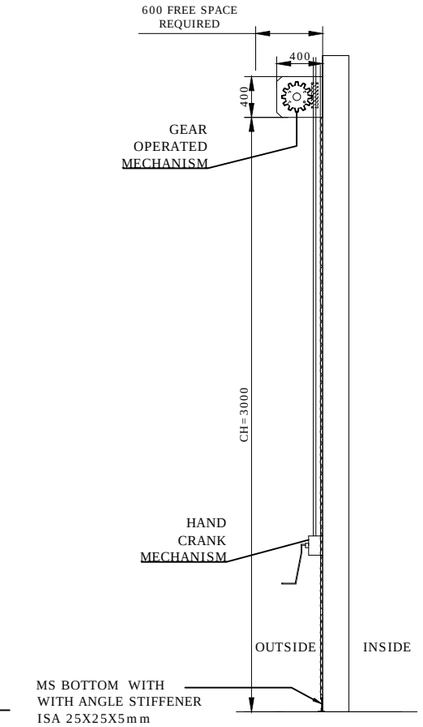


OUTSIDE ELEVATION

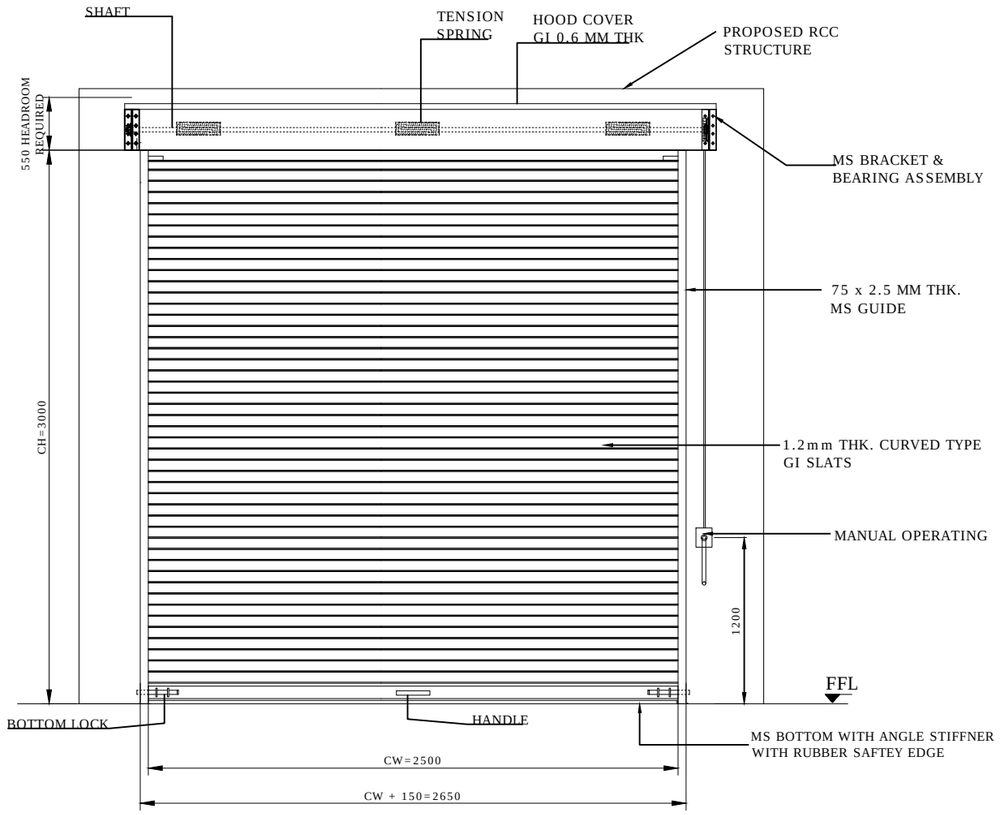

PLAN

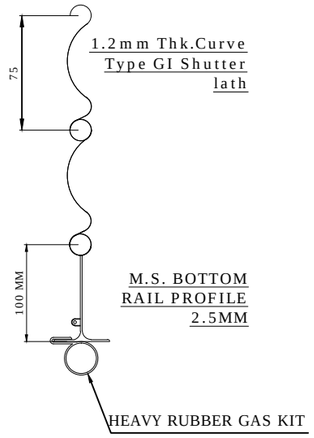

M.S. BOTTOM RAIL PROFILE 2.5MM

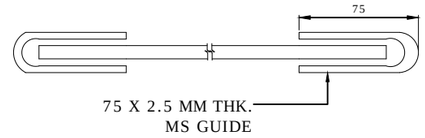

RAL CODE	RAL COLOR	APPROVAL
RAL 7040	WINDOW GREY	APPROVED

SR NO	(CW) CLEAR WIDTH	(CH) CLEAR HEIGHT	QUANTITY
1	2500	3000	04 NO

TOLERANCE - ±10mm

NOTE-
1. ALL DIMENSIONS ARE IN MM.
2. SURFACE FINISH: POWDER COATING OF APPROVED RAL CODE.
3. MOUNTING ON OUTSIDE CONCRETE STRUCTURE.
4. MOUNTING OF LEVER WILL BE ON RIGHT SIDE.

This drawing & design is the property of NIHVA TECHNOLOGIES. Not to be sold or copied to any other concern.

TITLE
GEAR OPERATED ROLLING SHUTTER

	NAME	SIGN	DATE
DRAWN	G.I.P		23.02.2022
CHECK	A.K.		23.02.2022
APPRD.	V.T.		23.02.2022

If any queries contact : design@nihva.com

ALL DIMENSION ARE IN mm

NIHVA TECHNOLOGIES PVT. LTD.
Website:- www.nihva.com
NIHVA TECHNOLOGIES PVT. LTD. PUNE
Tel : 020 66304033
Email:- info@nihva.com

CLIENT -

PROJECT -GEAR OPERATED ROLLING SHUTTER

SITE LOCATION -

DWG. NO. : NIHVA/21-22/VDR/028 | REV- R0

SCALE: NTS | WT: | SHEET: 01 OF 01