


DRAWING

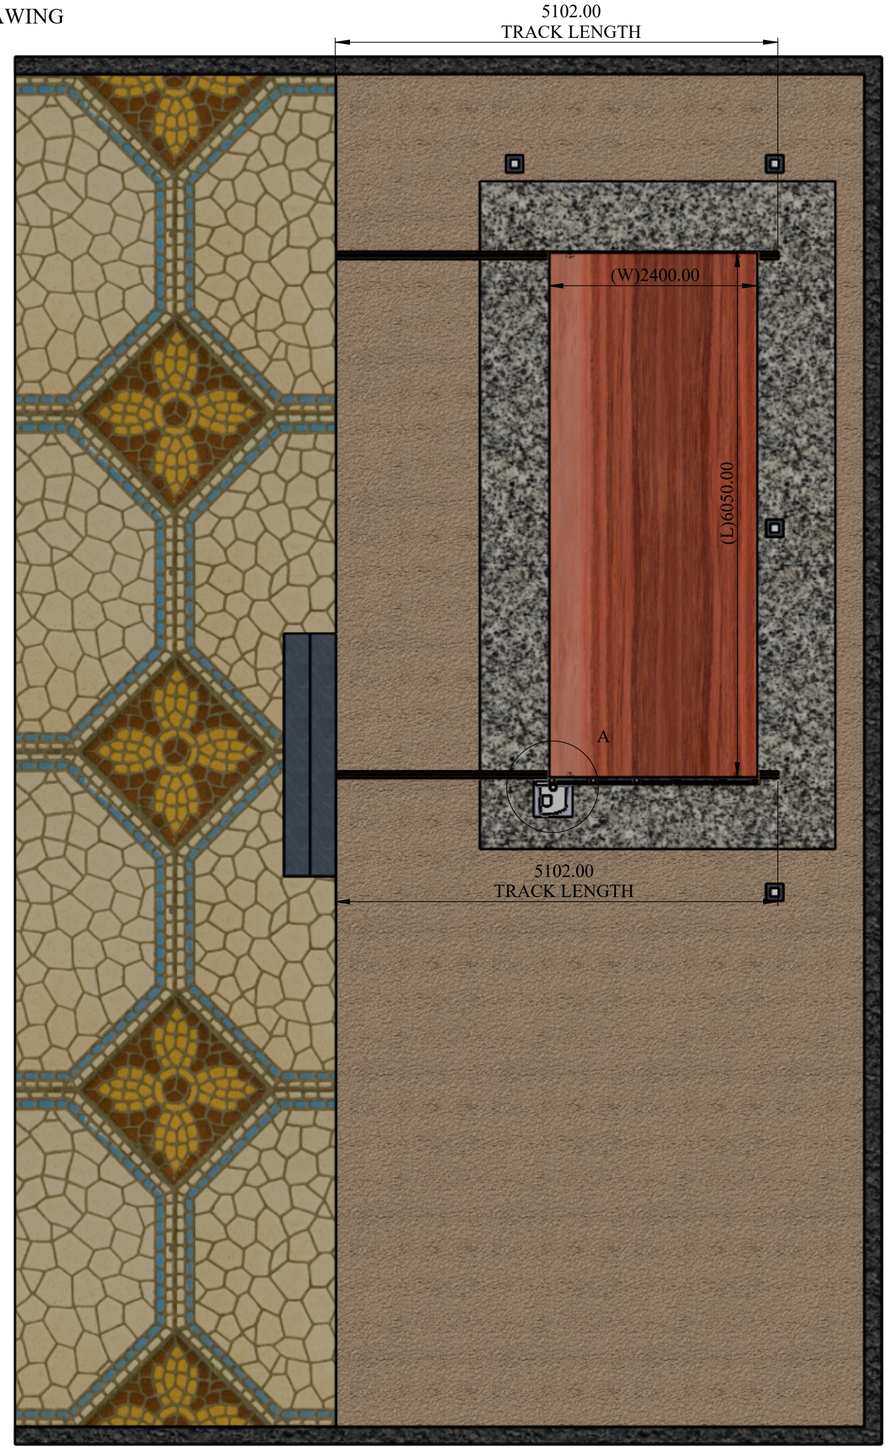


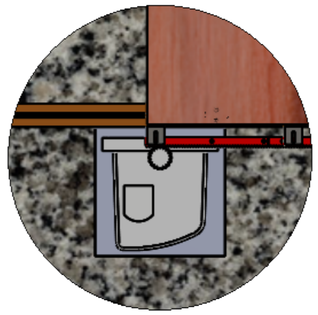


DETAIL A
SCALE 1 : 15

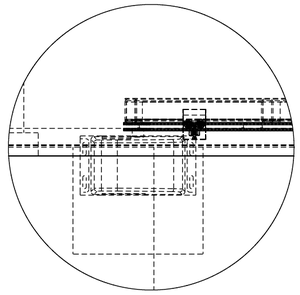

DETAIL B
SCALE 1 : 15

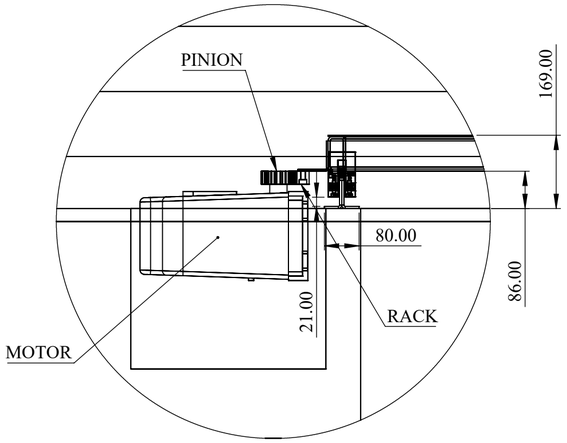

DETAIL C
SCALE 1 : 10

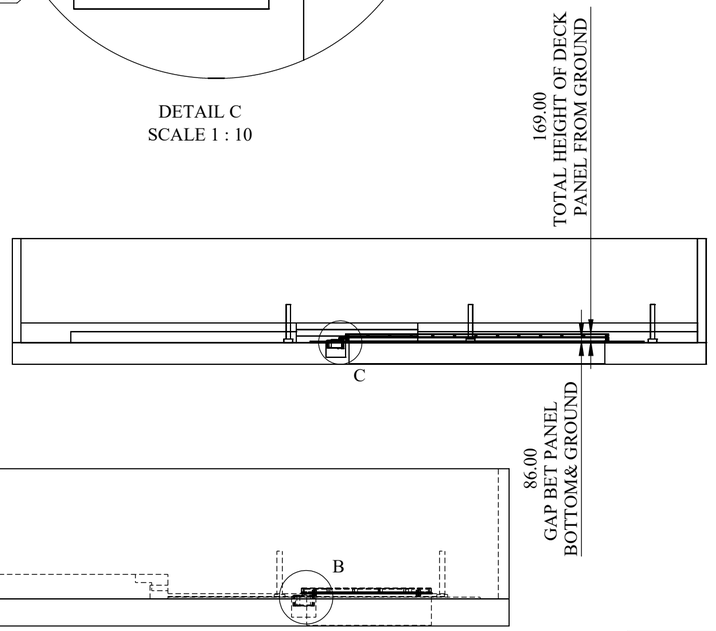

REV DESCRIPTION	DATE	REV NO
	01-04-2026	REV 00
1.		

NOTE :

SPECIAL INSTRUCTION'S :

TITLE - ROOF AUTOMATION

DWG NO - NTPL-000-PM-001-00-00-00

NIHVA Technologies Pvt. Ltd.

NIHVA TECHNOLOGIES PVT.LTD.PUNE
Website - www.nihva.com

	NAME	SIGNATURE	DATE
DRAWN	V.W.		01-04-2026
CHK'D	B.S.		03-04-2026
APPV'D	V.T.		03-04-2026

PRODUCT - SWIMMING POOL DECK

PROJECT NO - NTPL-000-PM | REVISION - 00

SITE LOCATION - | WEIGHT -

MATERIAL - | QTY - 1

If any queries contact - Design@nihva.com


ALL DIMENSION ARE IN mm | A2


PROJECTION METHOD:

SCALE :

DRAWING

REV DESCRIPTION	DATE	REV NO
	01-04-2026	REV 00
1.		

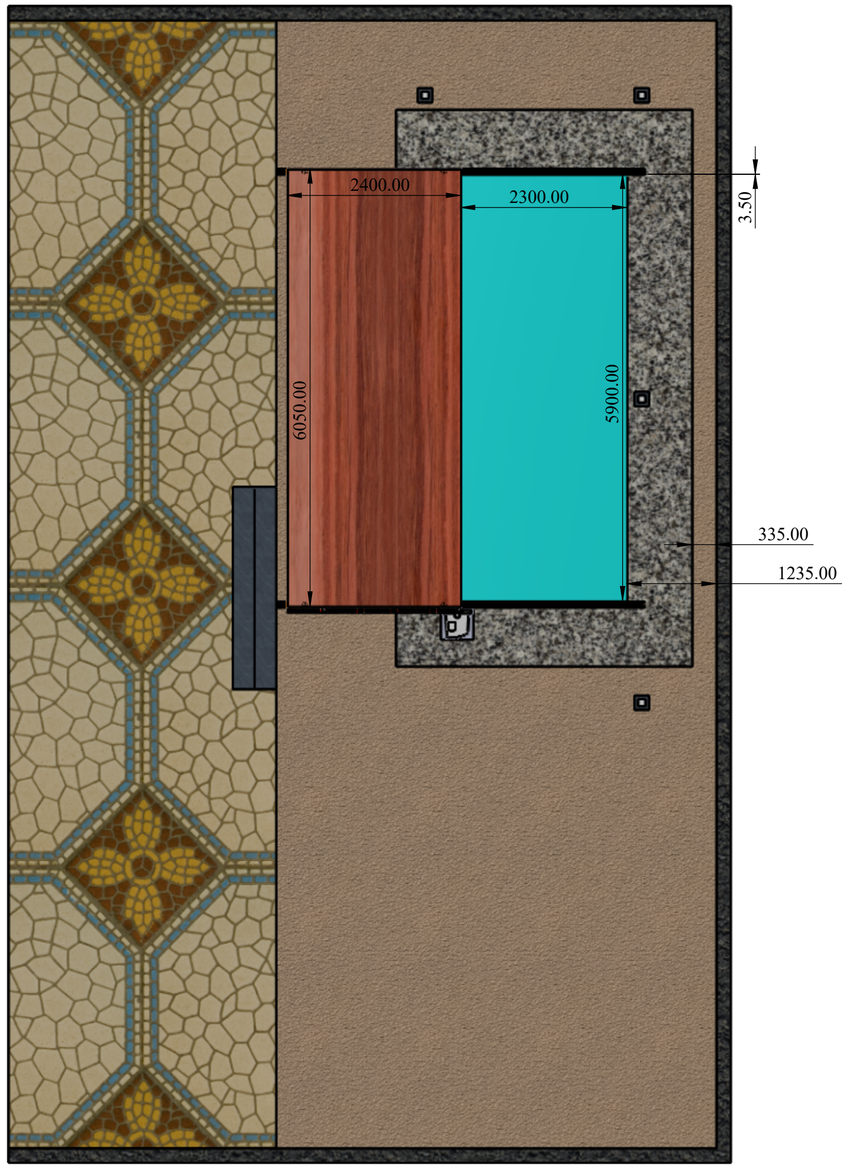

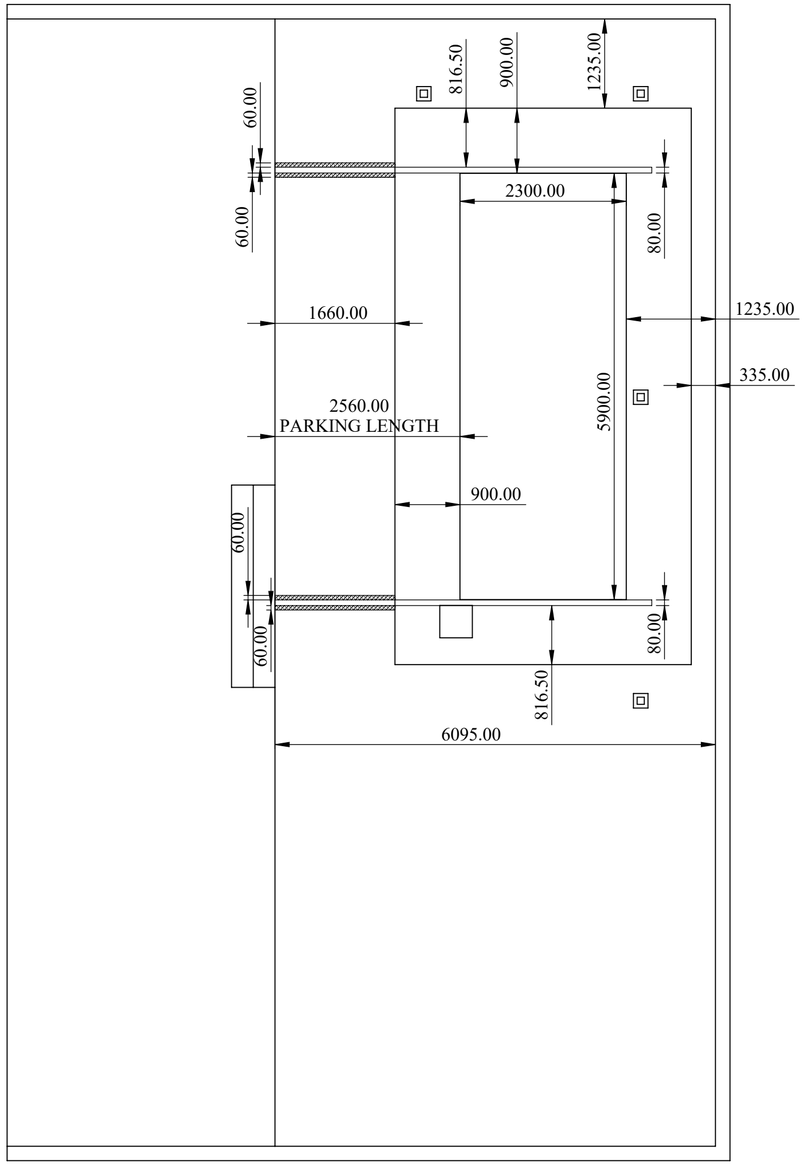

NOTE :

SPECIAL INSTRUCTION'S :

TITLE - ROOF AUTOMATION

DWG NO - NTPL-000-PM-001-00-00-00

NIHVA Technologies Pvt. Ltd.

NIHVA TECHNOLOGIES PVT.LTD.PUNE
Website - www.nihva.com

	NAME	SIGNATURE	DATE
DRAWN	V.W.		01-04-2026
CHK'D	B.S.		03-04-2026
APPV'D	V.T.		03-04-2026

PRODUCT - SWIMMING POOL DECK

PROJECT NO - NTPL-000-PM | REVISION - 00

SITE LOCATION - | WEIGHT -

MATERIAL - | QTY - 1


If any queries contact - Design@nihva.com

ALL DIMENSION ARE IN mm | A2


PROJECTION METHOD:

SCALE :


DRAWING

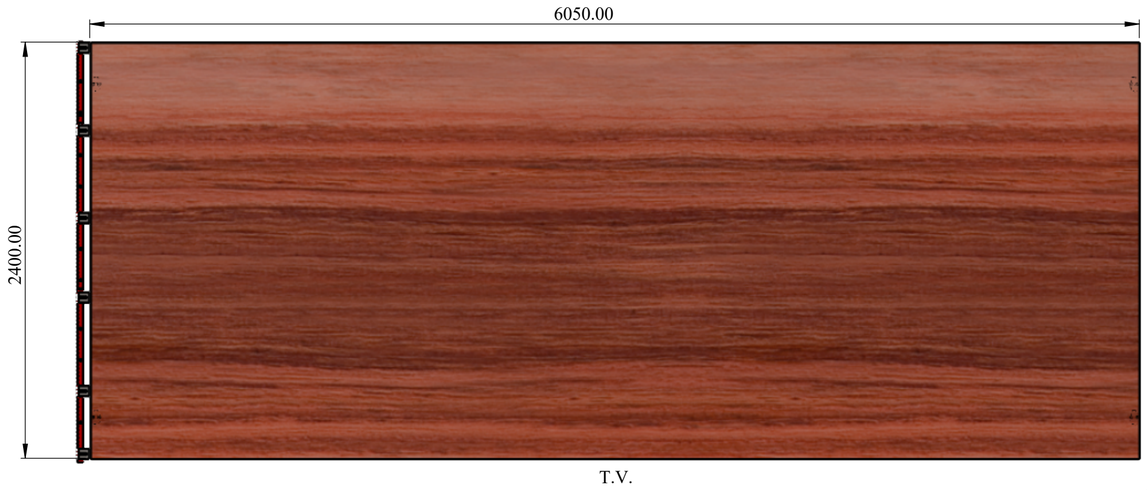


T.V.

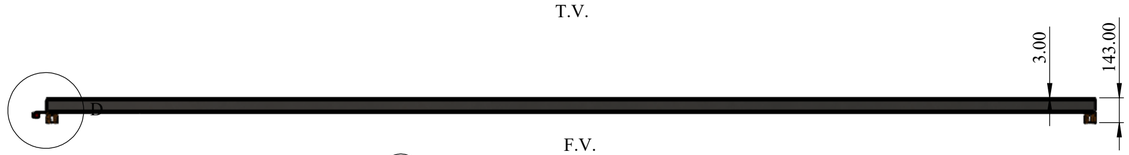

F.V.

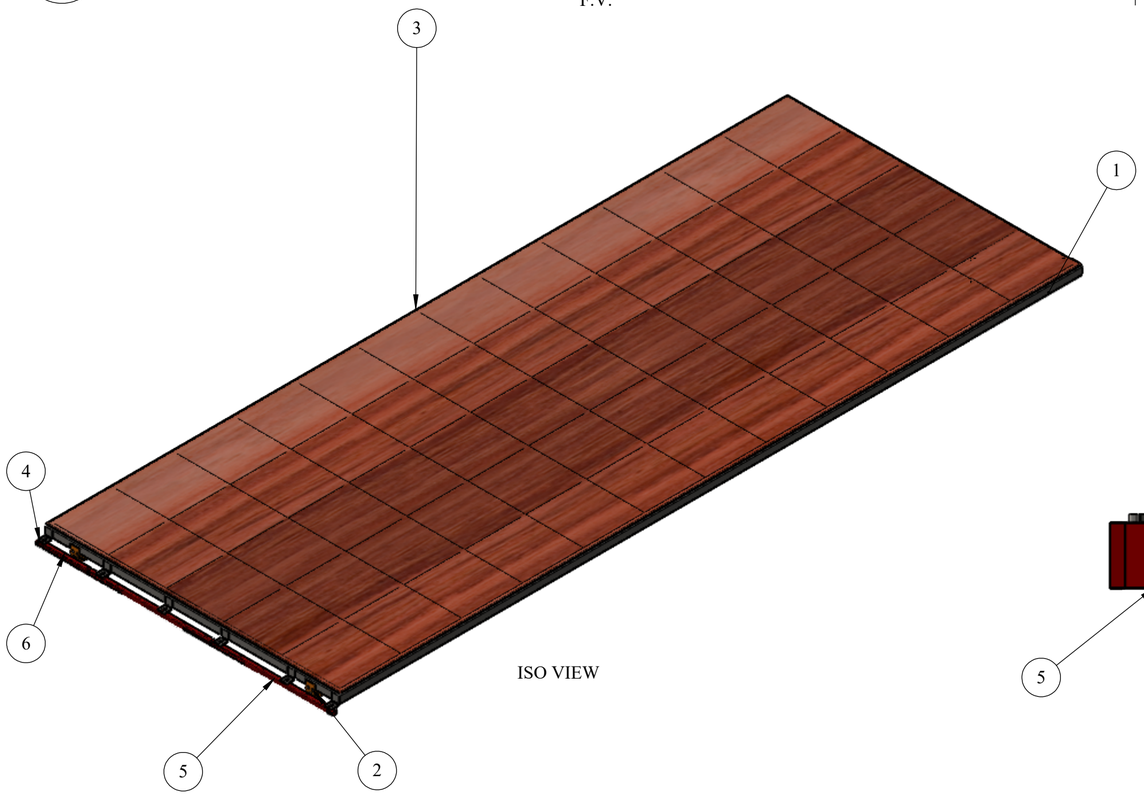

ISO VIEW

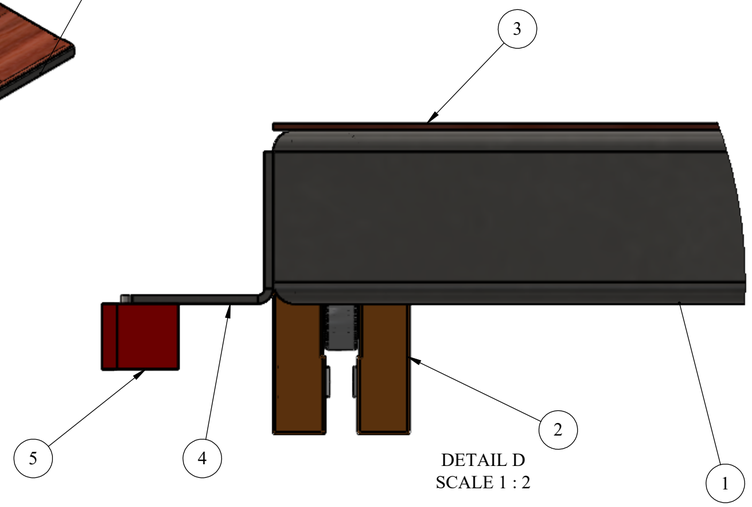

DETAIL D
SCALE 1 : 2

ITEM NO.	PART NUMBER	DESCRIPTION	QTY.
1	PANEL		1
2	BAERING HOUSING ASSEMBLY		4
3	SS SHEET		1
4	RACK SUPPORT PLATE	ss	6
5	RACK M6 MODULE	STD (M4 RACK, 30x8x1000 mm, ZINC COATED WITH SPACERS AND SCREWS.)	2
6	RACK M6 MODULE CUT PART .	STD (M4 RACK, 30x8x1000 mm, ZINC COATED WITH SPACERS AND SCREWS.)	1

REV DESCRIPTION	DATE	REV NO
	01-04-2026	REV 00
1.		

NOTE :

SPECIAL INSTRUCTION'S :

TITLE - ROOF AUTOMATION

DWG NO - NTPL-000-PM-001-00-00-00

NIHVA Technologies Pvt. Ltd.

NIHVA TECHNOLOGIES PVT.LTD.PUNE
Website - www.nihva.com

	NAME	SIGNATURE	DATE
DRAWN	V.W.		01-04-2026
CHK'D	B.S.		03-04-2026
APPV'D	V.T.		03-04-2026

PRODUCT - SWIMMING POOL DECK

PROJECT NO - NTPL-000-PM | REVISION - 00

SITE LOCATION - | WEIGHT -

MATERIAL - | QTY - 1

If any queries contact - Design@nihva.com


ALL DIMENSION ARE IN mm | A2


PROJECTION METHOD:


SCALE :

DRAWING

ITEM NO.	PART NUMBER	DESCRIPTION	QTY.
1	PANEL		1

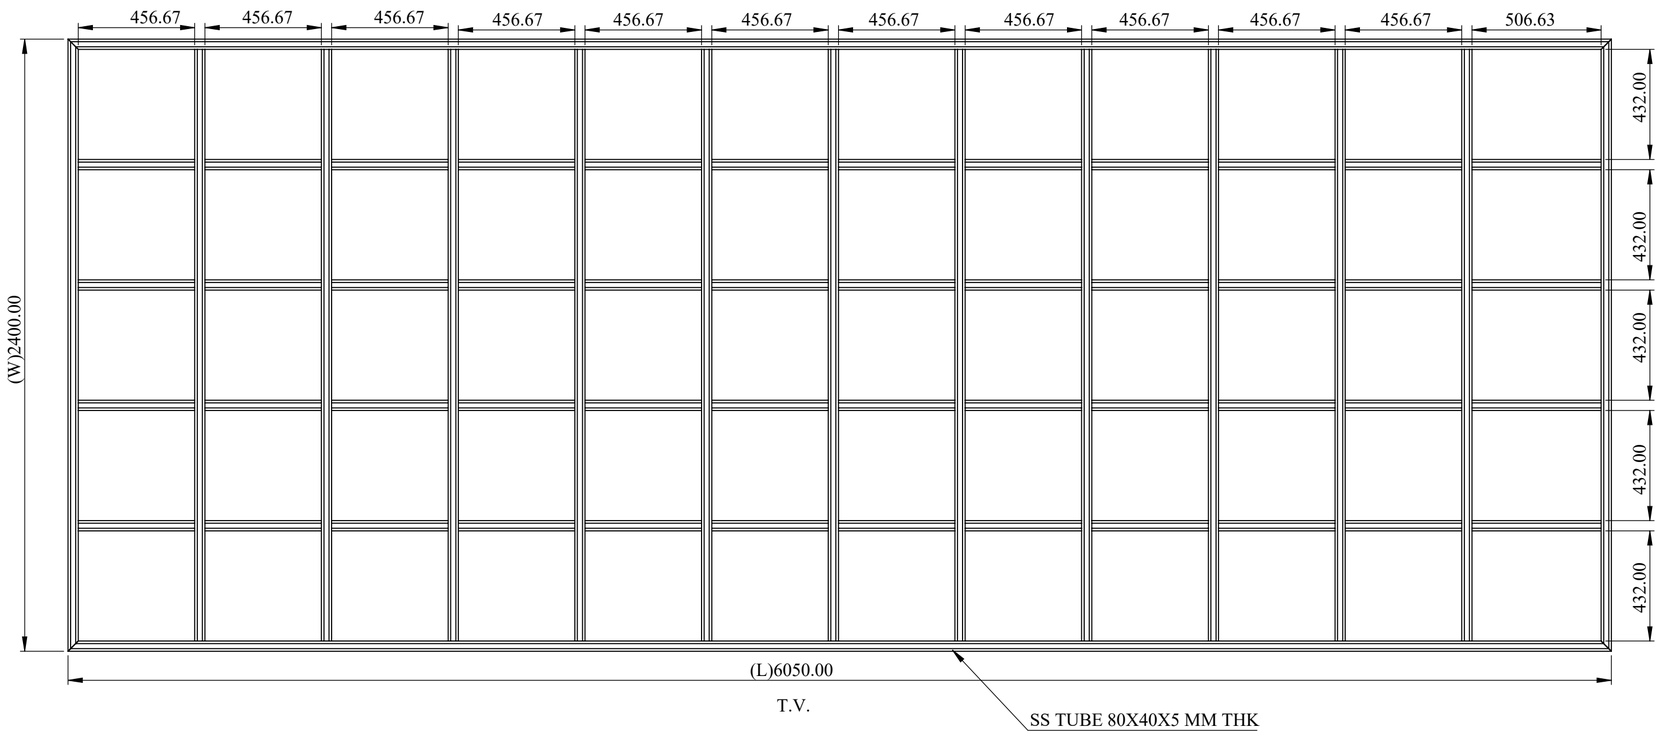

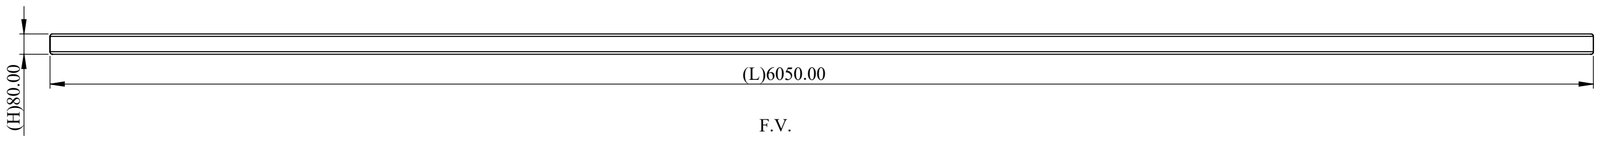

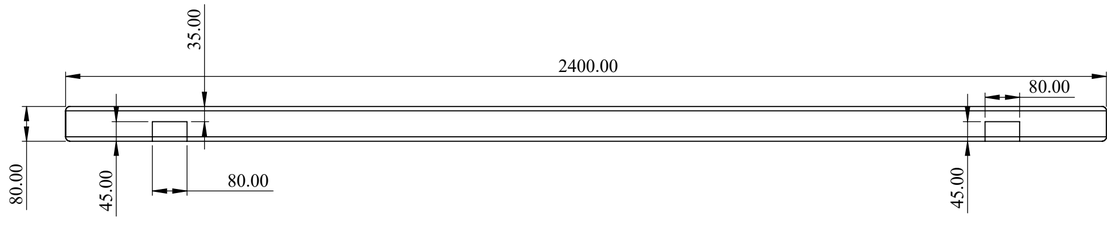

REV DESCRIPTION	DATE	REV NO
	01-04-2026	REV 00
1.		

NOTE :

SPECIAL INSTRUCTION'S :

TITLE - ROOF AUTOMATION

DWG NO - NTPL-000-PM-001-00-00-00

NIHVA Technologies Pvt. Ltd.

NIHVA TECHNOLOGIES PVT.LTD.PUNE
Website - www.nihva.com

	NAME	SIGNATURE	DATE
DRAWN	V.W.		01-04-2026
CHK'D	B.S.		03-04-2026
APPV'D	V.T.		03-04-2026

PRODUCT - SWIMMING POOL DECK

PROJECT NO - NTPL-000-PM | REVISION - 00

SITE LOCATION - | WEIGHT - 531.93 KG

MATERIAL - SS | QTY - 1

If any queries contact - Design@nihva.com


PROJECTION METHOD:

SCALE :


ALL DIMENSION ARE IN mm | A2

SHEET 4 OF 17

DRAWING

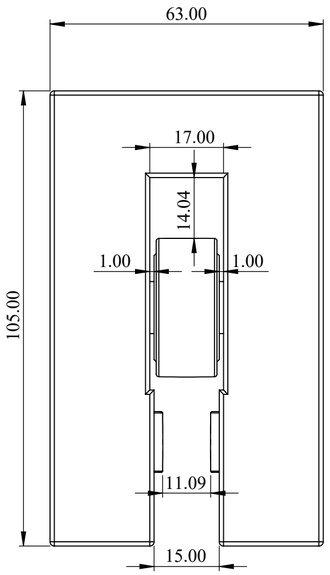


F.V.

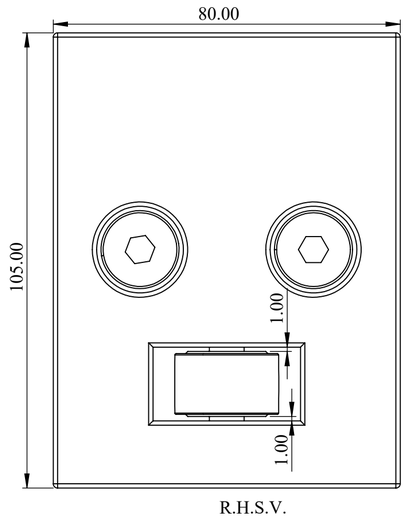


R.H.S.V.

ITEM NO.	PART NUMBER	DESCRIPTION	QTY.
1	BEARING BLOCK (T75-1B)	80X105X63 MM (VMC PART)	1
2	BEARING_SKF_NATR 12	BRG (SIZE- OD32 X ID12 X W15 MM)	2
3	SHOULDER BOLT NATR 12 (M12X35 MM)	M12X35 MM	2
4	SKF_NATR 8	BRG(SIZE- OD24 X ID8 X W15 MM)	2
5	SHOULDER BOLT NATR 8 (M8X30 MM)	M8X30 MM	2

REV DESCRIPTION	DATE	REV NO
	01-04-2026	REV 00
1.		

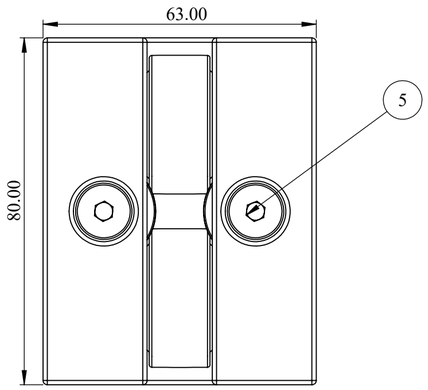

B.V.

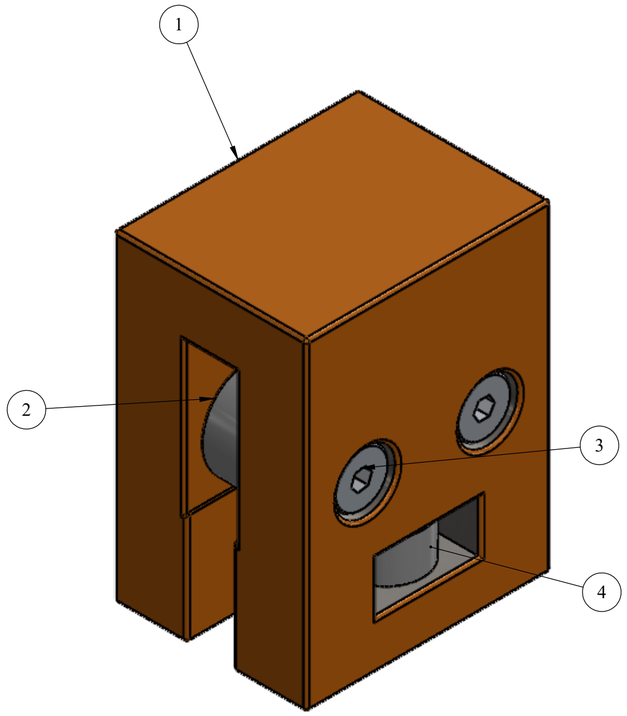

ISO VIEW

NOTE :

NOTE.:
NAME: BEARING BLOCK HOUSING ASSEMBLY
SIZE : 105 X 80 X 63 MM
MTL : SS
QTY : 04 NO'S

SPECIAL INSTRUCTION'S :

TITLE - ROOF AUTOMATION

DWG NO - NTPL-000-PM-001-00-00-00

NIHVA Technologies Pvt. Ltd.

NIHVA TECHNOLOGIES PVT.LTD.PUNE
Website - www.nihva.com


	NAME	SIGNATURE	DATE
DRAWN	V.W.		01-04-2026
CHK'D	B.S.		03-04-2026
APPV'D	V.T.		03-04-2026

PRODUCT - SWIMMING POOL DECK
PROJECT NO - NTPL-000-PM | REVISION - 00
SITE LOCATION - | WEIGHT -
MATERIAL - | QTY - 1
If any queries contact - Design@nihva.com
ALL DIMENSION ARE IN mm | A2
PROJECTION METHOD:
SCALE :


DRAWING

REV DESCRIPTION	DATE	REV NO
	01-04-2026	REV 00
1.		


ITEM NO.	PART NUMBER	DESCRIPTION	QTY.
1	BEARING BLOCK (T75-1B)	80X105X63 MM (VMC PART)	4

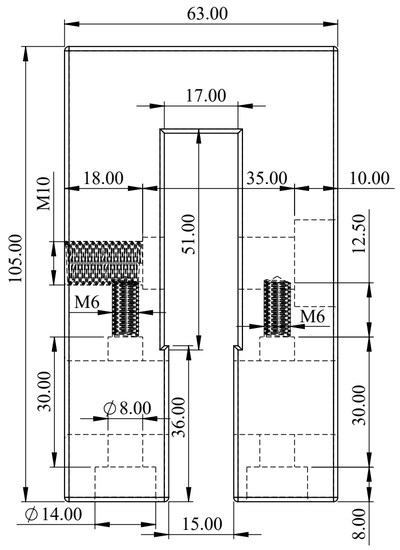


F.V

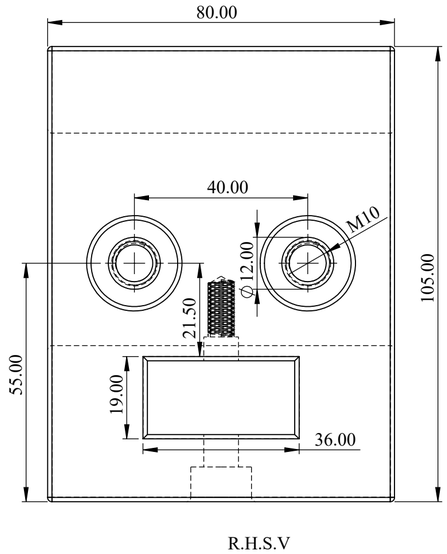

R.H.S.V

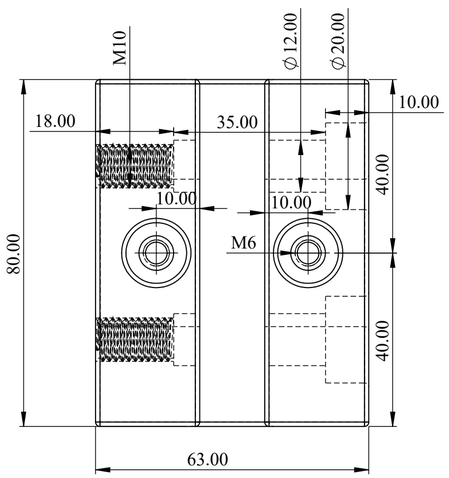

B.V

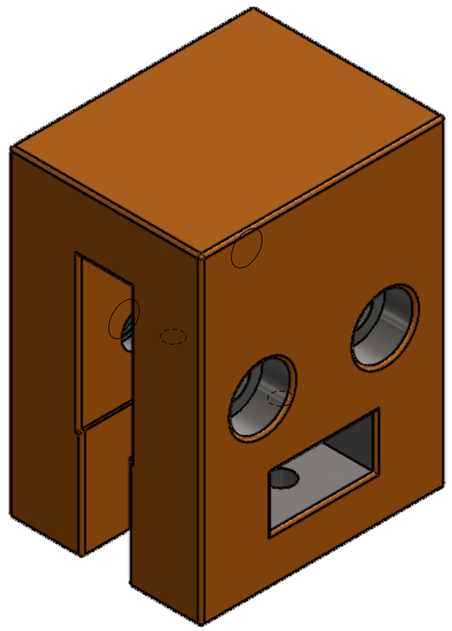

ISO VIEW

NOTE :

NOTE.:
NAME: BEARING BLOCK
SIZE : 105 X 80 X 63 MM
MTL : SS
QTY : 04 NO'S

SPECIAL INSTRUCTION'S :

TITLE - ROOF AUTOMATION

DWG NO - NTPL-000-PM-001-00-00-00

NIHVA Technologies Pvt. Ltd.

NIHVA TECHNOLOGIES PVT.LTD.PUNE
Website - www.nihva.com

	NAME	SIGNATURE	DATE
DRAWN	V.W.		01-04-2026
CHK'D	B.S.		03-04-2026
APPV'D	V.T.		03-04-2026


PRODUCT - SWIMMING POOL DECK
PROJECT NO - NTPL-000-PM
REVISION - 00
SITE LOCATION -
WEIGHT - 2.99 KG
MATERIAL - SS
QTY - 1
SCALE :


If any queries contact - Design@nihva.com
ALL DIMENSION ARE IN mm
A2
PROJECTION METHOD:


DRAWING

REV DESCRIPTION	DATE	REV NO
	01-04-2026	REV 00
1.		

ITEM NO.	PART NUMBER	DESCRIPTION	QTY.
1	BEARING_SKF_NATR 12	BRG(STD) (SIZE-OD32XID12XW15 MM)	08

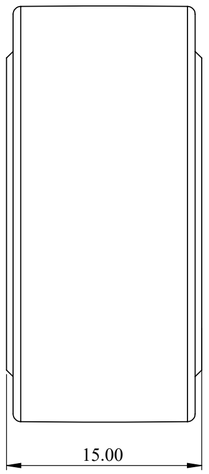

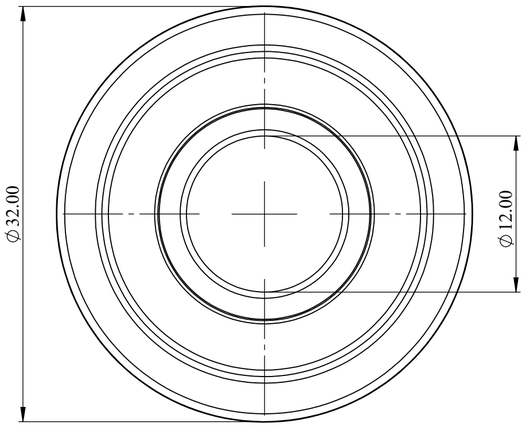

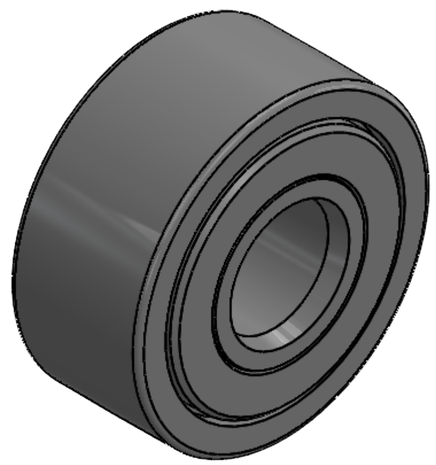

NOTE :

NOTE.:
NAME: BEARING NATR 12 (SKF)
SIZE : OD32 XID12 XW15 MM
QTY : 08 NO'S

SPECIAL INSTRUCTION'S :

TITLE - ROOF AUTOMATION

DWG NO - NTPL-000-PM-001-00-00-00

NIHVA Technologies Pvt. Ltd.

NIHVA TECHNOLOGIES PVT.LTD.PUNE
Website - www.nihva.com

	NAME	SIGNATURE	DATE
DRAWN	V.W.		01-04-2026
CHK'D	B.S.		03-04-2026
APPV'D	V.T.		03-04-2026


PRODUCT - SWIMMING POOL DECK
PROJECT NO - NTPL-000-PM
REVISION - 00
SITE LOCATION -
WEIGHT -
MATERIAL -
QTY - 1
SCALE :


If any queries contact - Design@nihva.com
ALL DIMENSION ARE IN mm
A2
PROJECTION METHOD:


DRAWING

REV DESCRIPTION	DATE	REV NO
	01-04-2026	REV 00
1.		

ITEM NO.	PART NUMBER	DESCRIPTION	QTY.
1	SHOULDER BOLT NATR 12 (M12X35 MM)	M12X35 MM	08

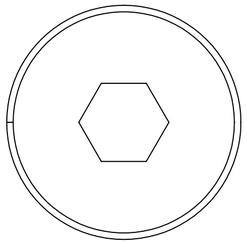

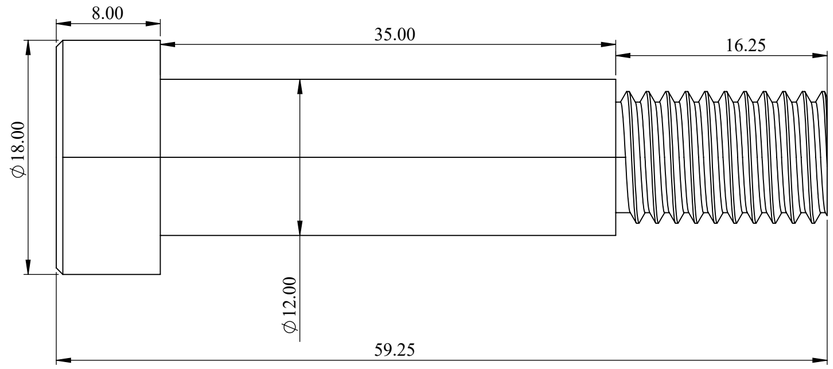

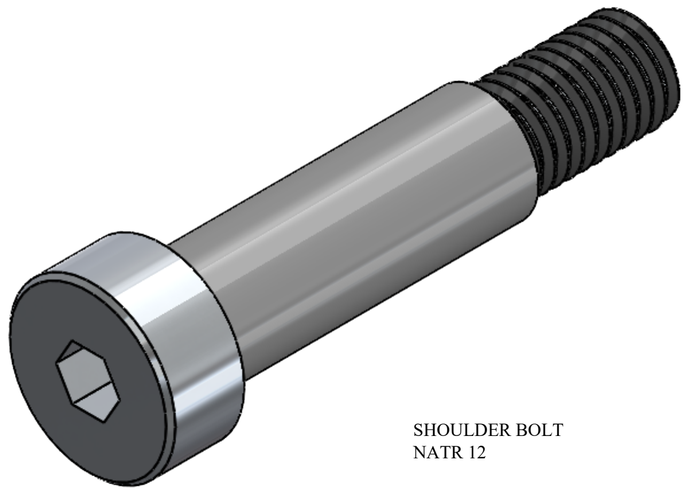

SHOULDER BOLT
NATR 12

NOTE :

NOTE.:
NAME: SHOULDER BOLT NATR 12
SIZE : M12 X 35 MM
QTY : 08 NO'S

SPECIAL INSTRUCTION'S :

TITLE - ROOF AUTOMATION

DWG NO - NTPL-000-PM-001-00-00-00

NIHVA Technologies Pvt. Ltd.

NIHVA TECHNOLOGIES PVT.LTD.PUNE
Website - www.nihva.com

	NAME	SIGNATURE	DATE
DRAWN	V.W.		01-04-2026
CHK'D	B.S.		03-04-2026
APPV'D	V.T.		03-04-2026

PRODUCT - SWIMMING POOL DECK

PROJECT NO - NTPL-000-PM | REVISION - 00

SITE LOCATION - | WEIGHT -

MATERIAL - | QTY - 1

If any queries contact - Design@nihva.com

ALL DIMENSION ARE IN mm | A2


PROJECTION METHOD:


SCALE :


DRAWING

REV DESCRIPTION	DATE	REV NO
	01-04-2026	REV 00
1.		

ITEM NO.	PART NUMBER	DESCRIPTION	QTY.
1	SKF_NATR 8	BRG(SIZE- OD24 X ID8 X W15 MM)	08

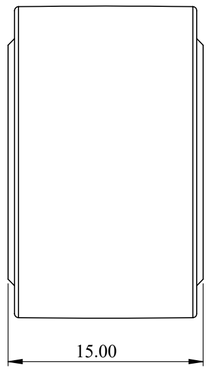

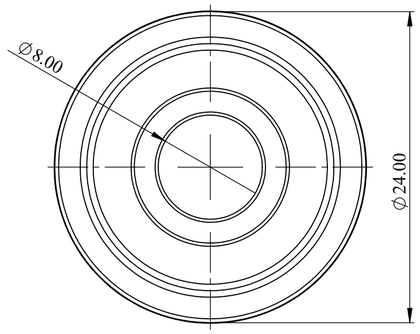

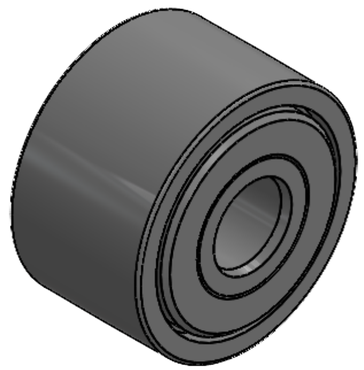

NOTE :

NOTE.:
NAME : BEARING NATR 8 (SKF)
SIZE : OD24 X ID8 XW15 MM
QTY : 08 NO'S

SPECIAL INSTRUCTION'S :

TITLE - ROOF AUTOMATION

DWG NO - NTPL-000-PM-001-00-00-00

	NAME	SIGNATURE	DATE
DRAWN	V.W.		01-04-2026
CHK'D	B.S.		03-04-2026
APPV'D	V.T.		03-04-2026

If any queries contact - Design@nihva.com

ALL DIMENSION ARE IN mm | A2

NIHVA TECHNOLOGIES PVT.LTD.PUNE
Website - www.nihva.com

PRODUCT - SWIMMING POOL DECK

PROJECT NO - NTPL-000-PM | REVISION - 00

SITE LOCATION - | WEIGHT -


MATERIAL - | QTY - 1


PROJECTION METHOD: | SCALE :


DRAWING

ITEM NO.	PART NUMBER	DESCRIPTION	QTY.
1	SHOULDER BOLT NATR 8 (M8X30 MM)	M8X30 MM	08

REV DESCRIPTION	DATE	REV NO
	01-04-2026	REV 00
1.		

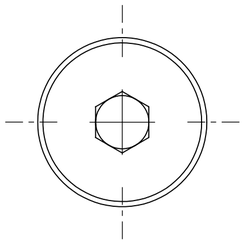

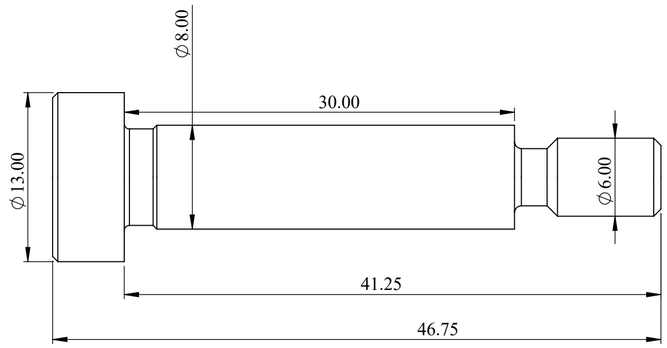

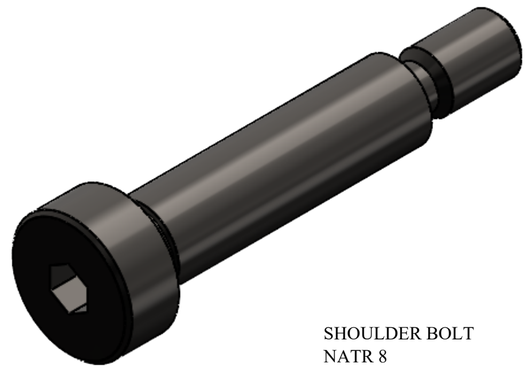

SHOULDER BOLT
NATR 8

NOTE :

NOTE.:
NAME: SHOULDER BOLT NATR 8
SIZE : M8 X 30 MM
QTY : 08 NO'S

SPECIAL INSTRUCTION'S :

TITLE - ROOF AUTOMATION

DWG NO - NTPL-000-PM-001-00-00-00

NIHVA Technologies Pvt. Ltd.

NIHVA TECHNOLOGIES PVT.LTD.PUNE
Website - www.nihva.com


	NAME	SIGNATURE	DATE
DRAWN	V.W.		01-04-2026
CHK'D	B.S.		03-04-2026
APPV'D	V.T.		03-04-2026

PRODUCT - SWIMMING POOL DECK
PROJECT NO - NTPL-000-PM
REVISION - 00
SITE LOCATION -
WEIGHT -
MATERIAL -
QTY - 1
If any queries contact - Design@nihva.com
PROJECTION METHOD:
SCALE :
ALL DIMENSION ARE IN mm
A2

DRAWING

REV DESCRIPTION	DATE	REV NO
	01-04-2026	REV 00
1.		

ITEM NO.	PART NUMBER	DESCRIPTION	QTY.
1	SS SHEET		1

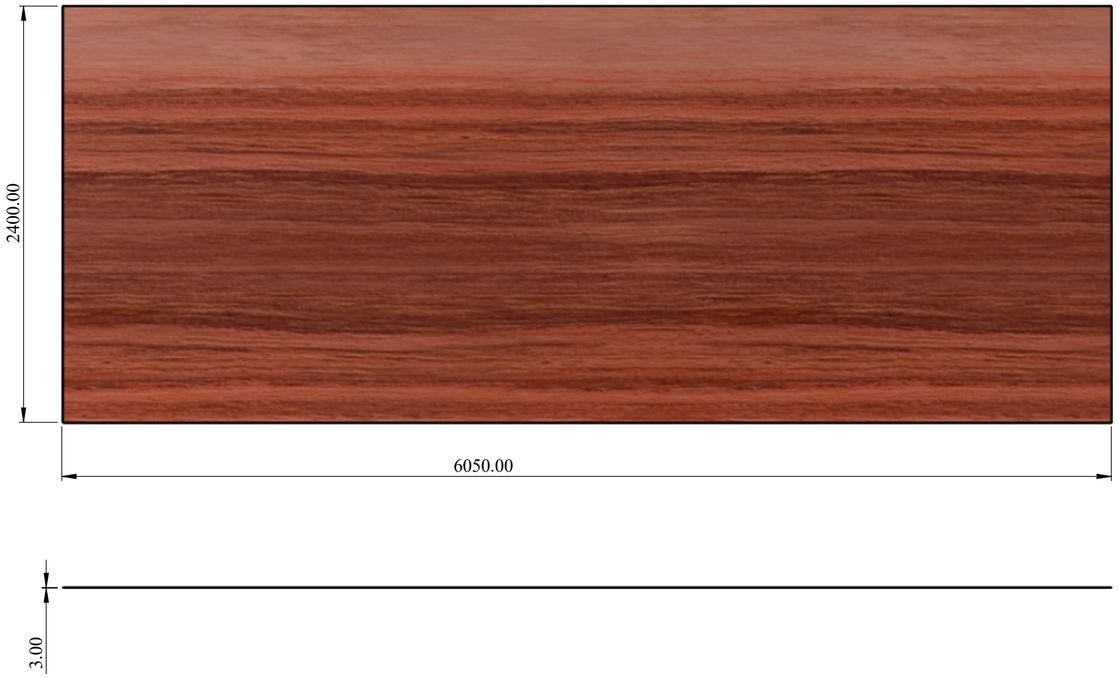

NOTE :

NOTE.:
NAME : SHEET
THK : 3 MM

SPECIAL INSTRUCTION'S :

TITLE - ROOF AUTOMATION

DWG NO - NTPL-000-PM-001-00-00-00

NIHVA Technologies Pvt. Ltd.

NIHVA TECHNOLOGIES PVT.LTD.PUNE
Website - www.nihva.com


	NAME	SIGNATURE	DATE
DRAWN	V.W.		01-04-2026
CHK'D	B.S.		03-04-2026
APPV'D	V.T.		03-04-2026


PRODUCT - SWIMMING POOL DECK
PROJECT NO - NTPL-000-PM
REVISION - 00
SITE LOCATION -
WEIGHT - 384 KG
MATERIAL - SS
QTY - 1
SCALE :


If any queries contact - Design@nihva.com
ALL DIMENSION ARE IN mm
A2
PROJECTION METHOD:

DRAWING


REV DESCRIPTION	DATE	REV NO
	01-04-2026	REV 00
1.		

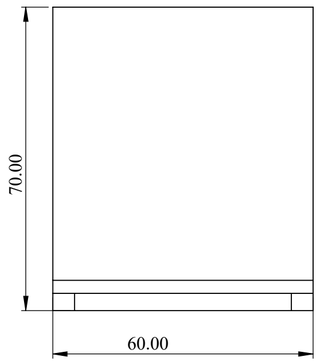


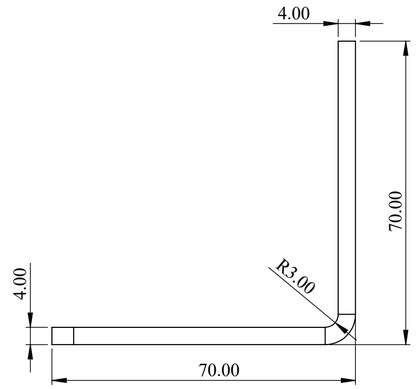

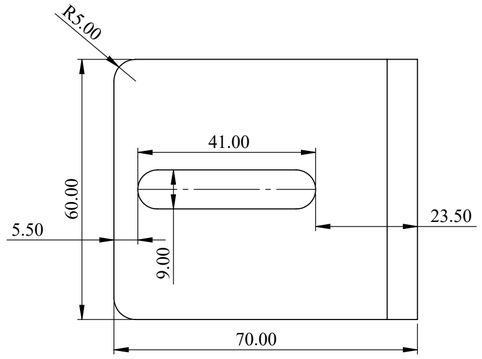

ITEM NO.	PART NUMBER	DESCRIPTION	QTY.
1	RACK SUPPORT PLATE	ss	08

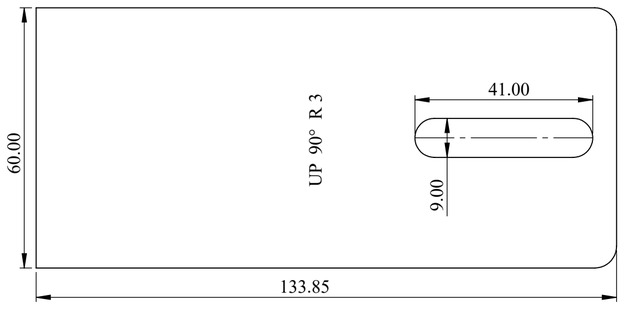

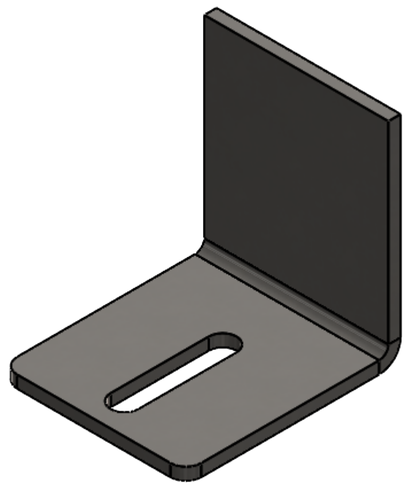

NOTE :

NOTE.:
NAME :RACK SUPPORT MTG PLATE
SIZE : W60 X L133.85 X 4 MM THK
MTL : SS
THK : 4 MM

SPECIAL INSTRUCTION'S :

TITLE - ROOF AUTOMATION

DWG NO - NTPL-000-PM-001-00-00-00

NIHVA Technologies Pvt. Ltd.


NIHVA TECHNOLOGIES PVT.LTD.PUNE
Website - www.nihva.com

	NAME	SIGNATURE	DATE	PRODUCT - SWIMMING POOL DECK	
DRAWN	V.W.		01-04-2026	PROJECT NO - NTPL-000-PM	REVISION - 00
CHK'D	B.S.		03-04-2026	SITE LOCATION -	WEIGHT -
APPV'D	V.T.		03-04-2026	MATERIAL -	QTY - 1
If any queries contact - Design@nihva.com				PROJECTION METHOD:	SCALE :
ALL DIMENSION ARE IN mm		A2			SHEET 12 OF 17

DRAWING

REV DESCRIPTION	DATE	REV NO
	01-04-2026	REV 00
1.		

ITEM NO.	PART NUMBER	DESCRIPTION	QTY.
1	RACK M6 MODULE	STD (M4 RACK, 30x8x1000 mm, ZINC COATED WITH SPACERS AND SCREWS.)	03

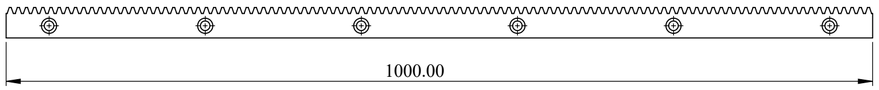

NOTE :

NOTE.:
NAME : RACK M6 MODULE (STD)
QTY : 03 NO'S.

SPECIAL INSTRUCTION'S :

TITLE - ROOF AUTOMATION

DWG NO - NTPL-000-PM-001-00-00-00

NIHVA Technologies Pvt. Ltd.

NIHVA TECHNOLOGIES PVT.LTD.PUNE
Website - www.nihva.com

	NAME	SIGNATURE	DATE
DRAWN	V.W.		01-04-2026
CHK'D	B.S.		03-04-2026
APPV'D	V.T.		03-04-2026

PRODUCT - SWIMMING POOL DECK

PROJECT NO - NTPL-000-PM | REVISION - 00

SITE LOCATION - | WEIGHT -

MATERIAL - | QTY - 1

If any queries contact - Design@nihva.com

ALL DIMENSION ARE IN mm | A2


PROJECTION METHOD:


SCALE :


DRAWING


REV DESCRIPTION	DATE	REV NO
	01-04-2026	REV 00
1.		

ITEM NO.	PART NUMBER	DESCRIPTION	QTY.
1	NCE_RUN_1800KG.		1

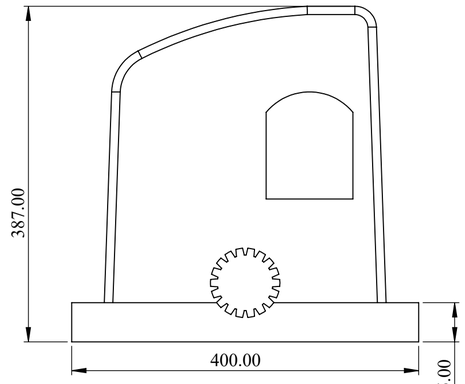

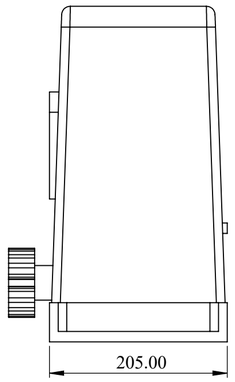

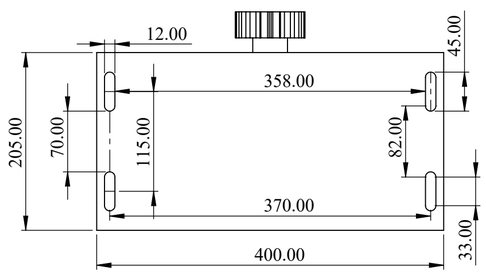

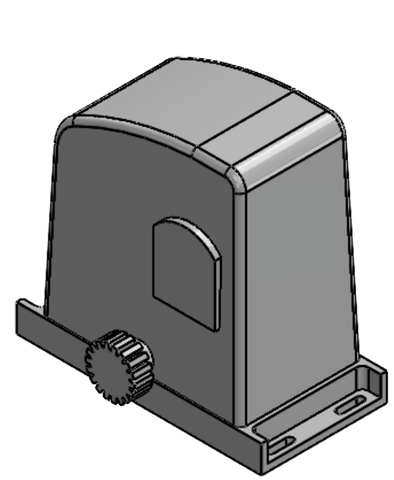

NOTE :

NOTE.:
NAME: NICE MOTOR
CAPACITY : 1800 KG
QTY : 1NO

SPECIAL INSTRUCTION'S :

TITLE - ROOF AUTOMATION

DWG NO - NTPL-000-PM-001-00-00-00

NIHVA Technologies Pvt. Ltd.

NIHVA TECHNOLOGIES PVT.LTD.PUNE
Website - www.nihva.com

	NAME	SIGNATURE	DATE		
DRAWN	V.W.		01-04-2026	PROJECT NO - NTPL-000-PM	REVISION - 00
CHK'D	B.S.		03-04-2026	SITE LOCATION -	WEIGHT -
APPV'D	V.T.		03-04-2026	MATERIAL -	QTY - 1

If any queries contact - Design@nihva.com

ALL DIMENSION ARE IN mm | A2

PROJECTION METHOD:


SCALE :


SHEET 14 OF 17

DRAWING

REV DESCRIPTION	DATE	REV NO
	01-04-2026	REV 00
1.		

ITEM NO.	PART NUMBER	DESCRIPTION	QTY.
1	MOTOR BASE PALTE		1

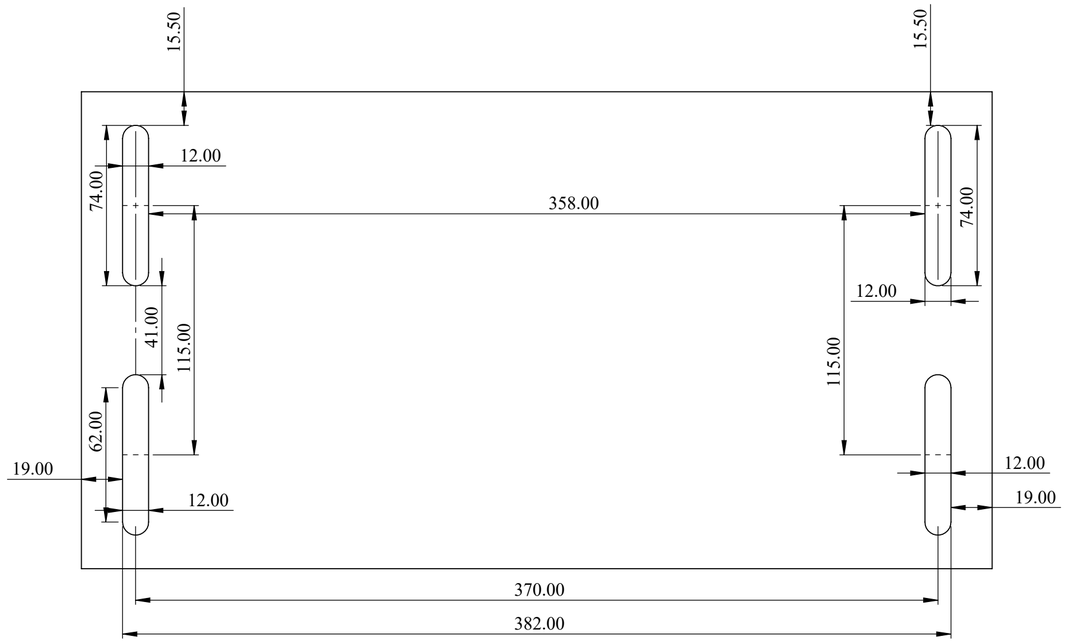

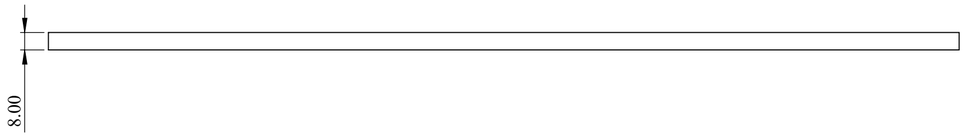

NOTE :

NOTE.:
NAME :MOTOR BASE PLATE
MTL : SS
THK : 8 MM

SPECIAL INSTRUCTION'S :

TITLE - ROOF AUTOMATION

DWG NO - NTPL-000-PM-001-00-00-00

NIHVA Technologies Pvt. Ltd.

NIHVA TECHNOLOGIES PVT.LTD.PUNE
Website - www.nihva.com

	NAME	SIGNATURE	DATE
DRAWN	V.W.		01-04-2026
CHK'D	B.S.		03-04-2026
APPV'D	V.T.		03-04-2026


PRODUCT - SWIMMING POOL DECK
PROJECT NO - NTPL-000-PM
REVISION - 00
SITE LOCATION -
WEIGHT - 5.694 KG
MATERIAL - SS
QTY - 1
SCALE :


If any queries contact - Design@nihva.com
ALL DIMENSION ARE IN mm
A2
PROJECTION METHOD:


DRAWING

ITEM NO.	PART NUMBER	DESCRIPTION	QTY.
1	TRACK ASSEMBLY.		2

REV DESCRIPTION	DATE	REV NO
	01-04-2026	REV 00
1.		

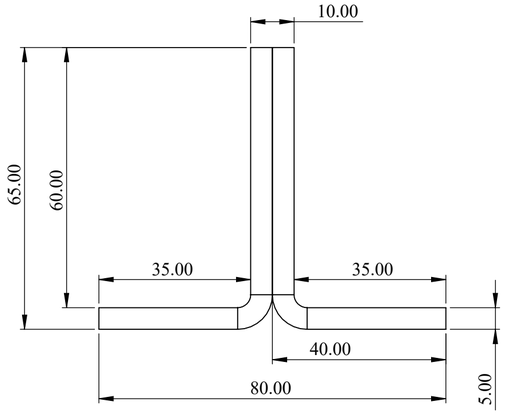

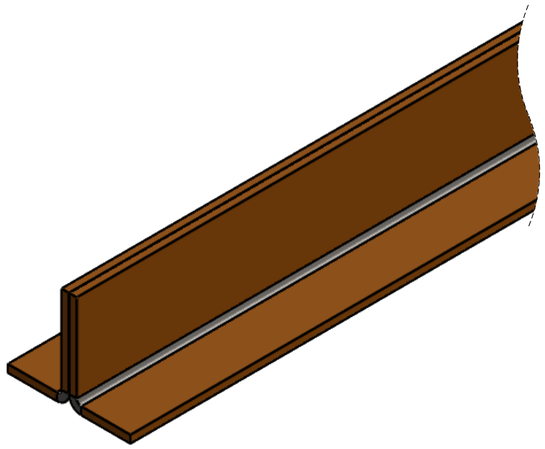

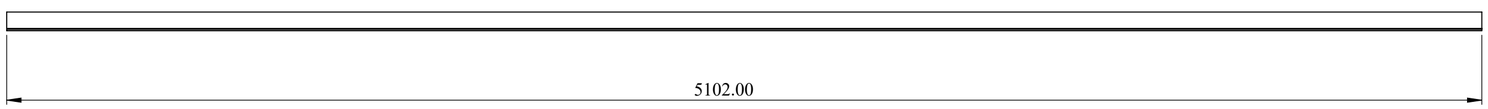

NOTE :

NOTE.:
NAME : TRACK ASSEMBLY
SIZE : W80 X H65 MM
QTY : 2 NOS
MTL : SS

SPECIAL INSTRUCTION'S :

TITLE - ROOF AUTOMATION

DWG NO - NTPL-000-PM-001-00-00-00

NIHVA Technologies Pvt. Ltd.


NIHVA TECHNOLOGIES PVT.LTD.PUNE
Website - www.nihva.com


	NAME	SIGNATURE	DATE
DRAWN	V.W.		01-04-2026
CHK'D	B.S.		03-04-2026
APPV'D	V.T.		03-04-2026

PRODUCT - SWIMMING POOL DECK
PROJECT NO - NTPL-000-PM | REVISION - 00
SITE LOCATION - | WEIGHT -
MATERIAL - | QTY - 1
If any queries contact - Design@nihva.com
ALL DIMENSION ARE IN mm | A2
PROJECTION METHOD:
SCALE :
SHEET 16 OF 17

DRAWING

REV DESCRIPTION	DATE	REV NO
	01-04-2026	REV 00
1.		

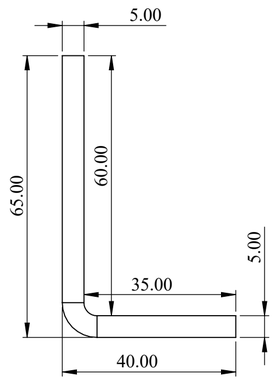

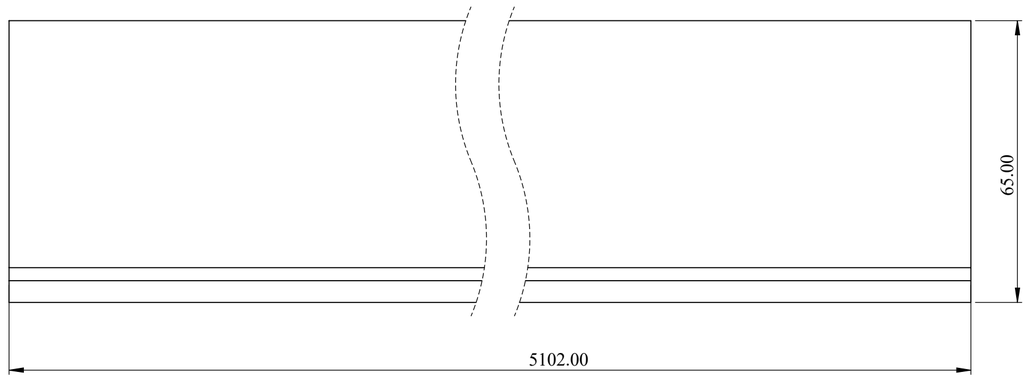

NOTE :

NOTE.:
NAME : TRACK
SIZE : W40 X H65 MM
QTY : 04 NOS

SPECIAL INSTRUCTION'S :

TITLE - ROOF AUTOMATION

DWG NO - NTPL-000-PM-001-00-00-00

NIHVA Technologies Pvt. Ltd.

NIHVA TECHNOLOGIES PVT.LTD.PUNE
Website - www.nihva.com

	NAME	SIGNATURE	DATE
DRAWN	V.W.		01-04-2026
CHK'D	B.S.		03-04-2026
APPV'D	V.T.		03-04-2026

PRODUCT - SWIMMING POOL DECK

PROJECT NO - NTPL-000-PM | REVISION - 00

SITE LOCATION - | WEIGHT -

MATERIAL - | QTY - 1

If any queries contact - Design@nihva.com

PROJECTION METHOD:

SCALE :

ALL DIMENSION ARE IN mm | A2