


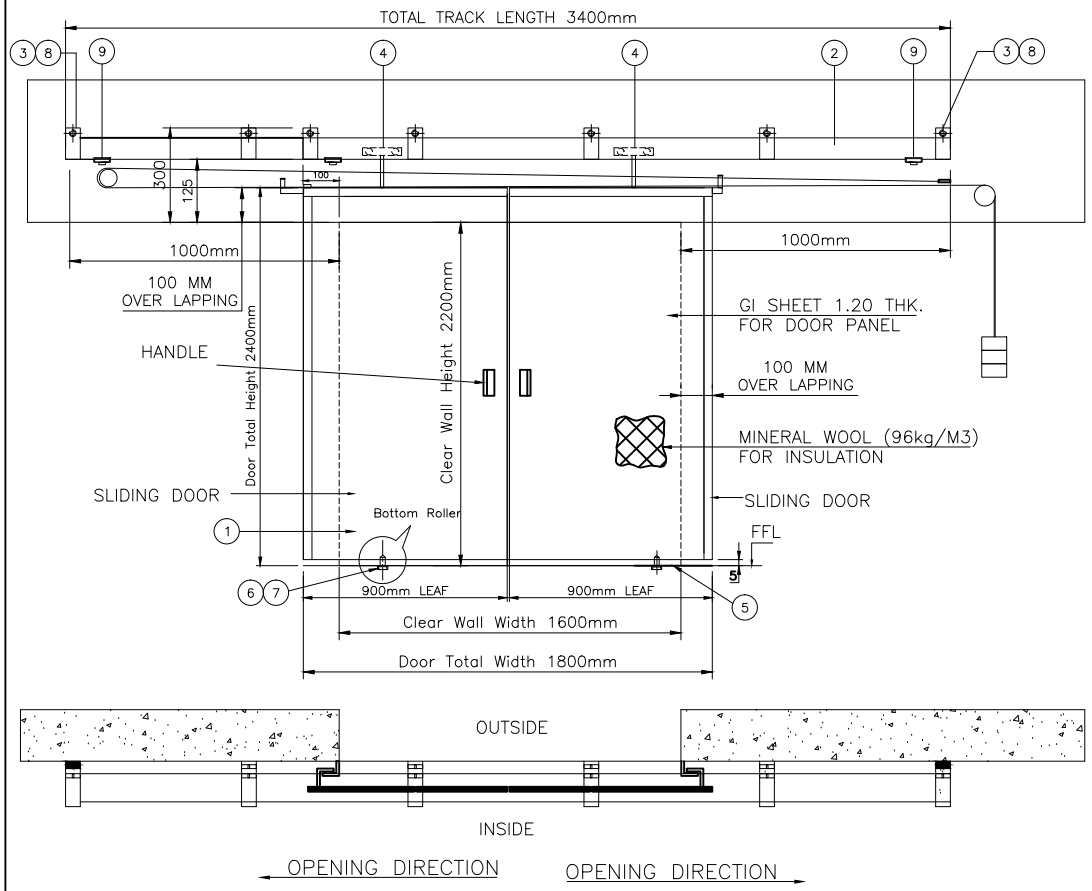


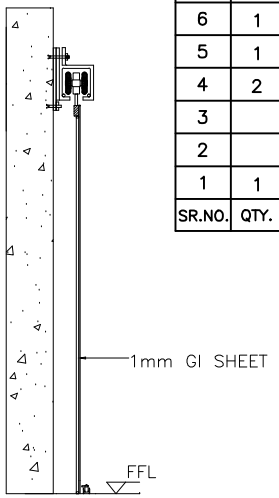

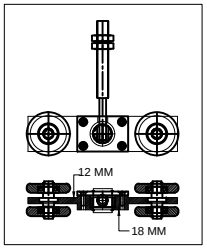

DETAIL AT 'B'

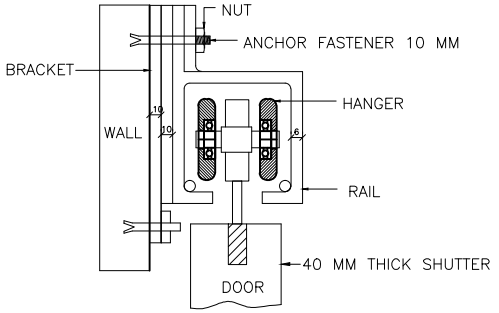

SR.NO.	QTY.	DESCRIPTION
9	1	STOPPER (FOR HANGER ASSLY.)
8	1	COVER (FOR TRACK BKT.)
7	1	BOTTOM ROLLER MTG. FLAT (BOTTOM ROLLER BKT.)
6	1	BOTTOM ROLLER ASSLY.
5	1	'Z' SECTION
4	2	HANGER ROLLER ASSLY./PANEL
3		TRACK BRACKET
2		SLIDING TRACK
1	1	SLIDING DOOR & FRAME / BACK SUPPORT SQ. TUBE

DOOR DIMENSION		
CLEAR WIDTH	CLEAR HEIGHT	
1600mm	2200mm	03 NOS

Panel Make : - Radient Safe Door Make

NOTE : DOOR OVERLAPING 100mm AT RH & LH AND TOP SIDE
ALL DIMENSIONS ARE IN MM.
CLIENT SHOULD CONFIRM DOOR OPENING DIRECTION.

TOLERANCE:- ± 10mm

This drawing & designing is the property of NIHVA TECHNOLOGIES. Not to be sold or copied to any other concern.

TITLE
AUTOMATIC SLIDING DOOR

NIHVA TECHNOLOGIES PVT. LTD.

NIHVA TECHNOLOGIES PVT. LTD. PUNE
Tel : 020 66304033
Website:- www.nihva.com
Email:- info@nihva.com

	NAME	SIGN	DATE
DRAWN	P.V.A		03.10.19
CHECK	G.J		03.10.19
APPROVAL			

If any queries contact : design@nihva.com
ALL DIMENSION ARE IN mm

CLIENT - RATNARUP PROJECT PVT. LTD.
PROJECT -RATNARUP PROJECT PVT. LTD.
SITE - BANNER,PUNE.
DWG. NO. : NIHVA/19-20/0113 REV-R0
SCALE: NTS WT: SHEET: 01 OF 01