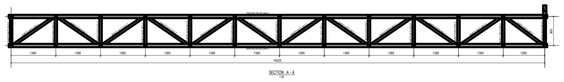
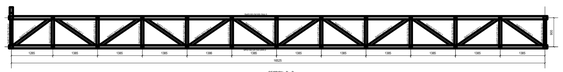
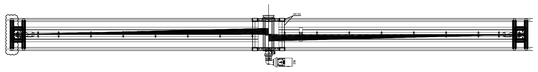
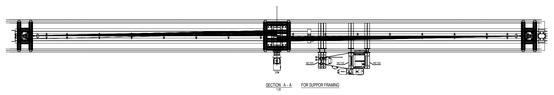
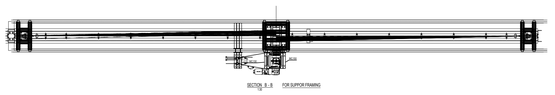

SECTION E-E

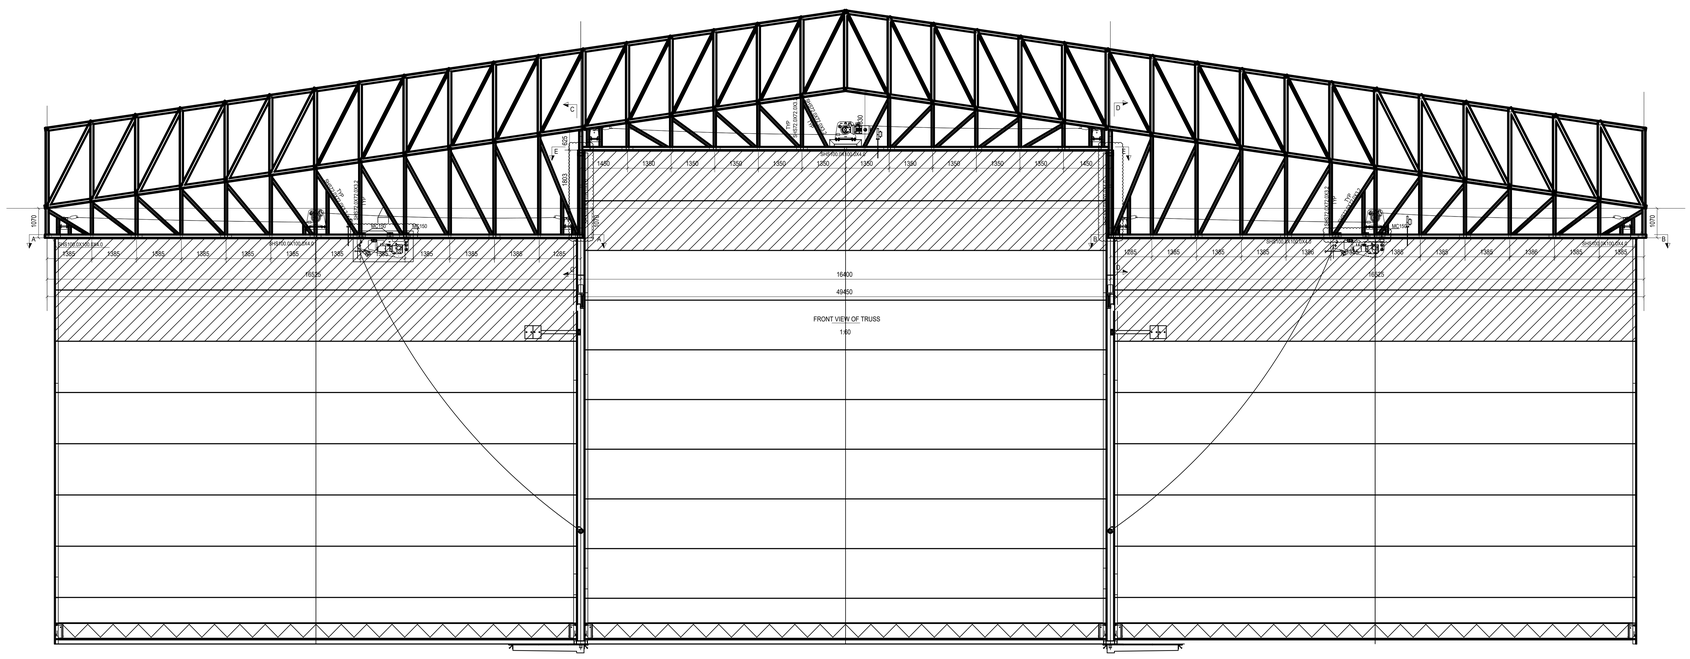

SECTION A-A

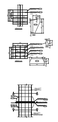

SECTION B-B


SECTION E-E FOR SUPPOR FRAMING

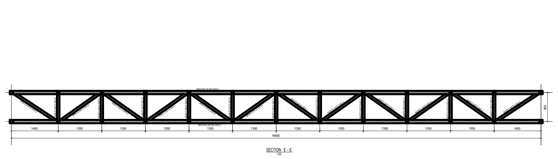

SECTION A-A FOR SUPPOR FRAMING

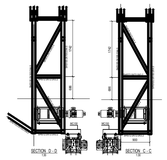

SECTION B-B FOR SUPPOR FRAMING

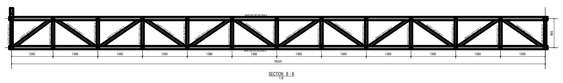

16400
40450
FRONT VIEW OF TRUSS
1:60

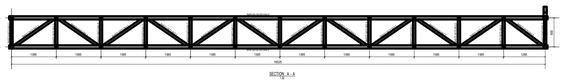





SECTION E-E


SECTION D-D
SECTION C-C


SECTION B-B


SECTION A-A