


PRODUCED BY AN AUTODESK EDUCATIONAL PRODUCT

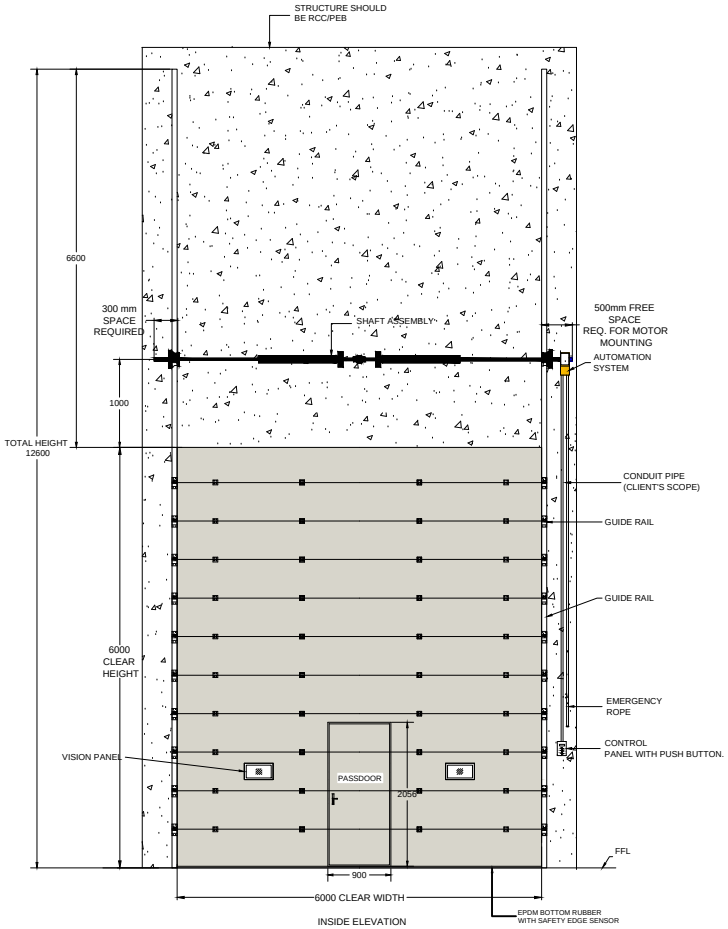


INSIDE ELEVATION

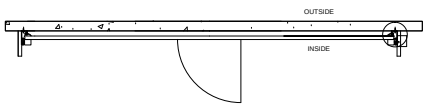

PLAN

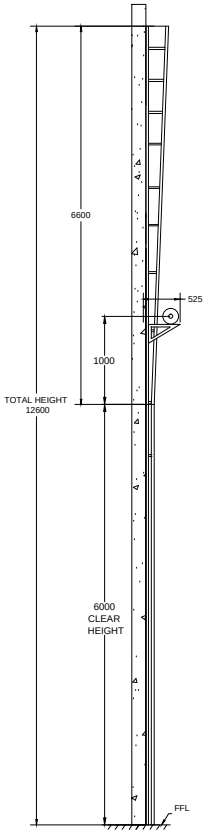

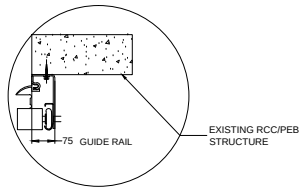

TRACK DETAILS

Pass door size- 900 (W) X 2056 (H)mm
Position of passdoor - At centre

DIMENSION :

CLEAR WIDTH	CLEAR HEIGHT	QUANTITY
6000 mm	6000 mm	14

TECHNICAL DATA :

COMPONENTS	MATERIALS	SPECIFICATIONS
DOOR PANELS	GI & PUF	42mm CFC- FREE POLYURETHANE WITH 0.5mm THK, GI PRECOATED PANELS.
DOOR HINGE	——	HEAVY DUTY HINGES FOR INTERLOCKING OF PANELS
SHAFT ASSEMBLY	STD.	TORSIONAL SPRING WITH SHAFT & BEARING PLATES
FINISH		PANELS ARE IN STANDARD RAL 9002 GREY WHITE COLOR

ACCESSORIES-
1. SAFETY EDGE SENSOR.

IMPORTANT NOTES:
1. REQUIRED STRUCTURE FOR DOOR SHALL BE IN CLIENT'S SCOPE.
2.SINGLE PHASE POWER SUPPLY REQUIRED AT DOOR LOCATION.
3.ALL CIVIL WORK SHALL BE CLIENT'S SCOPE.

NIHVA
NIHVA TECHNOLOGIES PVT. LTD.
NIHVA TECHNOLOGIES PVT. LTD. PUNE
Email:- info@nihva.com
Website:- www.nihva.com

TITLE:

SECTIONAL DOOR VL (MOTORIZED)

CLIENT'S APPROVAL :

CLIENT - INTERARCH BUILDING PRODUCTS PVT LTD

PROJECT -

SITE LOCATION - INDOR

DWG. NO. : NIHVA/18-19/0187 | REV- 0

SCALE: NTS | WT: | SHEET:1 OF 1

	NAME	DATE	SIGN
DRAWN	A.K.	30-11-2018	
CHECK	P.A.	30-11-2018	
APPROVAL	R.D.	30-11-2018	

If any queries contact : design@nihva.com

NOTE: ALL DIMENSIONS ARE IN mm

PRODUCED BY AN AUTODESK EDUCATIONAL PRODUCT

PRODUCED BY AN AUTODESK EDUCATIONAL PRODUCT