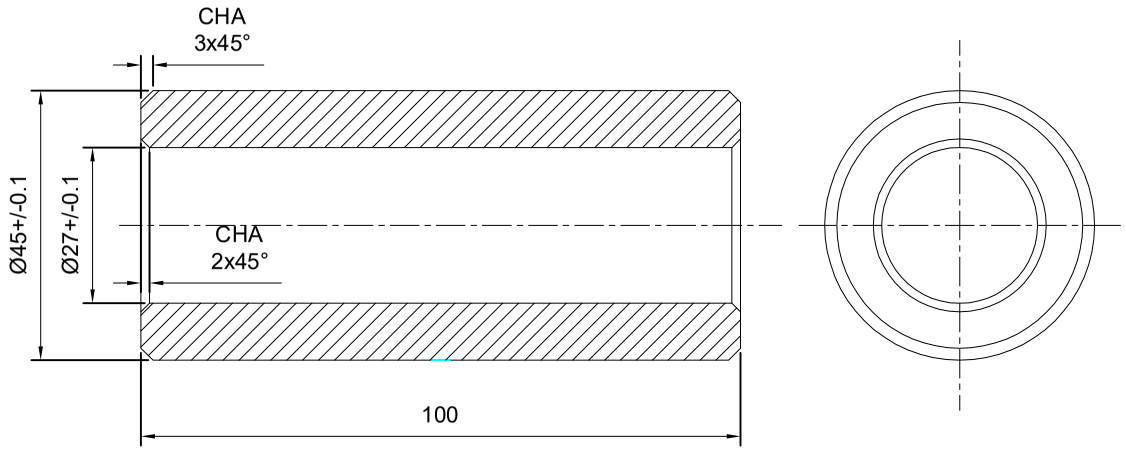


NOTE:~ MTL : MS

BUSH Ø45 X 100L = 18 NOS

NOTE : ~ PLEASE MAINTAIN 7 MM GAP BETWEEN TWO LIP BUSHES.

This drawing & design is the property of NIHVA TECHNOLOGIES. Not to be sold or copied to any other concern.

TITLE				
LIP MOUNTING BUSH				NIHVA TECHNOLOGIES PVT. LTD. PUNE Tel : 020 66304033 Email:- info@nihva.com Website:- www.nihva.com
	NAME	DATE	SIGN	
DRAWN	SUJATA	20/11/2021		CLIENT -
CHECK	G.PATIL	20/11/2021		PROJECT -
APPRD.	A.K	20/11/2021		SITE LOCATION -
If any queries contact : design@nihva.com				DWG. NO. : NIHVA/21-22/VDR/001
ALL DIMENSION ARE IN mm				SCALE: NTS / WT: / REV- 0